




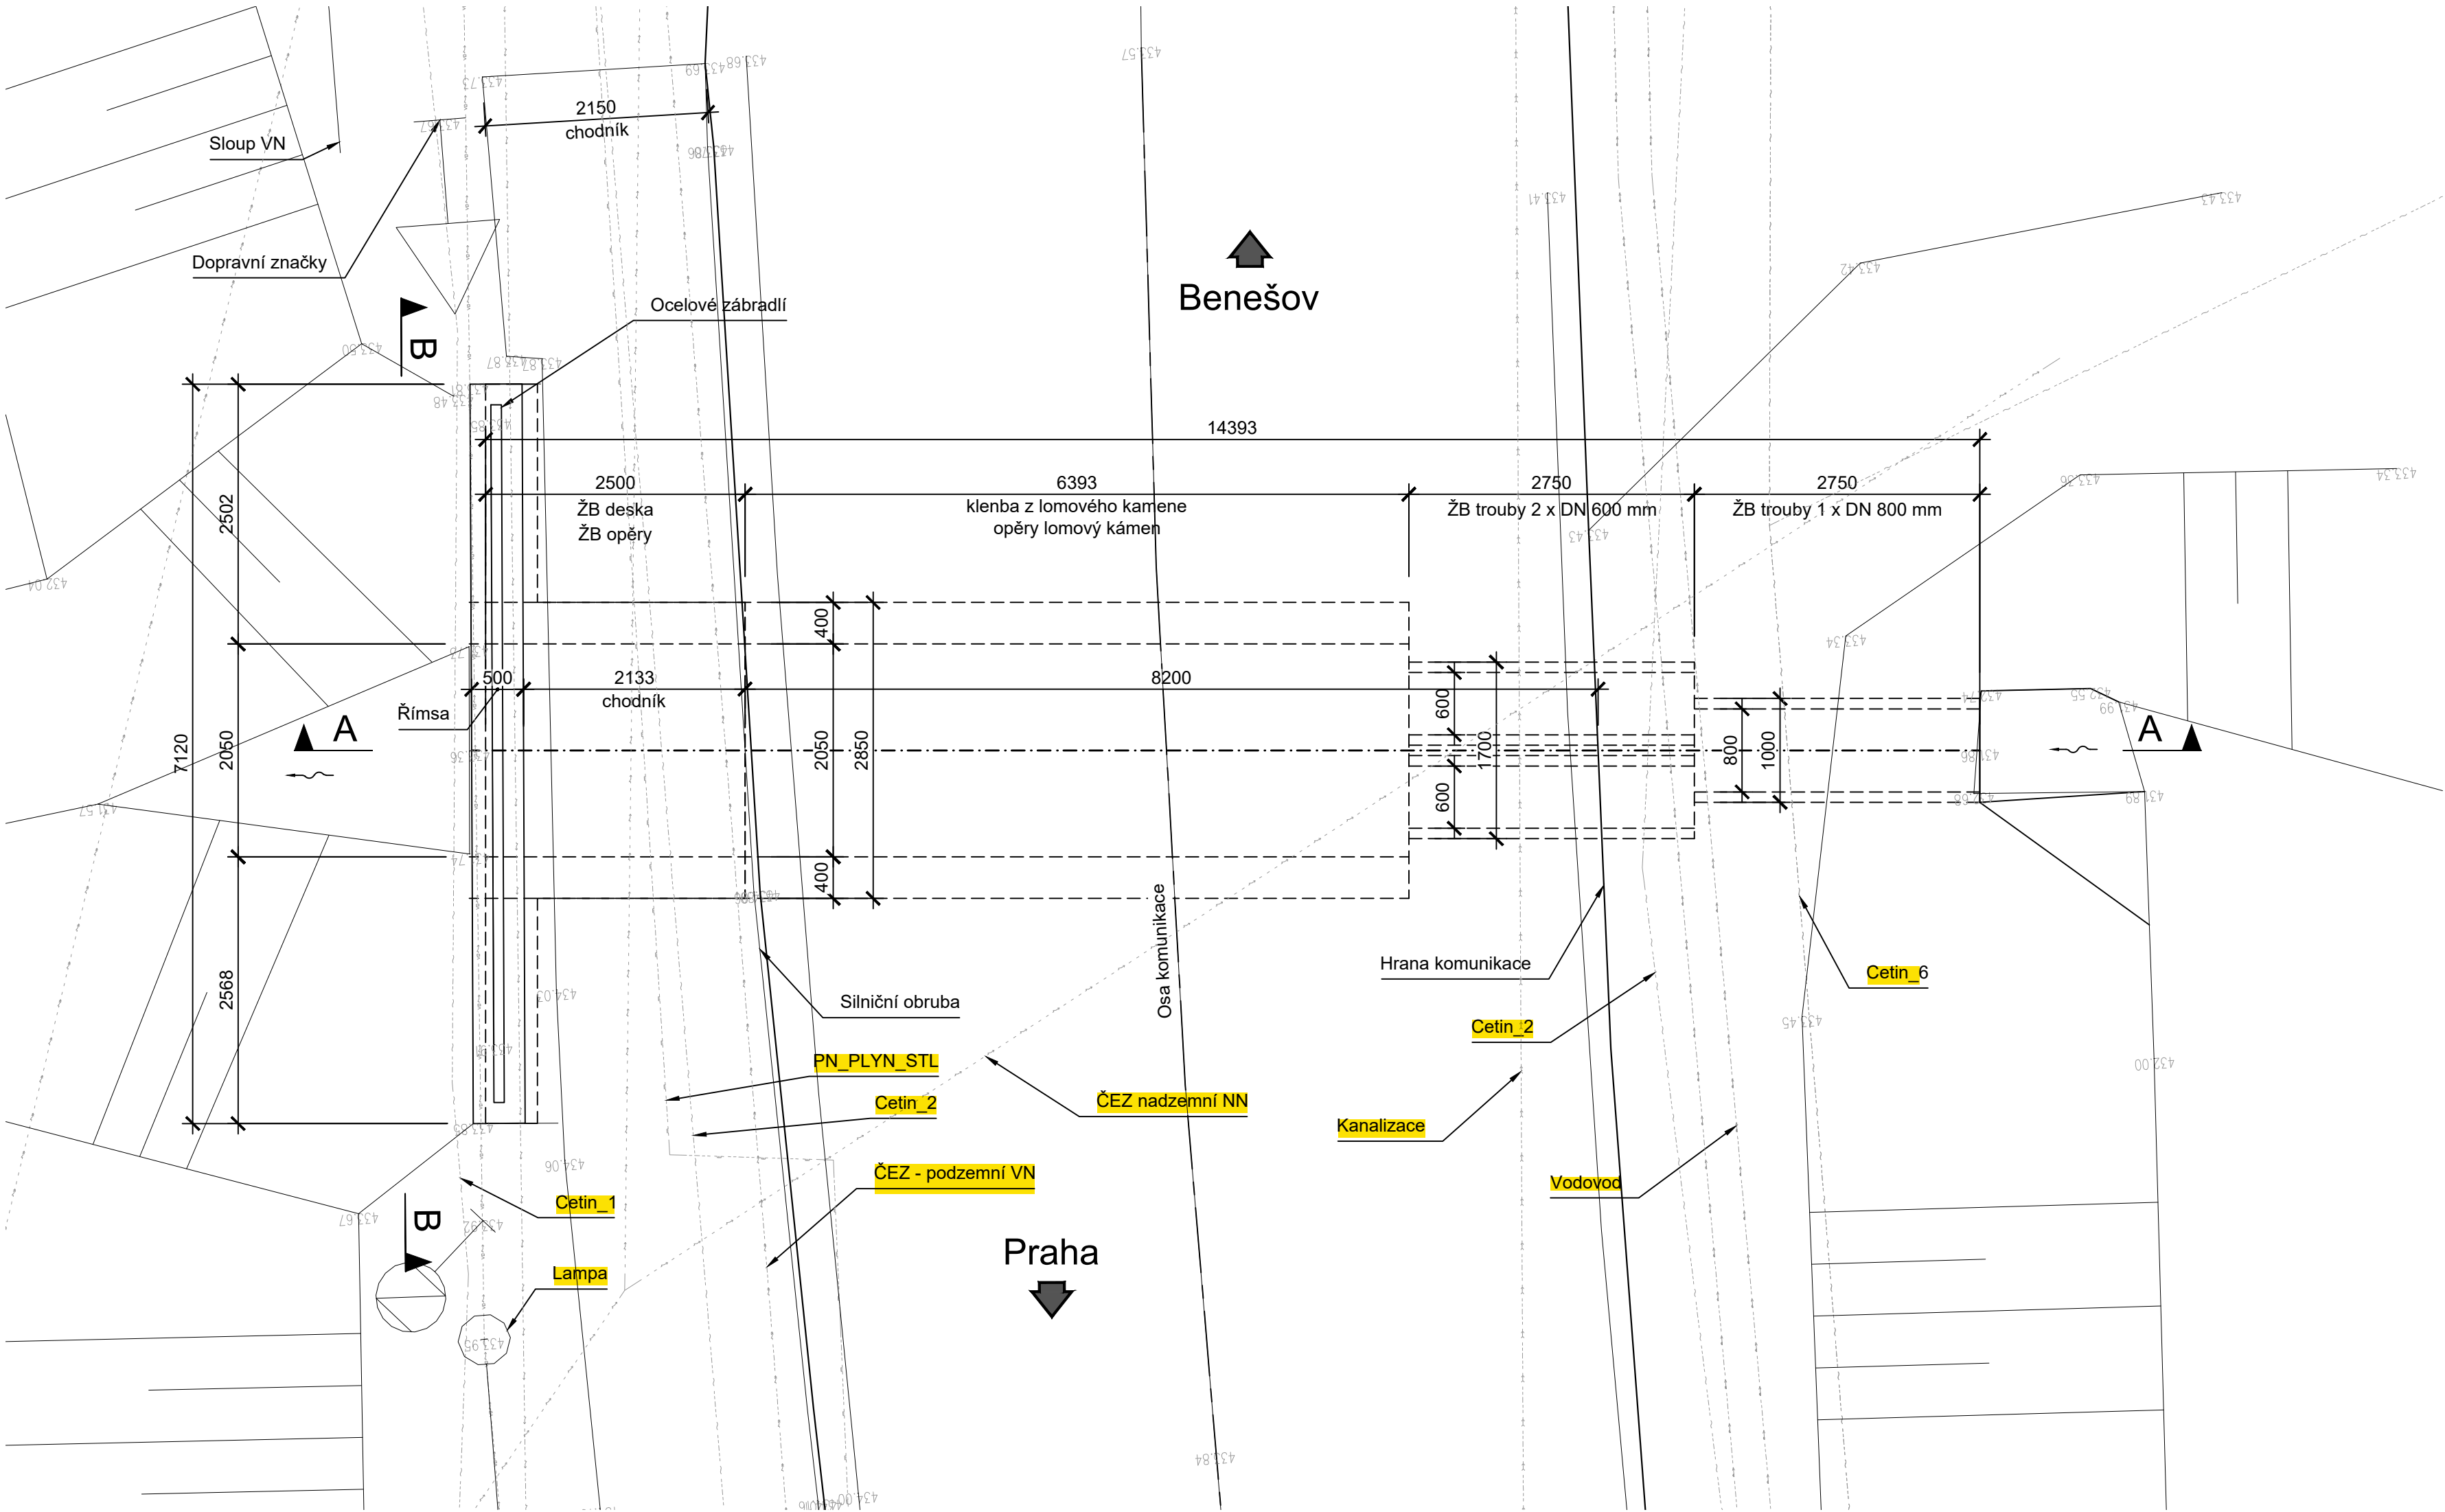

Řez B
1:50

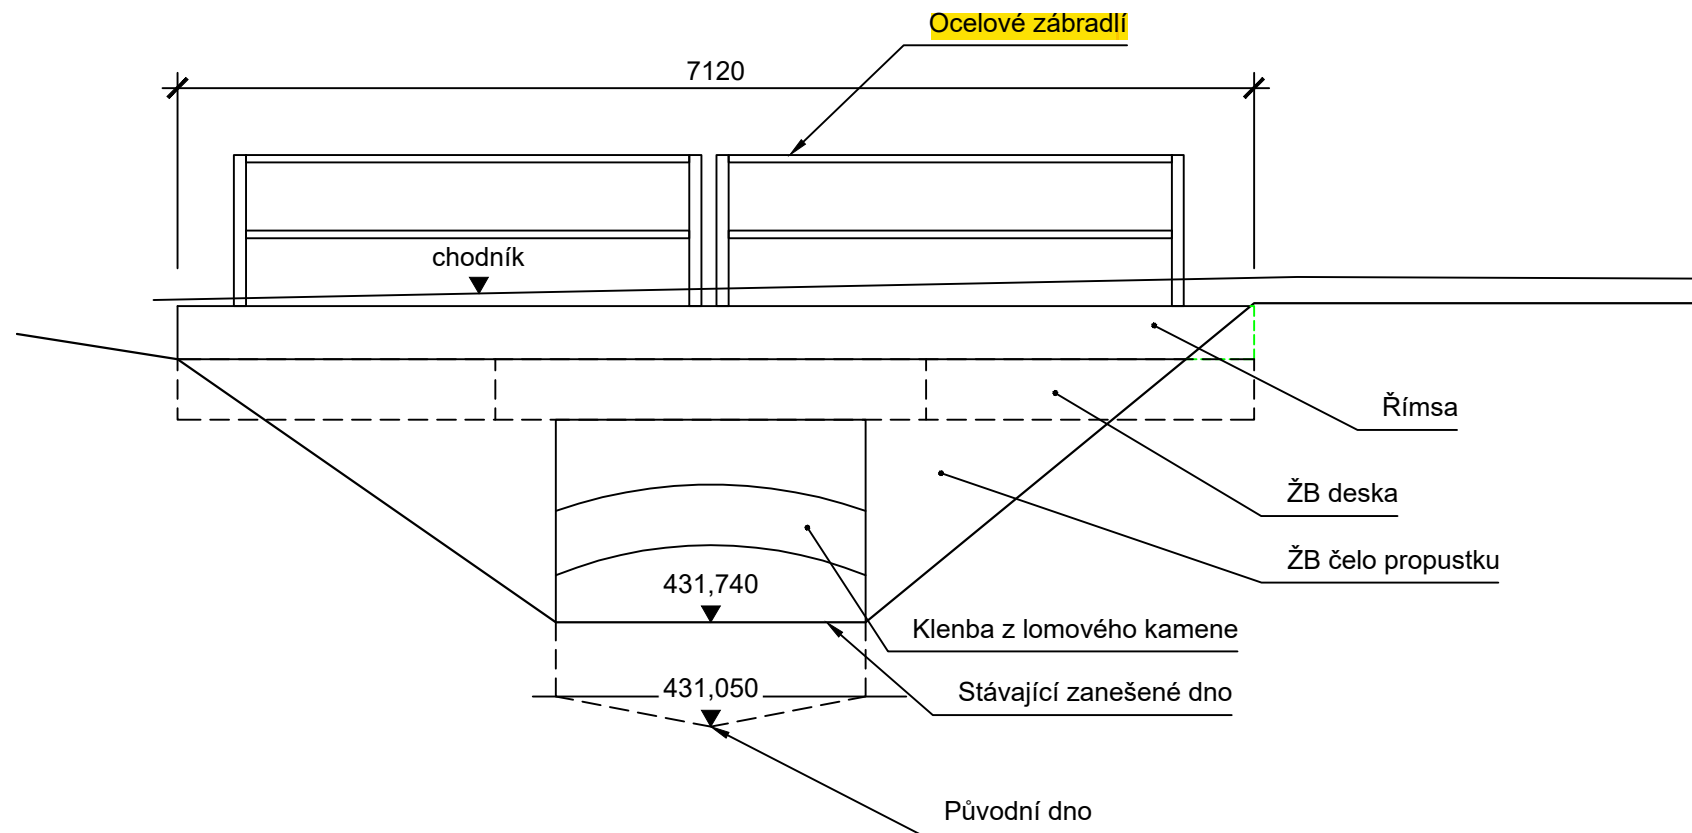

Řez A
1:50

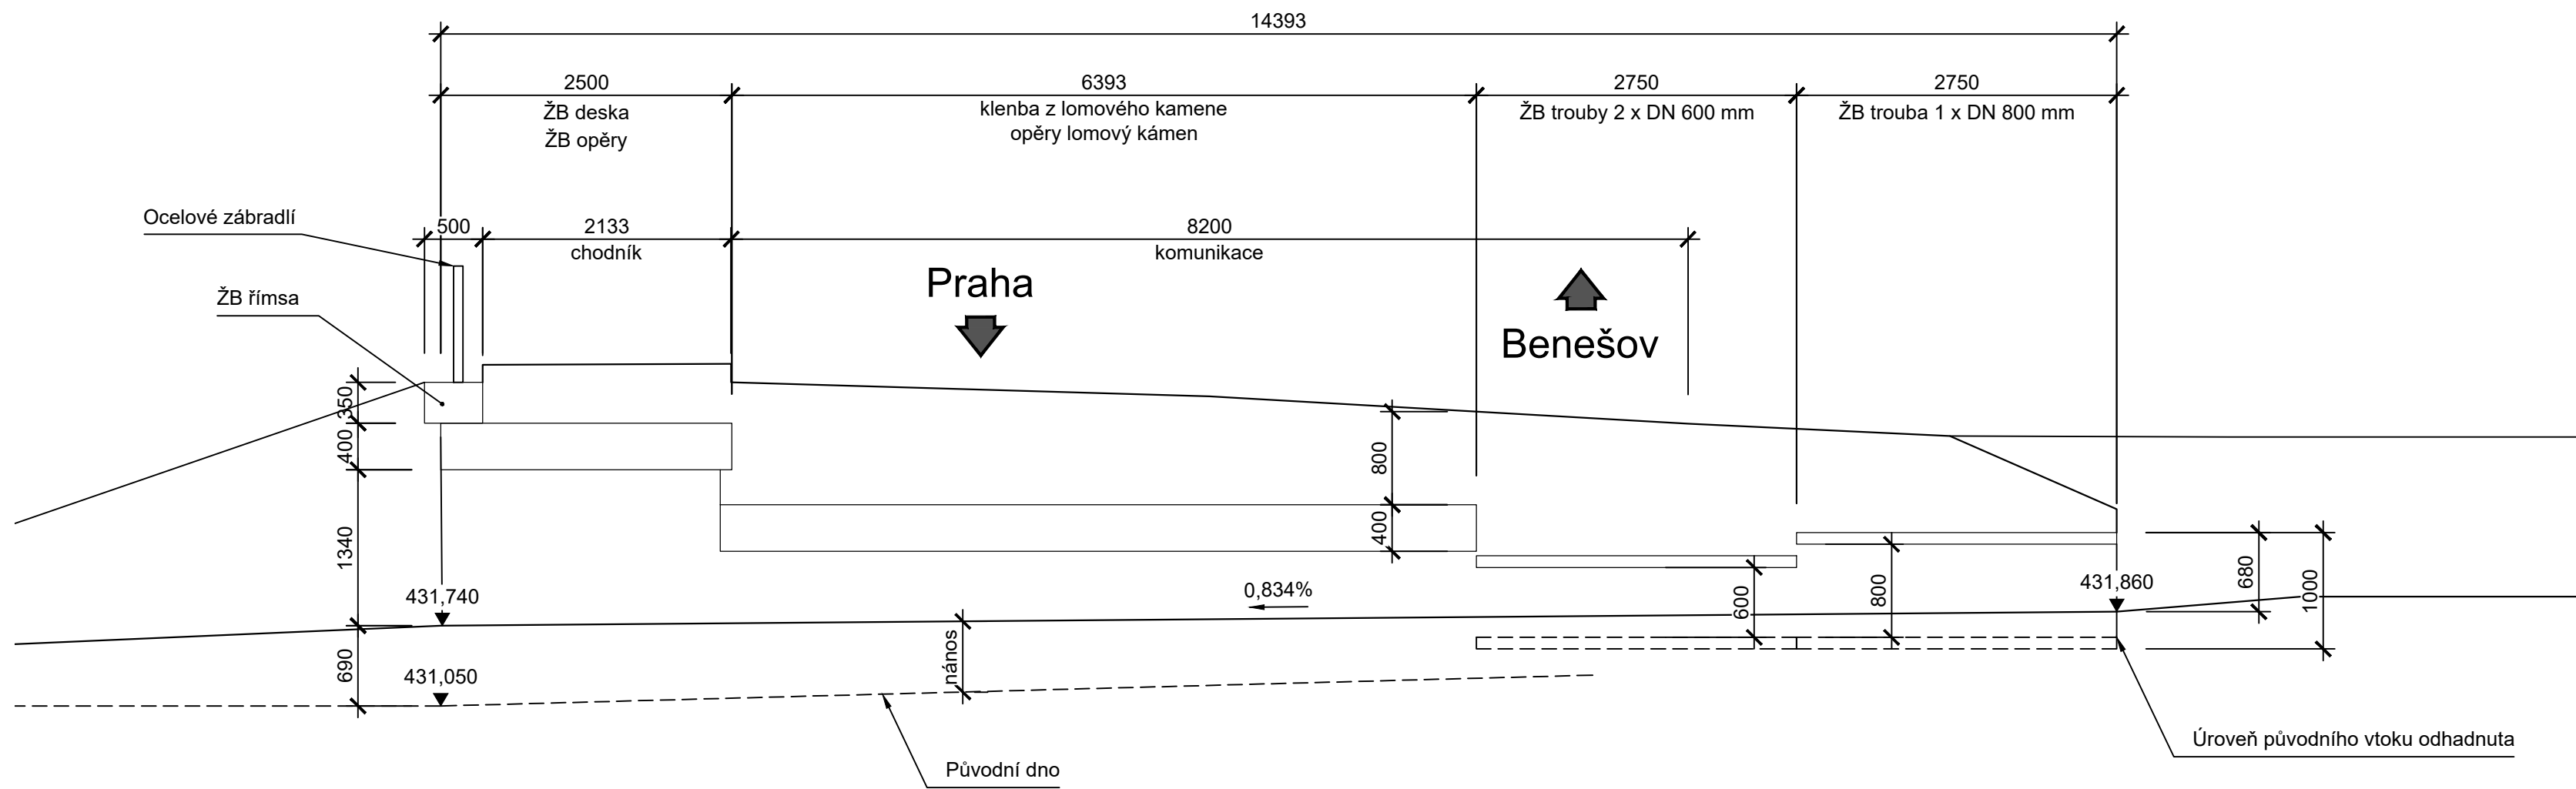

Poznámky:

- Demolice mostu bude probíhat za úplného vyloučení provozu.
- Všechny inženýrské sítě budou před zahájením prací přeloženy nebo ochráněny (viz samostatné stavební objekty)
- Koryto vodoteče bude provizorně zatrubněno.
- Rozsah bourání spodní stavby bude upřesněn po odkrytí konstrukce. Přesný tvar není znám protože se nedohovala archivní dokumentace mostu.
- Zhotovitel zpracuje technologický postup, který musí být před zahájením prací schválen TDI.

Souřadnicový systém S-JTSK, Výškový systém Bpv

Objednatel:	Středočeský kraj Zborovská 81/11, 150 21 Praha 5		Středočeský kraj	
-------------	--	--	------------------	--

Navrhl/vypracoval:	Zodpovědný projektant:	Zhotovitel:
Ing. Petr Nehasil	Ing. Petr Nehasil	Mott MacDonald CZ, spol. s r.o.
Technická kontrola:	Hlavní inženýr projektu:	M MOTT MACDONALD Národní 984/15 110 00 Praha 1 +420 221412800
Ing. Dušan Cichra	Ing. Dušan Cichra	

Kraj: Středočeský kraj	Čís.s.m.obj.:	S-1181/DOP/2019
Katastrální území: Sulice[759431], Střelná[662496], Ládví [5662445]	Čís.oke:	390474
Akce: II/603 Sulice- Želivec, rekonstrukce silnice a mostů	Datum:	07/2024
	Formát:	Bx44
	Měřítko:	1:50
	Stupeň:	Číslo kopie:
Část: SO 004 Demolice - most 603-010	PDPS	
	Číslo přílohy:	
	D.004-2	