




- OBRUBNÍK PŘÍMÝ
- OBRUBNÍK PŘÍMÝ SNÍŽENÝ
- OBRUBNÍK OBLOUKOVÝ
- OBRUBNÍK NÁBĚHOVÝ

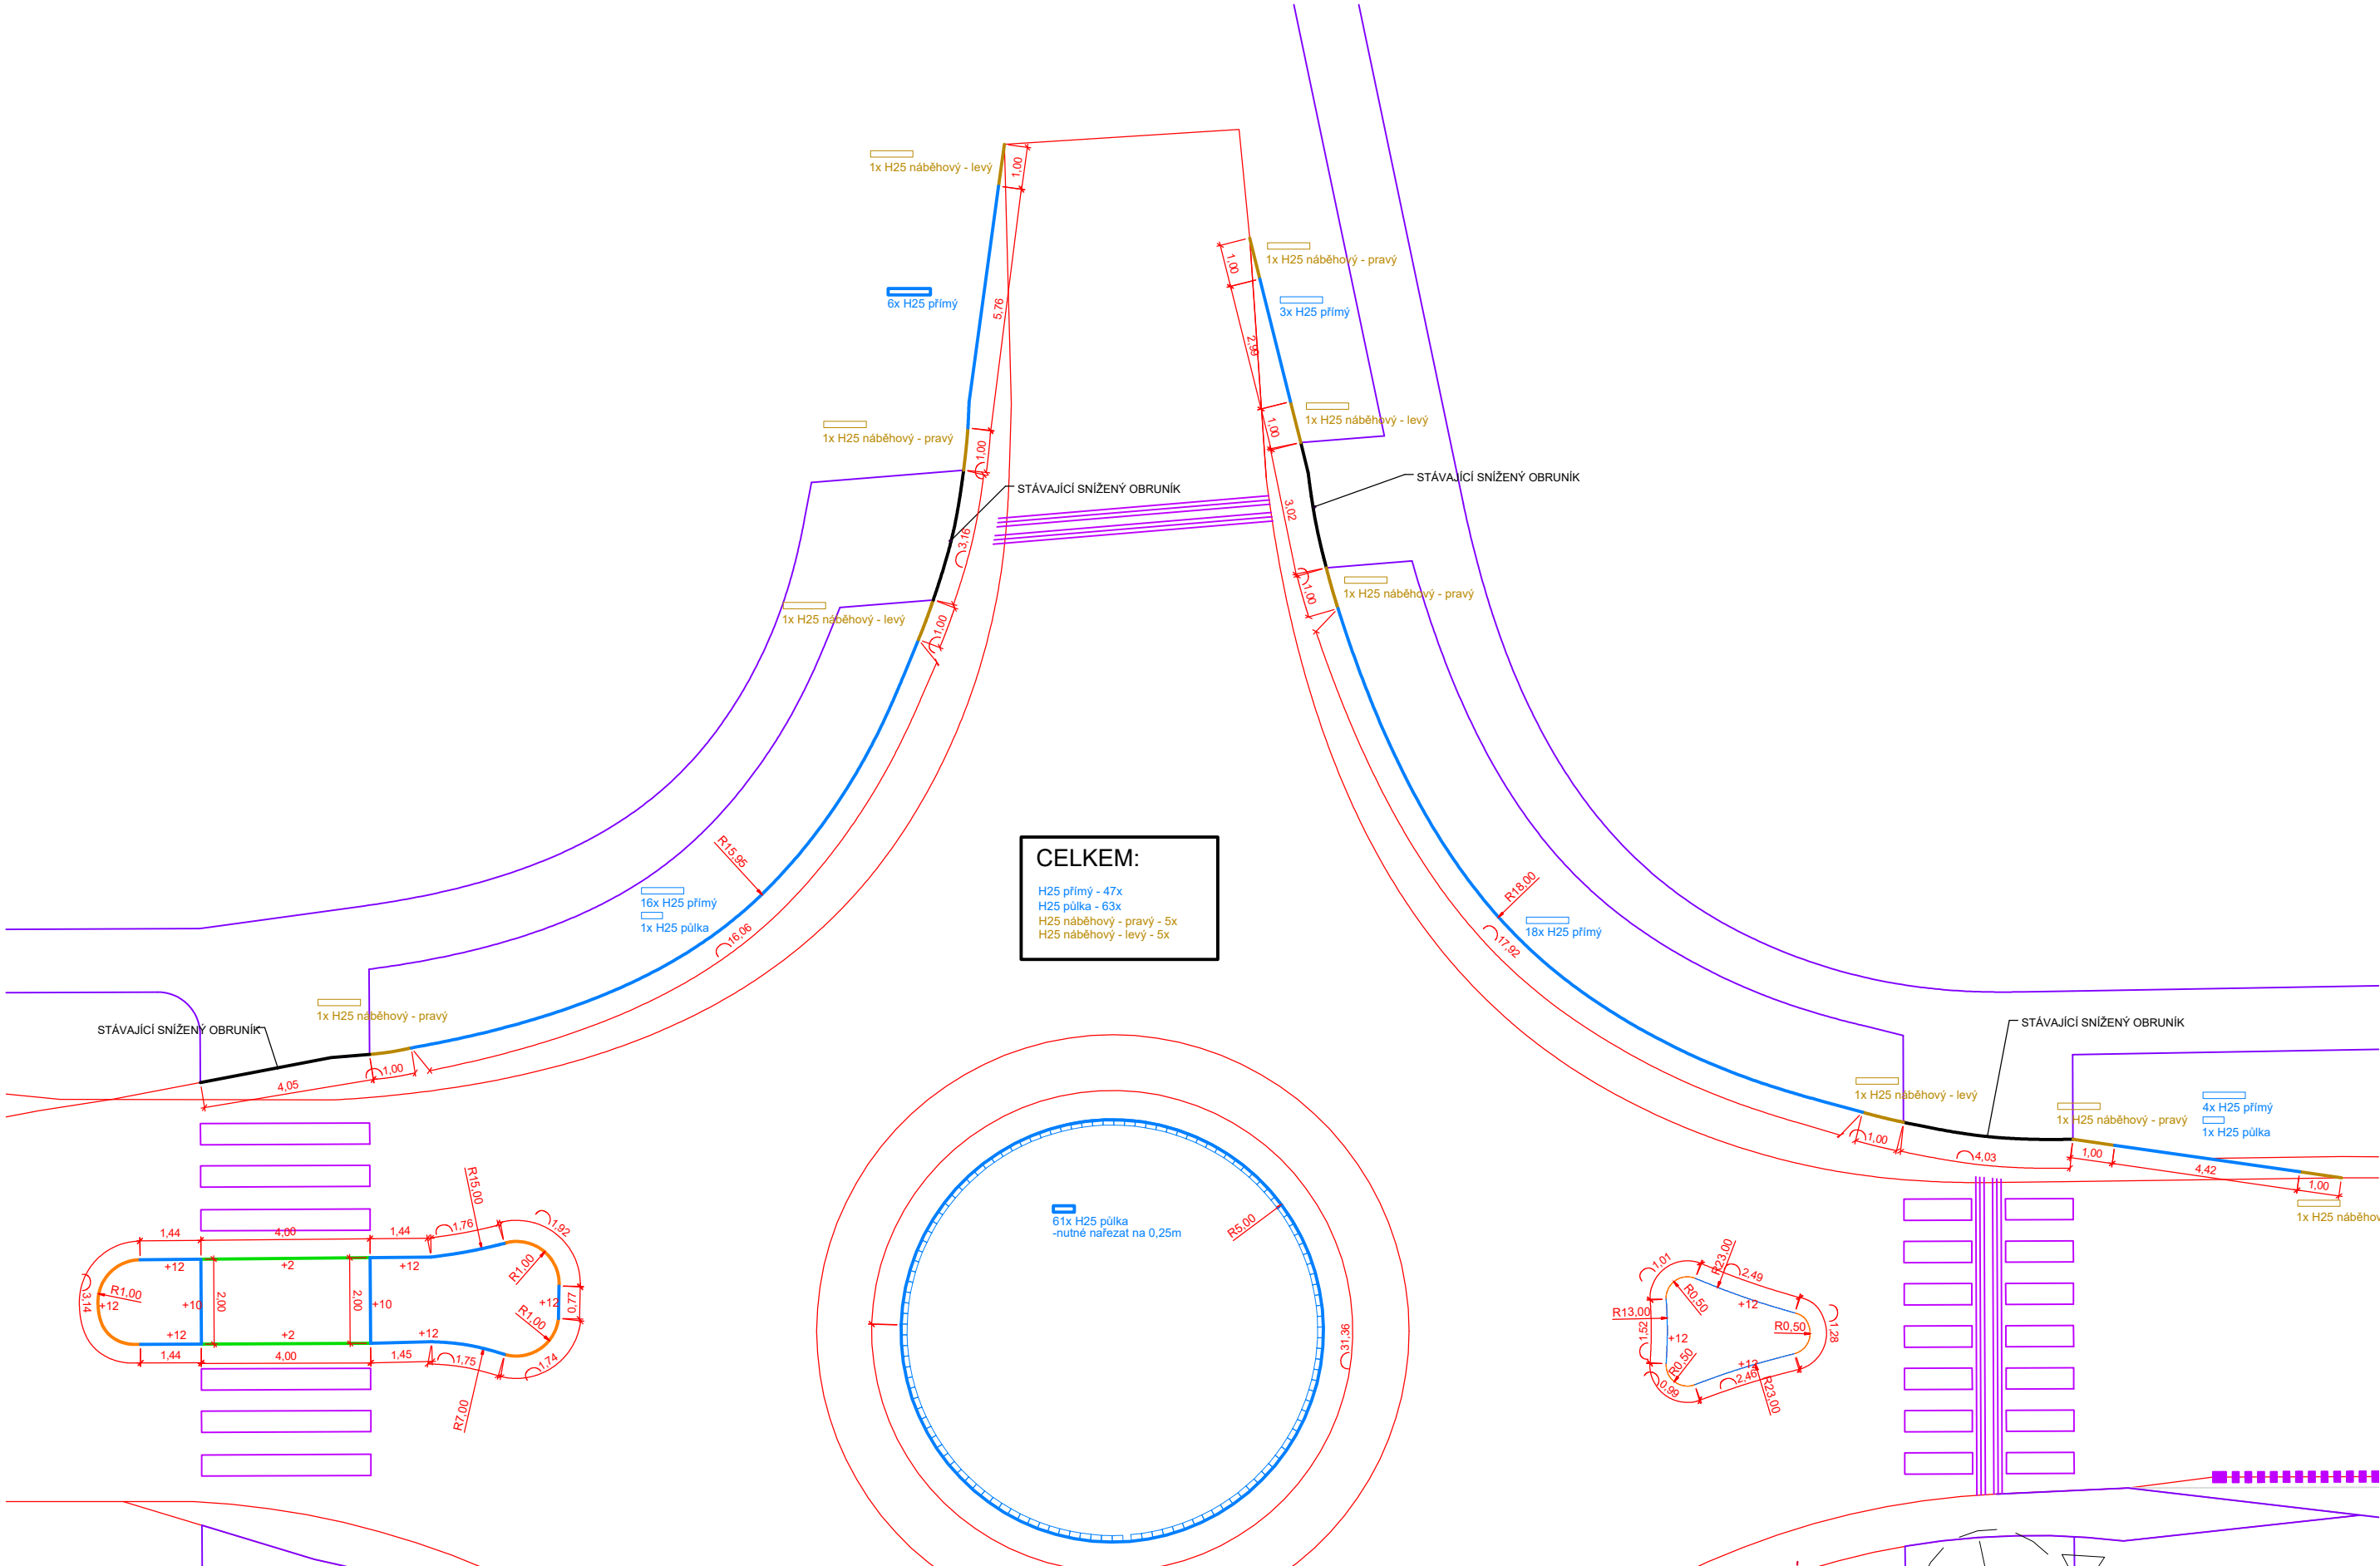

CELKEM:  
H25 přímý - 47x  
H25 půlka - 63x  
H25 náběhový - pravý - 5x  
H25 náběhový - levý - 5x

