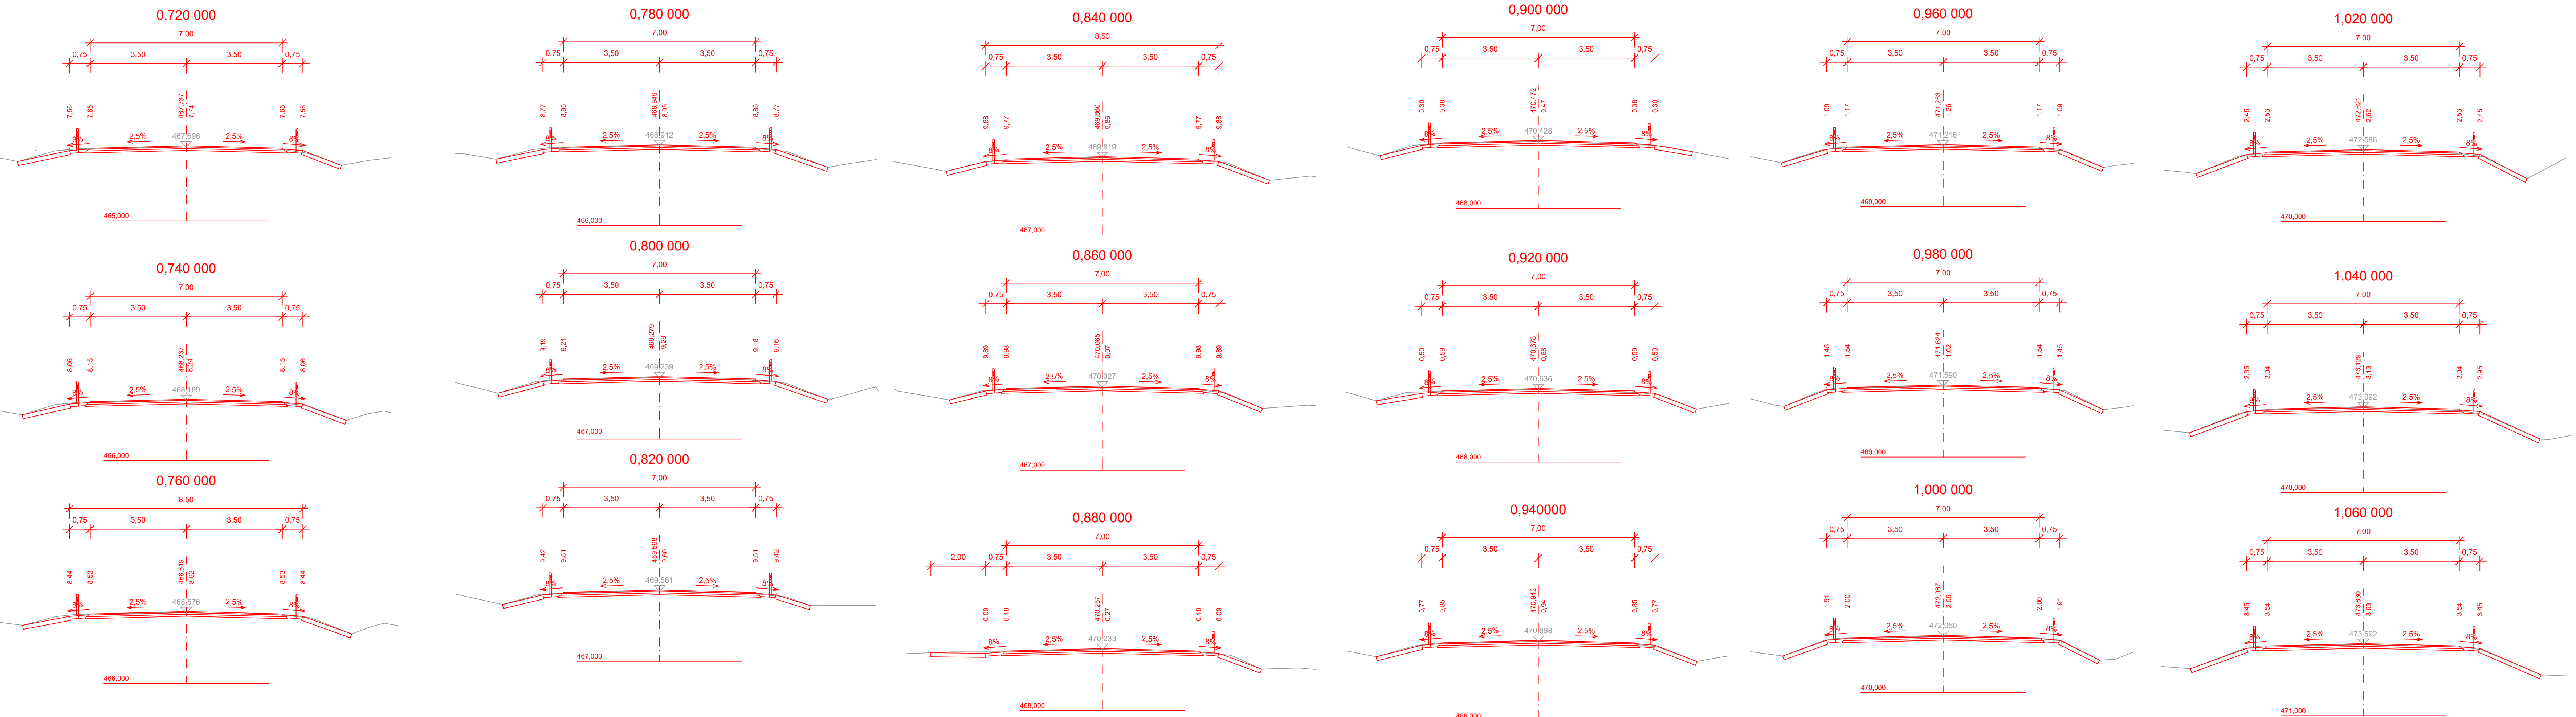


SO 102 - CHARAKTERISTICKÉ ŘEZY
M 1:100



REVIZE:	PŘEDMĚT ZMĚNY:	DATUM:	VYPRACOVAL:
a			
b			
c			

NÁZEV STAVBY: II/603 SULICE - ŽELIVEC, REK. SILNICE A MOSTŮ	ČÍSLO OBJEKTU: SO 102
--	--------------------------

INVESTOR STAVBY č. 1:  KRAJSKÁ SPRÁVA A ÚDRŽBA SILNIC STŘEDOČESKÉHO KRAJE p.o. Zborovská 81/11, 150 21 Praha 5	RAZÍTKO: DATUM: PODPIS:
--	----------------------------

INVESTOR STAVBY č. 2:  OBEC KAMENICE Ringhofferovo náměstí 434 Olešovice, 251 68 Kamenice	RAZÍTKO: DATUM: PODPIS:
---	----------------------------

TECHNICKÝ DOZOR INVESTORA  REALSTAV MB, s.r.o. Klaudiánova 124, 293 01 Mladá Boleslav	RAZÍTKO: KONTROLOVAL: DATUM: PODPIS:
--	--

ZHOTOVITEL STAVBY:  M - SILNICE, a.s. Husova 1697, Bílé Předměstí, 530 03 Pardubice	RAZÍTKO: KONTROLOVAL: DATUM: PODPIS:
--	--

KOORDINÁTOR RDS:  M - PROJEKCE, s.r.o. Resslova 956/13, 500 02 Hradec Králové	RAZÍTKO: KONTROLOVAL: DATUM: PODPIS:
--	--

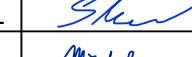
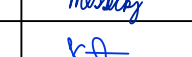
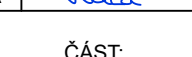
SOUŘADNICOVÝ SYSTÉM: S-JTSK
VÝŠKOVÝ SYSTÉM: B.P.V.

ČISTOPIS

NÁZEV STAVBY: II/603 SULICE - ŽELIVEC, REKONSTRUKCE SILNICE A MOSTŮ
--

ČÁST / STAVEBNÍ OBJEKT: SO 101 - SILNICE II/603 ÚSEK 2 - EXTRAVILÁN
--

PŘÍLOHA: CHARAKTERISTICKÉ PŘÍČNÉ ŘEZY - 1. ČÁST
--

ZHOTOVITEL RDS:  M - PROJEKCE, s.r.o. Resslova 956/13 500 02 Hradec Králové	HLAVNÍ INŽENÝR PROJEKTU: Bc. R. MĚSTECKÝ	PARÉ:    
	ZODPOVĚDNÝ PROJEKTANT: Ing. M. STEJSKAL	
	VYPRACOVAL: Bc. R. MĚSTECKÝ	
	KONTROLA: Ing. P. KELČA	
	MĚŘÍTKO: Č. ZAKÁZKY: STUPĚŇ: DATUM: ČÁST: PŘÍLOHA: 1:100 25-118-03 RDS 06/2026 102 5.1	