


SO 102 - CHARAKTERISTICKÉ ŘEZY
M 1:100

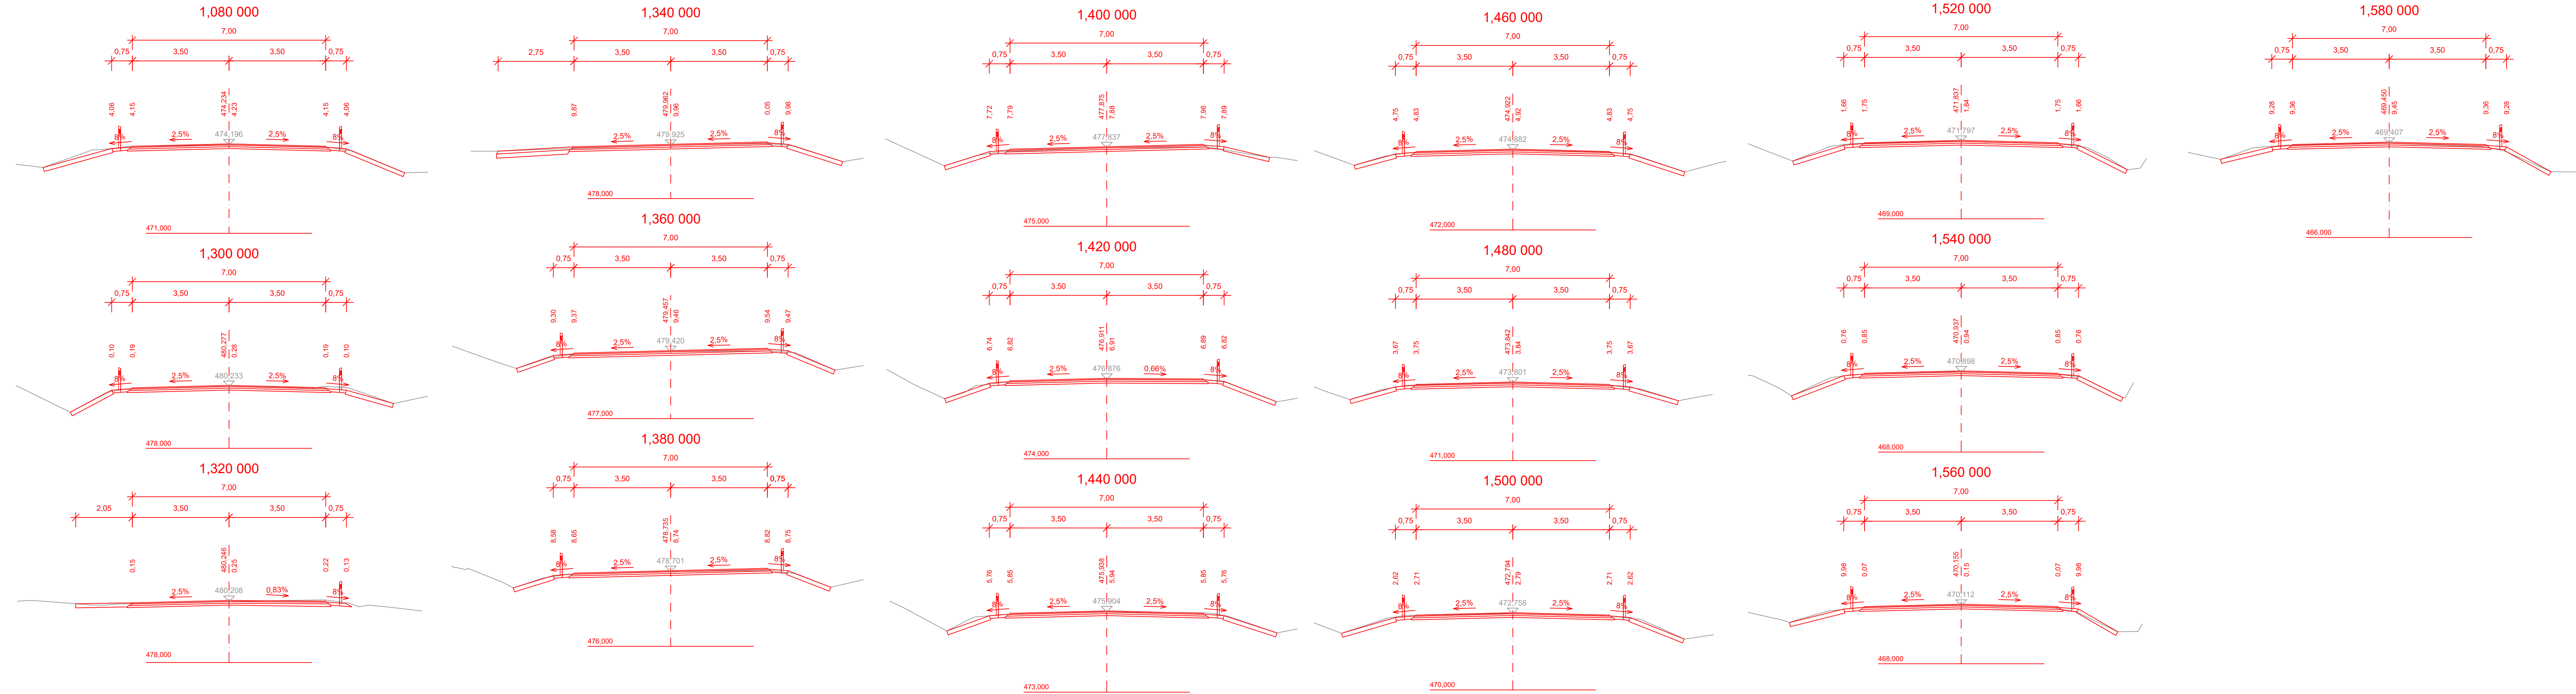

REVIZE:	PŘEDMĚT ZMĚNY:	DATUM:	VYPRACOVAL:
a			
b			
c			

NÁZEV STAVBY: II/603 SULICE - ŽELIVEC, REK. SILNICE A MOSTŮ	ČÍSLO OBJEKTU: SO 102
--	--------------------------

INVESTOR STAVBY č. 1:  KRAJSKÁ SPRÁVA A ÚDRŽBA SILNIC STŘEDOČESKÉHO KRAJE p.o. Zborovská 81/11, 150 21 Praha 5	RAZÍTKO: DATUM: PODPIS:
--	-------------------------------------

INVESTOR STAVBY č. 2:  OBEC KAMENICE Ringhofferovo náměstí 434 Olešovice, 251 68 Kamenice	RAZÍTKO: DATUM: PODPIS:
---	-------------------------------------

TECHNICKÝ DOZOR INVESTORA  REALSTAV MB, spol. s r.o. Klaudiánova 124, 293 01 Mladá Boleslav	RAZÍTKO: KONTOLOVAL: DATUM: PODPIS:
--	--

ZHOTOVITEL STAVBY:  M - SILNICE, a.s. Husova 1697, Bílé Předměstí, 530 03 Pardubice	RAZÍTKO: KONTOLOVAL: DATUM: PODPIS:
--	--

KOORDINÁTOR RDS:  M - PROJEKCE, s.r.o. Resslova 956/13, 500 02 Hradec Králové	RAZÍTKO: KONTOLOVAL: DATUM: PODPIS:
--	--


SOUŘADNICOVÝ SYSTÉM: S-JTSK
VÝŠKOVÝ SYSTÉM: B.P.V.

ČISTOPIS

NÁZEV STAVBY: II/603 SULICE - ŽELIVEC, REKONSTRUKCE SILNICE A MOSTŮ
--

ČÁST / STAVEBNÍ OBJEKT: SO 102 - SILNICE II/603 ÚSEK 2 - EXTRAVILÁN
--

PŘÍLOHA: CHARAKTERISTICKÉ PŘÍČNÉ ŘEZY - 2. ČÁST
--

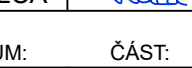ZHOTOVITEL RDS:  M - PROJEKCE, s.r.o. Resslova 956/13 500 02 Hradec Králové	HLAVNÍ INŽENÝR PROJEKTU: Bc. R. MĚSTECKÝ 	PARÉ:
ZODPOVĚDNÝ PROJEKTANT: Ing. M. STEJSKAL 		
VYPRACOVAL: Bc. R. MĚSTECKÝ 		
KONTROLA: Ing. P. KELČA 		
MĚŘÍTKO: 1:100	Č. ZAKÁZKY: 25-118-03	STUPĚŇ: RDS
DATUM: 06/2026	ČÁST: 102	PŘÍLOHA: 5.2