



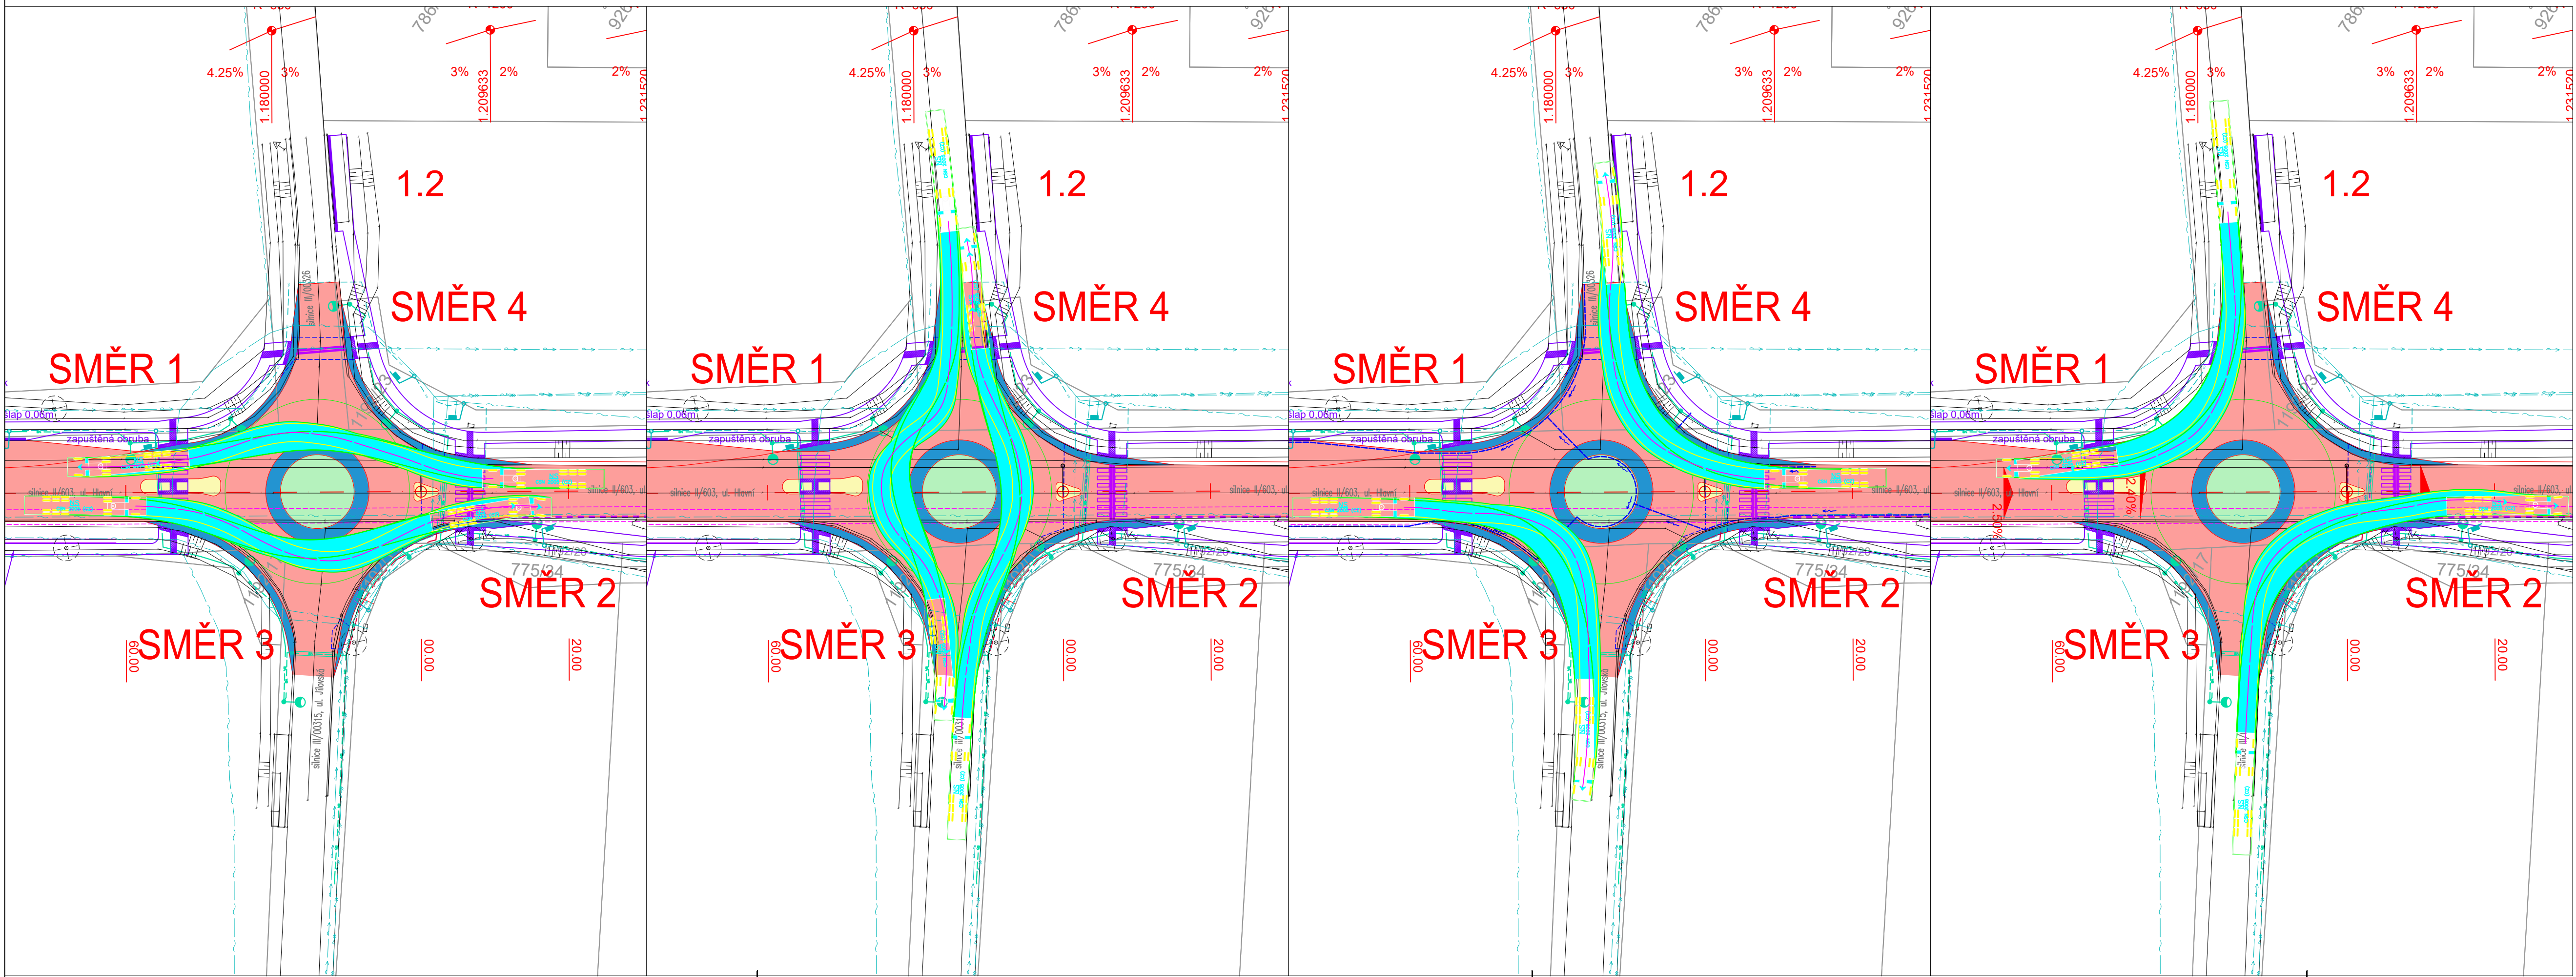

Směrové návaznosti

	Směr
1	Hlubočinka
2	Želivec
3	Sulice
4	Křížový Újezdec

Vozidlo NS

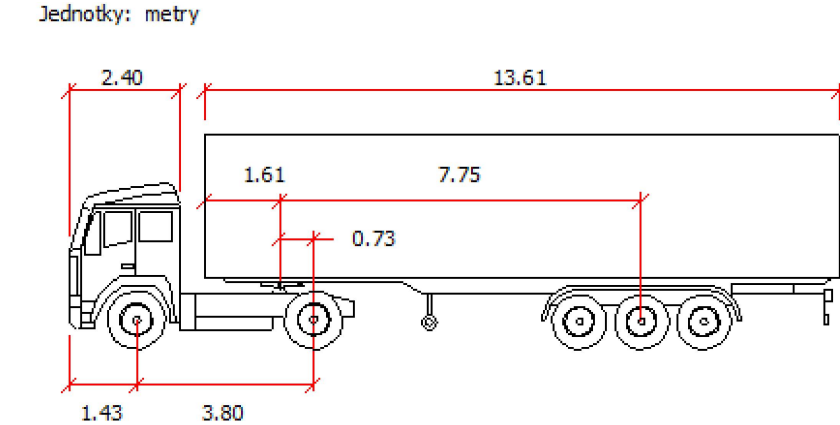

Simulovaná rychlost

Trasa	Rychlost
1->2	20 km/h
2->1	20 km/h
3->4	20 km/h
4->3	10 km/h
1->3	20 km/h
2->4	20 km/h
4->1	20 km/h
3->2	20 km/h

SEZNAM STAVEBNÍCH OBJEKTŮ:

100 - OBJEKTY POZEMNÍCH KOMUNIKACÍ

SO 101 - SILNICE II/603 ÚSEK 1 - INTRAVILÁN
SO 101.1 - SILNICE II/603 ÚSEK 1 - INTRAVILÁN CHODNÍK 2,721-2,797
SO 101.2 - OZELENĚNÍ NEZPEVNĚNÉ PLOCHY ULICE RINGHOFFEROVA
SO 101.3 - SILNICE II/603 ÚSEK 1 - INTRAVILÁN - OPRAVA POVRCHU
SO 101.4 - SILNICE II/603 ÚSEK 1 - KOMPLEXNÍ OPRAVA 2,471-2,509
SO 102 - SILNICE II/603 ÚSEK 2 - EXTRAVILÁN
SO 103 - SILNICE II/603 ÚSEK 3 - OKRUŽNÍ KŘÍŽOVATKA
SO 104 - SILNICE II/603 ÚSEK 4 - PROPUSTEK 1
SO 105 - SILNICE II/603 ÚSEK 5 - PROPUSTEK 2
SO 106 - SILNICE II/603 ÚSEK 6 - NOVÁ HOSPODA
SO 107 - SILNICE II/603 ÚSEK 7 - ZPOMALOVACÍ OSTRŮVEK
SO 161 - DOPRAVNÍ INŽENÝRSKÉ OPATŘENÍ (NENÍ ZOBRAZENO)

300 - VODOHOSPODÁRSKÉ OBJEKTY

SO 331 - OCHRANA / ÚPRAVA KANALIZACE V ÚSEKU 1
SO 334 - OCHRANA / ÚPRAVA KANALIZACE V ÚSEKU 4
SO 335 - OCHRANA / ÚPRAVA KANALIZACE V ÚSEKU 5
SO 336 - OCHRANA / ÚPRAVA KANALIZACE V ÚSEKU 6
SO 337 - OCHRANA / ÚPRAVA KANALIZACE V ÚSEKU 7
SO 341 - OCHRANA / ÚPRAVA VODOVODŮ V ÚSEKU 1
SO 343 - OCHRANA / ÚPRAVA VODOVODŮ V ÚSEKU 3
SO 344 - OCHRANA / ÚPRAVA VODOVODŮ V ÚSEKU 4
SO 345 - OCHRANA / ÚPRAVA VODOVODŮ V ÚSEKU 5
SO 346 - OCHRANA / ÚPRAVA VODOVODŮ V ÚSEKU 6

LEGENDA:

ČÁRY A HRANY

HRANY KOMUNIKACE
OSA KOMUNIKACE
SOUVISEJÍCÍ STAVBA
ZAMĚŘENÍ STÁVAJÍCÍHO STAVU
KATASTRÁLNÍ MAPA
DRENÁŽ

PLOCHY

PLOCHA KOMUNIKACE - SKLADBA 1 (INTRAVILÁN)
PLOCHA KOMUNIKACE - SKLADBA 2 (EXTRAVILÁN)
PLOCHA KOMUNIKACE - SKLADBA 3 (OPRAVA OBRUSU)
PLOCHA KOMUNIKACE - SKLADBA 4 (POJÍZDNÁ DLAŽBA OK)
PLOCHA KOMUNIKACE - SKLADBA 5 (NEPOJÍZDNÁ DLAŽBA CHODNÍKY)
PLOCHA KOMUNIKACE - SKLADBA 6 (POJÍZDNÁ DLAŽBA)
OBNOVA NÁPOJENÍ SJEZDŮ (ŠTERK)
OBNOVA NÁPOJENÍ SJEZDŮ (DLAŽBA POJÍZDNÁ)
OBNOVA NÁPOJENÍ SJEZDŮ (ASFALT)
NEZPEVNĚNÁ KRAJNICE
ZPEVNĚNÍ POVRCHU S ODVODŇOVACÍ FUNKCÍ
OZELENĚNÍ, NEZPEVNĚNÁ PLOCHA, TERÉNNÍ ÚPRAVY

400 - ELEKTRO A SDĚLOVACÍ OBJEKTY

SO 413 - PŘELOŽKA VEDENÍ VN V ÚSEKU 3
SO 414 - OCHRANA / ÚPRAVA VEDENÍ VN V VN V ÚSEKU 4
SO 432 - OCHRANA / ÚPRAVA KABELŮ NN A VN V ÚSEKU 1 A 2
SO 434 - OCHRANA / ÚPRAVA VEDENÍ NN V ÚSEKU 4
SO 435 - OCHRANA / ÚPRAVA VEDENÍ NN V ÚSEKU 5
SO 437 - OCHRANA / ÚPRAVA VEDENÍ NN V ÚSEKU 7
SO 441 - DOPLNĚNÍ A ÚPRAVA VO V ÚSEKU 1, KM 2,756
SO 443 - DOPLNĚNÍ A ÚPRAVA VO V ÚSEKU 3 - OK
SO 444 - OCHRANA / ÚPRAVA KABELŮ VO V ÚSEKU 4
SO 445 - OCHRANA / ÚPRAVA KABELŮ VO V ÚSEKU 5
SO 446 - OCHRANA / ÚPRAVA KABELŮ VO V ÚSEKU 6
SO 447 - DOPLNĚNÍ A ÚPRAVA VO V ÚSEKU 7 - ZPOMALOVACÍ OSTRŮVEK
SO 452 - OCHRANA / ÚPRAVA SDĚLOVACÍCH KABELŮ V ÚSEKU 1 A 2
SO 453 - OCHRANA / ÚPRAVA SDĚLOVACÍCH KABELŮ V ÚSEKU 3
SO 454 - OCHRANA / ÚPRAVA SDĚLOVACÍCH KABELŮ V ÚSEKU 4
SO 455 - OCHRANA / ÚPRAVA SDĚLOVACÍCH KABELŮ V ÚSEKU 5
SO 457 - OCHRANA / ÚPRAVA SDĚLOVACÍCH KABELŮ V ÚSEKU 7

500 - OBJEKTY TRUBNÍCH VEDENÍ

SO 515 - OCHRANA / ÚPRAVA VLT PLYNOVODŮ V ÚSEKU 5
SO 521 - OCHRANA / ÚPRAVA STL PLYNOVODŮ V ÚSEKU 1
SO 524 - OCHRANA / ÚPRAVA STL PLYNOVODŮ V ÚSEKU 4
SO 525 - OCHRANA / ÚPRAVA STL PLYNOVODŮ V ÚSEKU 5
SO 526 - OCHRANA / ÚPRAVA STL PLYNOVODŮ V ÚSEKU 6
SO 527 - OCHRANA / ÚPRAVA STL PLYNOVODŮ V ÚSEKU 7

LEGENDA INŽENÝRSKÝCH SÍTÍ:

STÁVAJÍCÍ

VODOVOD, PŘÍPOJKY
PODZEMNÍ VEDENÍ NN
SOUVISEJÍCÍ STAVBA
PODZEMNÍ VEDENÍ VN
NADZEMNÍ VEDENÍ VN
SDĚLOVACÍ VEDENÍ - BEZ ROZLIŠENÍ
VEREJNÉ OSVĚTLENÍ
PLYNOVÉ STL
PLYNOVÉ VTL
KANALIZACE - BEZ ROZLIŠENÍ

POZN. POLOHA INŽ. SÍTÍ JE POUZE ORIENTAČNÍ. PŘED
PROVÁDĚNÍM STAVEBNÍCH PRACÍ JE NEZBYTNÉ PROVĚST
VYTÝČENÍ VEŠKERÝCH INŽENÝRSKÝCH SÍTÍ.

REVIZE:	PŘEDMĚT ZMĚNY:	DATUM:	VYPRACOVAL:
a			
b			
c			

NÁZEV STAVBY:	ČÍSLO OBJEKTU:
II/603 SULICE - ŽELIVEC, REK. SILNICE A MOSTŮ	SO 103

INVESTOR STAVBY č.1:	KRAJSKÁ SPRÁVA A ÚDRŽBA SILNIC STŘEDOČESKÉHO KRAJE p.o. Zborovská 81/11, 150 21 Praha 5	RAZÍTKO:
		DATUM: PODPIS:

INVESTOR STAVBY č.2:	OBEC KAMENICE Ringhofferovo náměstí 434 Olešovice, 251 68 Kamenice	RAZÍTKO:
		DATUM: PODPIS:

TECHNICKÝ DOZOR INVESTORA	REALSTAV MB, s.r.o. Klaudánova 124, 293 01 Mladá Boleslav	RAZÍTKO:
		KONTROLOVAL: DATUM: PODPIS:

ZHOTOVITEL STAVBY:	M - SILNICE, a.s. Husova 1697, Bílé Předměstí, 530 03 Pardubice	RAZÍTKO:
		KONTROLOVAL: DATUM: PODPIS:

KOORDINÁTOR RDS:	M - PROJEKCE, s.r.o. Resslova 956/13, 500 02 Hradec Králové	RAZÍTKO:
		KONTROLOVAL: DATUM: PODPIS:

SOUŘADNICOVÝ SYSTÉM: S-JTSK
VÝŠKOVÝ SYSTÉM: B.P.V.

ČISTOPIS

NÁZEV STAVBY:	II/603 SULICE - ŽELIVEC, REKONSTRUKCE SILNICE A MOSTŮ				
ČÁST / STAVEBNÍ OBJEKT:	SO 103 - SILNICE II/603 ÚSEK 3 - OKRUŽNÍ KŘÍŽOVATKA				
PŘÍLOHA:	VLEČNÉ KŘIVKY				
ZHOTOVITEL RDS:	HLAVNÍ INŽENÝR PROJEKTU:	Bc. R. MĚSTECKÝ		PARÉ:	
	ZODPOVĚDNÝ PROJEKTANT:	Ing. M. STEJSKAL			
M - PROJEKCE, s.r.o. Resslova 956/13 500 02 Hradec Králové	VYPRACOVAL:	Ing. M. ŠPRONGL			
	KONTROLA:	Ing. P. KELČA			
	MĚŘÍTKO:	Č. ZAKÁZKY:	STUPEŇ:	DATUM:	ČÁST:
	1:500	25-118-03	RDS	06/2026	103
					8