


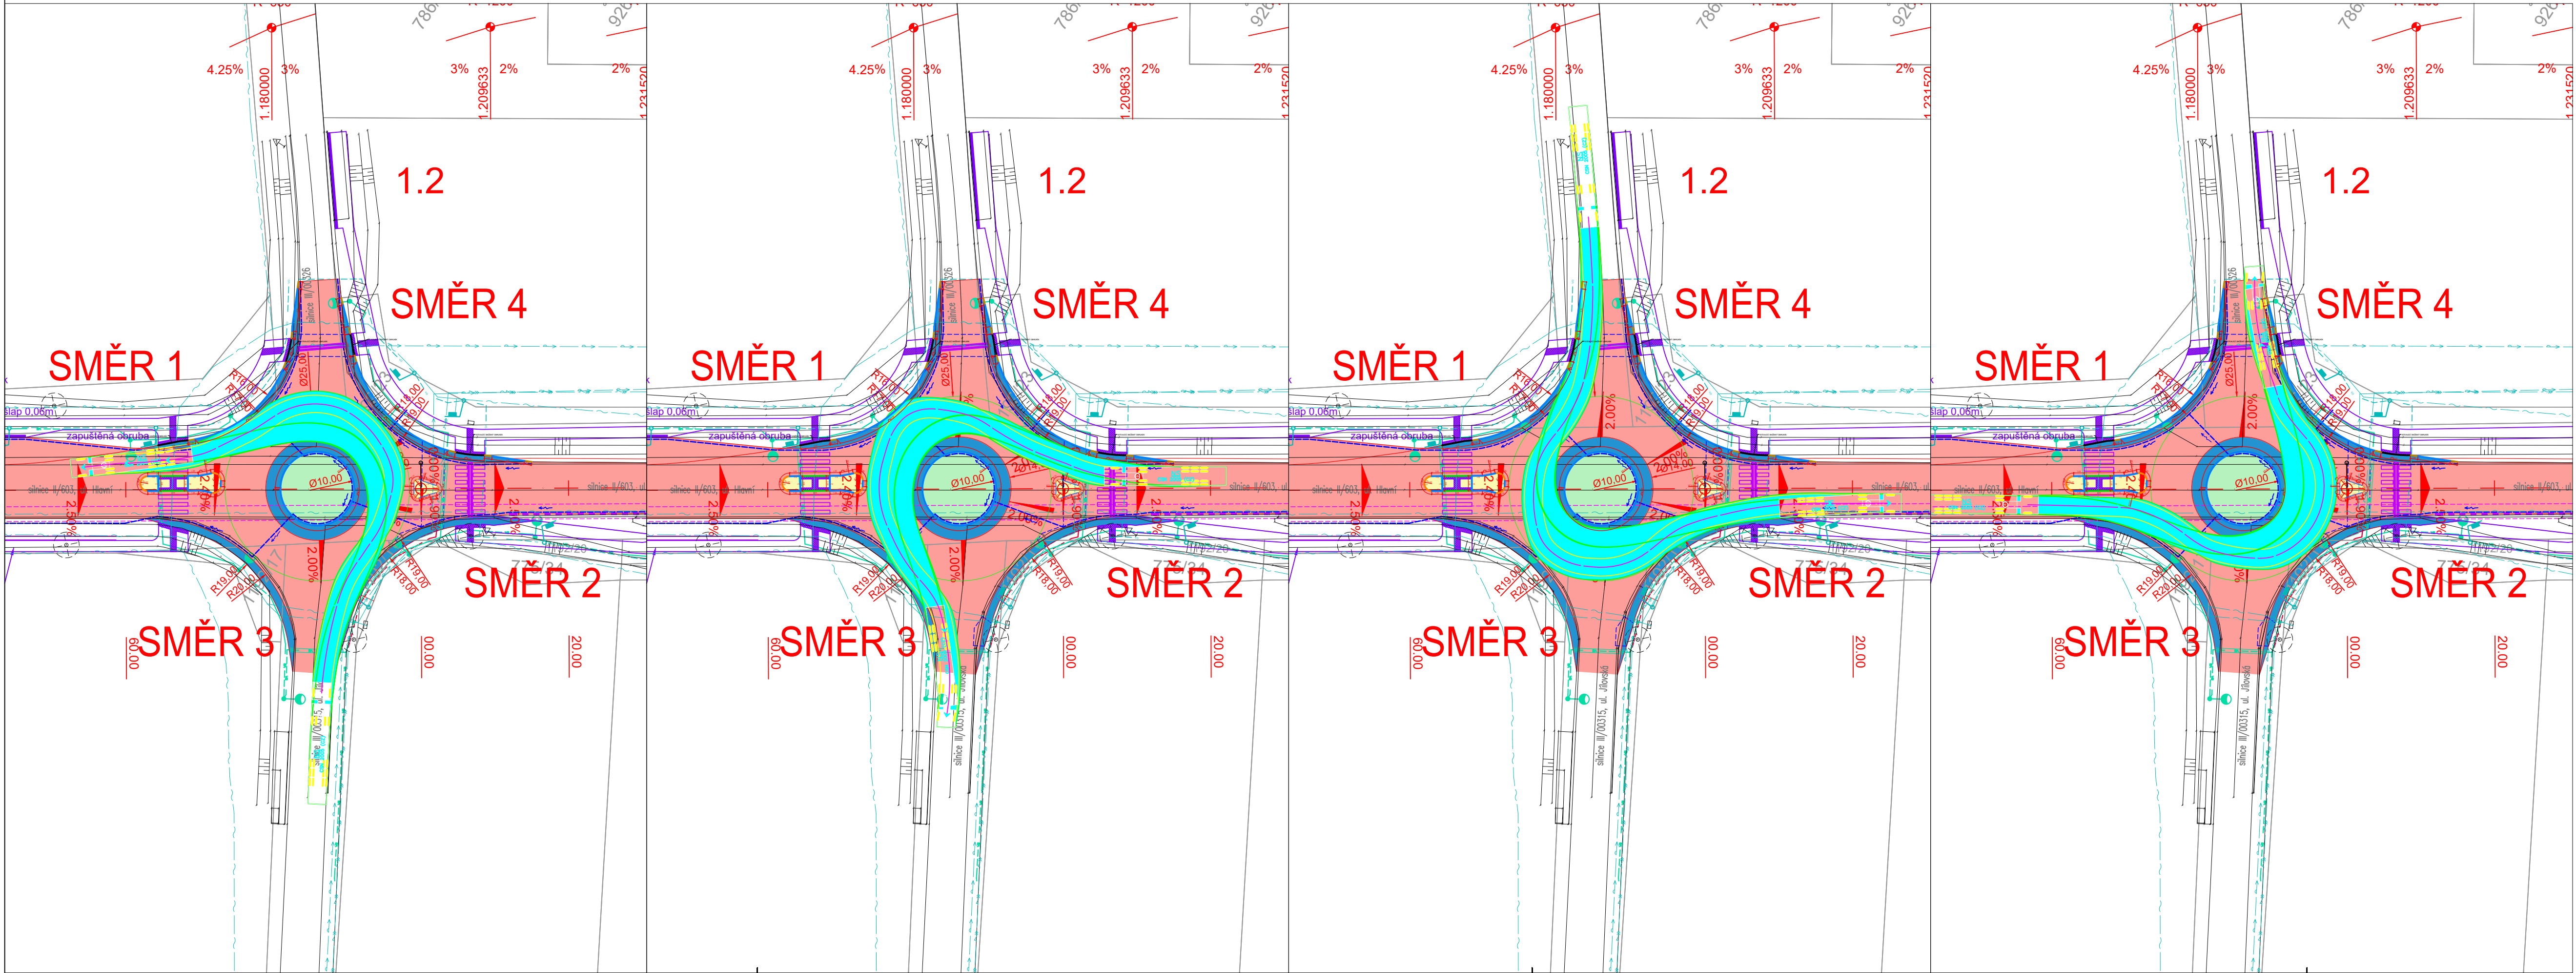


Směrové návaznosti

	Směr
1	Hlubočinka
2	Želivec
3	Sulice
4	Křížový Újezdec

Vozidlo NS

Jednotky: metry

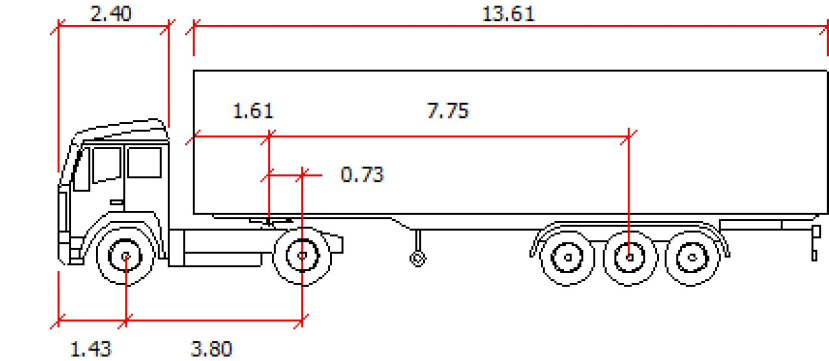

Simulovaná rychlost

Trasa	Rychlost
3 -> 1	10 km/h
2 -> 3	10 km/h
4 -> 2	10 km/h
1 -> 4	10 km/h

SEZNAM STAVEBNÍCH OBJEKTŮ:

100 - OBJEKTY POZEMNÍCH KOMUNIKACÍ

SO 101 - SILNICE II/603 ÚSEK 1 - INTRAVILÁN
SO 101.1 - SILNICE II/603 ÚSEK 1 - INTRAVILÁN CHODNÍK 2,721-2,797
SO 101.2 - OZELENÍ NEZPEVNĚNÉ PLOCHY ULICE RINGHOFFEROVA
SO 101.3 - SILNICE II/603 ÚSEK 1 - INTRAVILÁN - OPRAVA POVRCHU
SO 101.4 - SILNICE II/603 ÚSEK 1 - KOMPLEXNÍ OPRAVA 2,471-2,509
SO 102 - SILNICE II/603 ÚSEK 2 - EXTRAVILÁN
SO 103 - SILNICE II/603 ÚSEK 3 - OKRUŽNÍ KŘÍŽOVATKA
SO 104 - SILNICE II/603 ÚSEK 4 - PROPUSTEK 1
SO 105 - SILNICE II/603 ÚSEK 5 - PROPUSTEK 2
SO 106 - SILNICE II/603 ÚSEK 6 - NOVÁ HOSPODA
SO 107 - SILNICE II/603 ÚSEK 7 - ZPOMALOVACÍ OSTRŮVEK
SO 161 - DOPRAVNÍ INŽENÝRSKÉ OPATŘENÍ (NENÍ ZOBRAZENO)

300 - VODOHOSPODÁRSKÉ OBJEKTY

SO 331 - OCHRANA / ÚPRAVA KANALIZACE V ÚSEKU 1
SO 334 - OCHRANA / ÚPRAVA KANALIZACE V ÚSEKU 4
SO 335 - OCHRANA / ÚPRAVA KANALIZACE V ÚSEKU 5
SO 335.1 - OCHRANA / ÚPRAVA DEŠŤOVÉ KANALIZACE V ÚSEKU 5
SO 336 - OCHRANA / ÚPRAVA KANALIZACE V ÚSEKU 6
SO 337 - OCHRANA / ÚPRAVA KANALIZACE V ÚSEKU 7
SO 341 - OCHRANA / ÚPRAVA VODOVODŮ V ÚSEKU 1
SO 343 - OCHRANA / ÚPRAVA VODOVODŮ V ÚSEKU 3
SO 344 - OCHRANA / ÚPRAVA VODOVODŮ V ÚSEKU 4
SO 345 - OCHRANA / ÚPRAVA VODOVODŮ V ÚSEKU 5
SO 346 - OCHRANA / ÚPRAVA VODOVODŮ V ÚSEKU 6

LEGENDA:

ČÁRY A HRANY

— HRANY KOMUNIKACE
— OSA KOMUNIKACE
— SOUVISEJÍCÍ STAVBA
— ZAMĚŘENÍ STÁVAJÍCÍHO STAVU
— KATASTRÁLNÍ MAPA
— DRENÁŽ

PLOCHY

PLOCHA KOMUNIKACE - SKLADBA 1 (INTRAVILÁN)
PLOCHA KOMUNIKACE - SKLADBA 2 (EXTRAVILÁN)
PLOCHA KOMUNIKACE - SKLADBA 3 (OPRAVA OBRUSU)
PLOCHA KOMUNIKACE - SKLADBA 4 (POJÍZDNÁ DLAŽBA OK)
PLOCHA KOMUNIKACE - SKLADBA 5 (NEPOJÍZDNÁ DLAŽBA CHODNÍKY)
PLOCHA KOMUNIKACE - SKLADBA 6 (POJÍZDNÁ DLAŽBA)
OBNOVA NÁPOJENÍ SJEZDŮ (ŠTĚRK)
OBNOVA NÁPOJENÍ SJEZDŮ (DLAŽBA POJÍZDNÁ)
OBNOVA NÁPOJENÍ SJEZDŮ (ASFALT)
NEZPEVNĚNÁ KRAJNICE
ZPEVNĚNÍ POVRCHU S ODVODŇOVACÍ FUNKCÍ
OZELENÍ, NEZPEVNĚNÁ PLOCHA, TERÉNNÍ ÚPRAVY

400 - ELEKTRO A SDĚLOVACÍ OBJEKTY

SO 413 - PŘELOŽKA VEDENÍ VN V ÚSEKU 3
SO 414 - OCHRANA / ÚPRAVA VEDENÍ VN V ÚSEKU 4
SO 432 - OCHRANA / ÚPRAVA KABELŮ NN A VN V ÚSEKU 1 A 2
SO 434 - OCHRANA / ÚPRAVA VEDENÍ NN V ÚSEKU 4
SO 435 - OCHRANA / ÚPRAVA VEDENÍ NN V ÚSEKU 5
SO 437 - OCHRANA / ÚPRAVA VEDENÍ NN V ÚSEKU 7
SO 441 - DOPLNĚNÍ A ÚPRAVA VO V ÚSEKU 1, KM 2,756
SO 443 - DOPLNĚNÍ A ÚPRAVA VO V ÚSEKU 3 - OK
SO 444 - OCHRANA / ÚPRAVA KABELŮ VO V ÚSEKU 4
SO 445 - OCHRANA / ÚPRAVA KABELŮ VO V ÚSEKU 5
SO 446 - OCHRANA / ÚPRAVA KABELŮ VO V ÚSEKU 6
SO 447 - DOPLNĚNÍ A ÚPRAVA VO V ÚSEKU 7 - ZPOMALOVACÍ OSTRŮVEK
SO 452 - OCHRANA / ÚPRAVA SDĚLOVACÍCH KABELŮ V ÚSEKU 1 A 2
SO 453 - OCHRANA / ÚPRAVA SDĚLOVACÍCH KABELŮ V ÚSEKU 3
SO 454 - OCHRANA / ÚPRAVA SDĚLOVACÍCH KABELŮ V ÚSEKU 4
SO 455 - OCHRANA / ÚPRAVA SDĚLOVACÍCH KABELŮ V ÚSEKU 5
SO 457 - OCHRANA / ÚPRAVA SDĚLOVACÍCH KABELŮ V ÚSEKU 7

500 - OBJEKTY TRUBNÍCH VEDENÍ

SO 515 - OCHRANA / ÚPRAVA VLT PLYNOVODŮ V ÚSEKU 5
SO 521 - OCHRANA / ÚPRAVA STL PLYNOVODŮ V ÚSEKU 1
SO 524 - OCHRANA / ÚPRAVA STL PLYNOVODŮ V ÚSEKU 7
SO 525 - OCHRANA / ÚPRAVA STL PLYNOVODŮ V ÚSEKU 4
SO 526 - OCHRANA / ÚPRAVA STL PLYNOVODŮ V ÚSEKU 6
SO 527 - OCHRANA / ÚPRAVA STL PLYNOVODŮ V ÚSEKU 7

LEGENDA INŽENÝRSKÝCH SÍTÍ:

STÁVAJÍCÍ

— VODOVOD, PŘÍPOJKY
— PODZEMNÍ VEDENÍ NN
— NADZEMNÍ VEDENÍ NN
— PODZEMNÍ VEDENÍ VN
— NADZEMNÍ VEDENÍ VN
— SDĚLOVACÍ VEDENÍ - BEZ ROZLIŠENÍ
— VEREJNÉ OSVĚTLENÍ
— PLYNOVÉ STL
— PLYNOVÉ VTL
— KANALIZACE - BEZ ROZLIŠENÍ

POZN. POLOHA INŽ. SÍTÍ JE POUZE ORIENTAČNÍ. PŘED PROVEDENÍM STAVEBNÍCH PRACÍ JE NEZBYTNÉ PROVĚST VYTÝČENÍ VEŠKERÝCH INŽENÝRSKÝCH SÍTÍ.

REVIZE:	PŘEDMĚT ZMĚNY:	DATUM:	VYPRACOVAL:
a			
b			
c			

NÁZEV STAVBY:	ČÍSLO OBJEKTU:
II/603 SULICE - ŽELIVEC, REK. SILNICE A MOSTŮ	SO 103

INVESTOR STAVBY č.1:	RAZÍTKO:
DATUM:	PODPIS:

INVESTOR STAVBY č.2:	RAZÍTKO:
DATUM:	PODPIS:

TECHNICKÝ DOZOR INVESTORA	RAZÍTKO:
KONTROLOVAL:	DATUM:

ZHOTOVITEL STAVBY:	RAZÍTKO:
KONTROLOVAL:	DATUM:

KOORDINÁTOR RDS:	RAZÍTKO:
KONTROLOVAL:	DATUM:

SOUŘADNICOVÝ SYSTÉM: S-JTSK	VÝŠKOVÝ SYSTÉM: B.P.V.	ČISTOPIS
-----------------------------	------------------------	----------

NÁZEV STAVBY:	II/603 SULICE - ŽELIVEC, REKONSTRUKCE SILNICE A MOSTŮ				
ČÁST / STAVEBNÍ OBJEKT:	SO 103 - SILNICE II/603 ÚSEK 3 - OKRUŽNÍ KŘÍŽOVATKA				
PŘÍLOHA:	VLEČNÉ KŘIVKY				
ZHOTOVITEL RDS:	HLAVNÍ INŽENÝR PROJEKTU:	Bc. R. MĚSTECKÝ		PARÉ:	
	ZODPOVĚDNÝ PROJEKTANT:	Ing. M. STEJSKAL			
	VYPRACOVAL:	Ing. M. ŠPRONGL			
	KONTROLA:	Ing. P. KELČA			
MĚŘÍTKO:	Č. ZAKÁZKY:	STUPEŇ:	DATUM:	ČÁST:	PŘÍLOHA:
1:500	25-118-03	RDS	06/2026	103	8.2