

REVIZE:	PŘEDMĚT ZMĚNY:	DATUM:	VYPRACOVAL:
a			
b			
c			

NÁZEV STAVBY: II/603 SULICE - ŽELIVEC, REK. SILNICE A MOSTŮ	ČÍSLO OBJEKTU: SO 103
---	---------------------------------

INVESTOR STAVBY č.1:  KRAJSKÁ SPRÁVA A ÚDRŽBA SILNIC STŘEDOČESKÉHO KRAJE p.o. Zborovská 81/11, 150 21 Praha 5	RAZÍTKO: DATUM: PODPIS:
--	---

INVESTOR STAVBY č.2:  OBEC KAMENICE Ringhofferovo náměstí 434 Olešovice, 251 68 Kamenice	RAZÍTKO: DATUM: PODPIS:
--	---

TECHNICKÝ DOZOR INVESTORA  REALSTAV MB, s.r.o. Klaudiánova 124, 293 01 Mladá Boleslav	RAZÍTKO: KONTROLOVAL: DATUM: PODPIS:
--	---

ZHOTOVITEL STAVBY:  M - SILNICE, a.s. Husova 1697, Bílé Předměstí, 530 03 Pardubice	RAZÍTKO: KONTROLOVAL: DATUM: PODPIS:
--	---

KOORDINÁTOR RDS:  M - PROJEKCE, s.r.o. Resslova 956/13, 500 02 Hradec Králové	RAZÍTKO: KONTROLOVAL: DATUM: PODPIS:
--	---

SOUŘADNICOVÝ SYSTÉM: S-JTSK

VÝŠKOVÝ SYSTÉM: B.P.V.

ČISTOPIS


NÁZEV STAVBY: II/603 SULICE - ŽELIVEC, REKONSTRUKCE SILNICE A MOSTŮ

ČÁST / STAVEBNÍ OBJEKT: SO 103 - SILNICE II/603 ÚSEK 3 - OKRUŽNÍ KŘÍŽOVATKA

PŘÍLOHA: VYTYČOVACÍ BODY

ZHOTOVITEL RDS:  M - PROJEKCE, s.r.o. Resslova 956/13 500 02 Hradec Králové	HLAVNÍ INŽENÝR PROJEKTU: Bc. R. MĚSTECKÝ					PARÉ:	
	ZODPOVĚDNÝ PROJEKTANT: Ing. M. STEJSKAL						
	VYPRACOVAL: Bc. R. MĚSTECKÝ						
	KONTROLA: Ing. P. KELČA						
	MĚŘÍTKO: Č. ZAKÁZKY: STUPEŇ: DATUM: ČÁST: PŘÍLOHA:						
-		25-118-03		RDS	06/2026	103	11

SCHÉMA VYTYČOVANÝCH BODŮ M 1:50

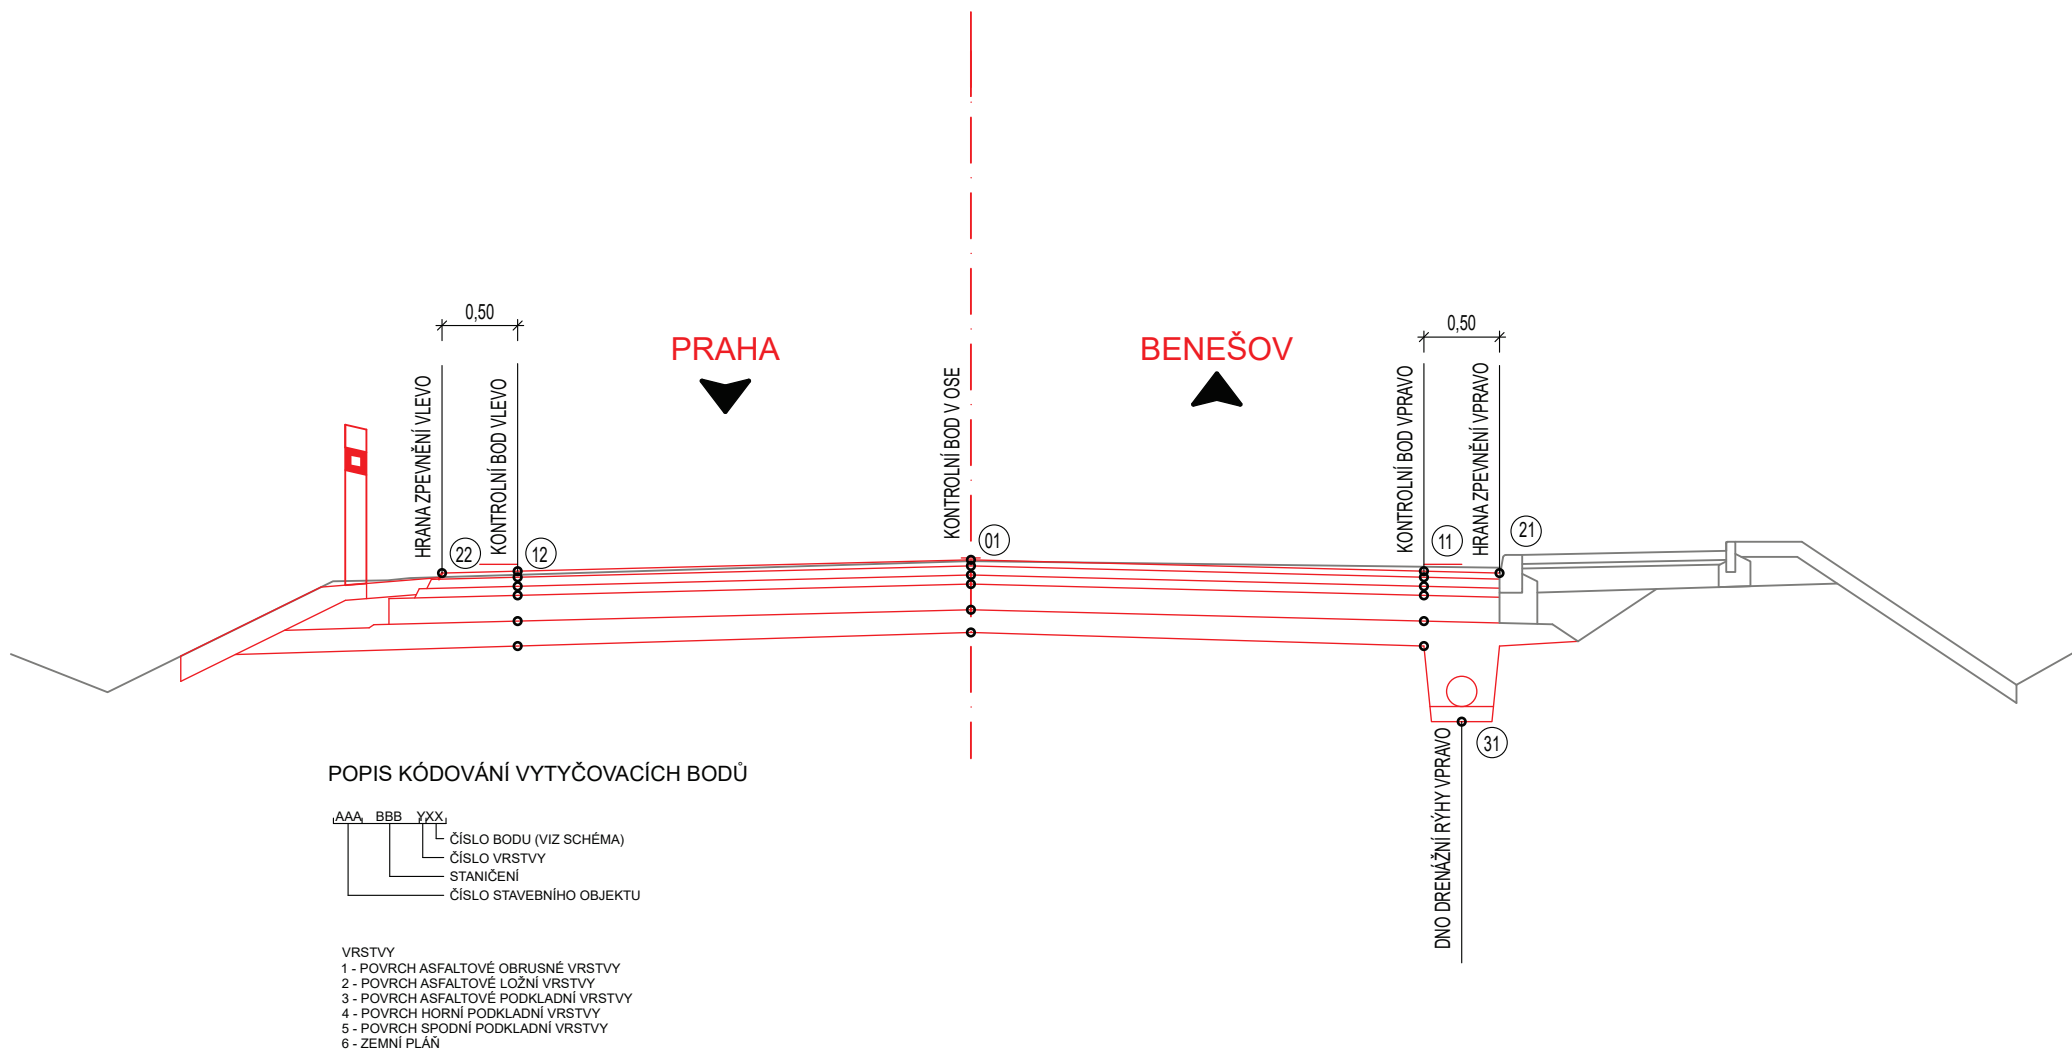

	21				11				01				12				22			
staničení	D	Y	X	Z	D	Y	X	Z	D	Y	X	Z	D	Y	X	Z	D	Y	X	Z
1,100	-5,338	734 782,464	1 062 074,637	474,779	-4,838	734 782,880	1 062 074,914	474,791	0,000	734 786,909	1 062 077,592	474,912	3,145	734 789,528	1 062 079,333	474,833	3,645	734 789,945	1 062 079,610	474,821
1,120	-7,029	734 769,984	1 062 090,357	475,548	-6,529	734 770,400	1 062 090,634	475,561	0,000	734 775,838	1 062 094,248	475,724	3,250	734 778,544	1 062 096,047	475,643	3,750	734 778,961	1 062 096,324	475,630
1,140	-7,146	734 758,815	1 062 106,949	476,395	-6,646	734 759,232	1 062 107,225	476,408	0,000	734 764,767	1 062 110,904	476,574	3,317	734 767,529	1 062 112,741	476,491	3,817	734 767,946	1 062 113,017	476,479
1,160	-5,737	734 748,918	1 062 124,385	477,379	-5,237	734 749,335	1 062 124,662	477,383	0,000	734 753,696	1 062 127,561	477,424	3,383	734 756,513	1 062 129,433	477,341	3,883	734 756,930	1 062 129,710	477,328
1,220	-3,516	734 717,554	1 062 175,583	479,282	-3,016	734 717,970	1 062 175,860	479,295	0,000	734 720,482	1 062 177,529	479,370	3,000	734 722,981	1 062 179,190	479,295	3,500	734 723,397	1 062 179,467	479,283
1,240	-3,425	734 706,559	1 062 192,290	479,647	-2,925	734 706,975	1 062 192,566	479,659	0,000	734 709,411	1 062 194,186	479,732	3,000	734 711,910	1 062 195,846	479,657	3,500	734 712,326	1 062 196,123	479,645
1,260	-3,468	734 695,452	1 062 208,923	479,898	-2,968	734 695,869	1 062 209,199	479,910	0,000	734 698,340	1 062 210,842	479,984	3,000	734 700,839	1 062 212,503	479,909	3,500	734 701,255	1 062 212,779	479,897
1,280	-3,577	734 684,290	1 062 225,518	480,056	-3,077	734 684,706	1 062 225,795	480,068	0,000	734 687,269	1 062 227,498	480,145	3,000	734 689,768	1 062 229,159	480,070	3,500	734 690,184	1 062 229,436	480,058
1,300	-3,500	734 673,230	1 062 242,113	480,189	-3,000	734 673,641	1 062 242,396	480,202	0,000	734 676,113	1 062 244,097	480,277	3,000	734 678,584	1 062 245,798	480,202	3,500	734 678,996	1 062 246,082	480,189

staničení	11				01				12			
	D	Y	X	Z	D	Y	X	Z	D	Y	X	Z
1,100	-4,838	734 782,880	1 062 074,914	474,751	0,000	734 786,909	1 062 077,592	474,872	3,145	734 789,528	1 062 079,333	474,793
1,120	-6,529	734 770,400	1 062 090,634	475,521	0,000	734 775,838	1 062 094,248	475,684	3,250	734 778,544	1 062 096,047	475,603
1,140	-6,646	734 759,232	1 062 107,225	476,368	0,000	734 764,767	1 062 110,904	476,534	3,317	734 767,529	1 062 112,741	476,451
1,160	-5,237	734 749,335	1 062 124,662	477,343	0,000	734 753,696	1 062 127,561	477,384	3,383	734 756,513	1 062 129,433	477,301
1,220	-3,016	734 717,970	1 062 175,860	479,255	0,000	734 720,482	1 062 177,529	479,330	3,000	734 722,981	1 062 179,190	479,255
1,240	-2,925	734 706,975	1 062 192,566	479,619	0,000	734 709,411	1 062 194,186	479,692	3,000	734 711,910	1 062 195,846	479,617
1,260	-2,968	734 695,869	1 062 209,199	479,870	0,000	734 698,340	1 062 210,842	479,944	3,000	734 700,839	1 062 212,503	479,869
1,280	-3,077	734 684,706	1 062 225,795	480,028	0,000	734 687,269	1 062 227,498	480,105	3,000	734 689,768	1 062 229,159	480,030
1,300	-3,000	734 673,641	1 062 242,396	480,162	0,000	734 676,113	1 062 244,097	480,237	3,000	734 678,584	1 062 245,798	480,162

staničení	11				01				12			
	D	Y	X	Z	D	Y	X	Z	D	Y	X	Z
1,100	-4,838	734 782,880	1 062 074,914	474,691	0,000	734 786,909	1 062 077,592	474,812	3,145	734 789,528	1 062 079,333	474,733
1,120	-6,529	734 770,400	1 062 090,634	475,461	0,000	734 775,838	1 062 094,248	475,624	3,250	734 778,544	1 062 096,047	475,543
1,140	-6,646	734 759,232	1 062 107,225	476,308	0,000	734 764,767	1 062 110,904	476,474	3,317	734 767,529	1 062 112,741	476,391
1,160	-5,237	734 749,335	1 062 124,662	477,283	0,000	734 753,696	1 062 127,561	477,324	3,383	734 756,513	1 062 129,433	477,241
1,220	-3,016	734 717,970	1 062 175,860	479,195	0,000	734 720,482	1 062 177,529	479,270	3,000	734 722,981	1 062 179,190	479,195
1,240	-2,925	734 706,975	1 062 192,566	479,559	0,000	734 709,411	1 062 194,186	479,632	3,000	734 711,910	1 062 195,846	479,557
1,260	-2,968	734 695,869	1 062 209,199	479,810	0,000	734 698,340	1 062 210,842	479,884	3,000	734 700,839	1 062 212,503	479,809
1,280	-3,077	734 684,706	1 062 225,795	479,968	0,000	734 687,269	1 062 227,498	480,045	3,000	734 689,768	1 062 229,159	479,970
1,300	-3,000	734 673,641	1 062 242,396	480,102	0,000	734 676,113	1 062 244,097	480,177	3,000	734 678,584	1 062 245,798	480,102

	11				01				12			
staničení	D	Y	X	Z	D	Y	X	Z	D	Y	X	Z
1,100	-4,838	734 782,880	1 062 074,914	474,631	0,000	734 786,909	1 062 077,592	474,752	3,145	734 789,528	1 062 079,333	474,673
1,120	-6,529	734 770,400	1 062 090,634	475,401	0,000	734 775,838	1 062 094,248	475,564	3,250	734 778,544	1 062 096,047	475,483
1,140	-6,646	734 759,232	1 062 107,225	476,248	0,000	734 764,767	1 062 110,904	476,414	3,317	734 767,529	1 062 112,741	476,331
1,160	-5,237	734 749,335	1 062 124,662	477,223	0,000	734 753,696	1 062 127,561	477,264	3,383	734 756,513	1 062 129,433	477,181
1,220	-3,016	734 717,970	1 062 175,860	479,135	0,000	734 720,482	1 062 177,529	479,210	3,000	734 722,981	1 062 179,190	479,135
1,240	-2,925	734 706,975	1 062 192,566	479,499	0,000	734 709,411	1 062 194,186	479,572	3,000	734 711,910	1 062 195,846	479,497
1,260	-2,968	734 695,869	1 062 209,199	479,750	0,000	734 698,340	1 062 210,842	479,824	3,000	734 700,839	1 062 212,503	479,749
1,280	-3,077	734 684,706	1 062 225,795	479,908	0,000	734 687,269	1 062 227,498	479,985	3,000	734 689,768	1 062 229,159	479,910
1,300	-3,000	734 673,641	1 062 242,396	480,042	0,000	734 676,113	1 062 244,097	480,117	3,000	734 678,584	1 062 245,798	480,042

	11				01				12			
staničení	D	Y	X	Z	D	Y	X	Z	D	Y	X	Z
1,100	-4,838	734 782,880	1 062 074,914	474,461	0,000	734 786,909	1 062 077,592	474,582	3,145	734 789,528	1 062 079,333	474,503
1,120	-6,529	734 770,400	1 062 090,634	475,231	0,000	734 775,838	1 062 094,248	475,394	3,250	734 778,544	1 062 096,047	475,313
1,140	-6,646	734 759,232	1 062 107,225	476,078	0,000	734 764,767	1 062 110,904	476,244	3,317	734 767,529	1 062 112,741	476,161
1,160	-5,237	734 749,335	1 062 124,662	477,053	0,000	734 753,696	1 062 127,561	477,094	3,383	734 756,513	1 062 129,433	477,011
1,220	-3,016	734 717,970	1 062 175,860	478,965	0,000	734 720,482	1 062 177,529	479,040	3,000	734 722,981	1 062 179,190	478,965
1,240	-2,925	734 706,975	1 062 192,566	479,329	0,000	734 709,411	1 062 194,186	479,402	3,000	734 711,910	1 062 195,846	479,327
1,260	-2,968	734 695,869	1 062 209,199	479,580	0,000	734 698,340	1 062 210,842	479,654	3,000	734 700,839	1 062 212,503	479,579
1,280	-3,077	734 684,706	1 062 225,795	479,738	0,000	734 687,269	1 062 227,498	479,815	3,000	734 689,768	1 062 229,159	479,740
1,300	-3,000	734 673,641	1 062 242,396	479,872	0,000	734 676,113	1 062 244,097	479,947	3,000	734 678,584	1 062 245,798	479,872

	31				11				01				12				32			
staničení	D	Y	X	Z	D	Y	X	Z	D	Y	X	Z	D	Y	X	Z	D	Y	X	Z
1,100	-5,088	734 782,672	1 062 074,776	473,787	-4,838	734 782,880	1 062 074,914	474,287	0,000	734 786,909	1 062 077,592	474,432	3,145	734 789,528	1 062 079,333	474,338	4,295	734 790,486	1 062 079,970	473,811
1,120	-6,779	734 770,192	1 062 090,495	474,548	-6,529	734 770,400	1 062 090,634	475,048	0,000	734 775,838	1 062 094,248	475,244	3,250	734 778,544	1 062 096,047	475,147	4,400	734 779,502	1 062 096,684	474,620
1,140	-6,896	734 759,024	1 062 107,087	475,395	-6,646	734 759,232	1 062 107,225	475,895	0,000	734 764,767	1 062 110,904	476,094	3,317	734 767,529	1 062 112,741	475,995	4,467	734 768,487	1 062 113,377	475,468
1,160	-5,487	734 749,126	1 062 124,524	476,398	-5,237	734 749,335	1 062 124,662	476,898	0,000	734 753,696	1 062 127,561	476,944	3,383	734 756,513	1 062 129,433	476,843	4,533	734 757,471	1 062 130,070	476,316
1,220	-3,266	734 717,762	1 062 175,721	478,300	-3,016	734 717,970	1 062 175,860	478,800	0,000	734 720,482	1 062 177,529	478,890	3,000	734 722,981	1 062 179,190	478,800	3,250	734 723,189	1 062 179,329	478,300
1,240	-3,175	734 706,767	1 062 192,428	478,664	-2,925	734 706,975	1 062 192,566	479,164	0,000	734 709,411	1 062 194,186	479,252	3,000	734 711,910	1 062 195,846	479,162	3,250	734 712,118	1 062 195,985	478,662
1,260	-3,218	734 695,661	1 062 209,061	478,915	-2,968	734 695,869	1 062 209,199	479,415	0,000	734 698,340	1 062 210,842	479,504	3,000	734 700,839	1 062 212,503	479,414	3,250	734 701,047	1 062 212,641	478,914
1,280	-3,327	734 684,498	1 062 225,656	479,073	-3,077	734 684,706	1 062 225,795	479,573	0,000	734 687,269	1 062 227,498	479,665	3,000	734 689,768	1 062 229,159	479,575	3,250	734 689,976	1 062 229,297	479,075
1,300	-3,250	734 673,435	1 062 242,254	479,517	-3,000	734 673,641	1 062 242,396	480,017	0,000	734 676,113	1 062 244,097	480,107	3,000	734 678,584	1 062 245,798	480,017	3,250	734 678,790	1 062 245,940	479,517