

REVIZE:	PŘEDMĚT ZMĚNY:	DATUM:	VYPRACOVAL:
a			
b			
c			

NÁZEV STAVBY: II/603 SULICE - ŽELIVEC, REK. SILNICE A MOSTŮ	ČÍSLO OBJEKTU: SO 104
---	---------------------------------

INVESTOR STAVBY č.1:  KRAJSKÁ SPRÁVA A ÚDRŽBA SILNIC STŘEDOČESKÉHO KRAJE p.o. Zborovská 81/11, 150 21 Praha 5	RAZÍTKO: DATUM: PODPIS:
--	---

INVESTOR STAVBY č.2:  OBEC KAMENICE Ringhofferovo náměstí 434 Olešovice, 251 68 Kamenice	RAZÍTKO: DATUM: PODPIS:
--	---

TECHNICKÝ DOZOR INVESTORA  REALSTAV MB, s.r.o. Klaudiánova 124, 293 01 Mladá Boleslav	RAZÍTKO: KONTROLOVAL: DATUM: PODPIS:
--	---

ZHOTOVITEL STAVBY:  M - SILNICE, a.s. Husova 1697, Bílé Předměstí, 530 03 Pardubice	RAZÍTKO: KONTROLOVAL: DATUM: PODPIS:
--	---

KOORDINÁTOR RDS:  M - PROJEKCE, s.r.o. Resslova 956/13, 500 02 Hradec Králové	RAZÍTKO: KONTROLOVAL: DATUM: PODPIS:
--	---

SOUŘADNICOVÝ SYSTÉM: S-JTSK

VÝŠKOVÝ SYSTÉM: B.P.V.

ČISTOPIS


NÁZEV STAVBY: II/603 SULICE - ŽELIVEC, REKONSTRUKCE SILNICE A MOSTŮ

ČÁST / STAVEBNÍ OBJEKT: SO 104 - SILNICE II/603 ÚSEK 4 - PROPUSTEK 1
--

PŘÍLOHA: VYTYČOVACÍ BODY

ZHOTOVITEL RDS:  M - PROJEKCE, s.r.o. Resslova 956/13 500 02 Hradec Králové	HLAVNÍ INŽENÝR PROJEKTU: Bc. R. MĚSTECKÝ					PARÉ:	
	ZODPOVĚDNÝ PROJEKTANT: Ing. M. STEJSKAL						
	VYPRACOVAL: Bc. R. MĚSTECKÝ						
	KONTROLA: Ing. P. KELČA						
	MĚŘÍTKO: Č. ZAKÁZKY: STUPEŇ: DATUM: ČÁST: PŘÍLOHA:						
-		25-118-03		RDS	06/2026	104	7

SCHÉMA VYTYČOVANÝCH BODŮ M 1:50

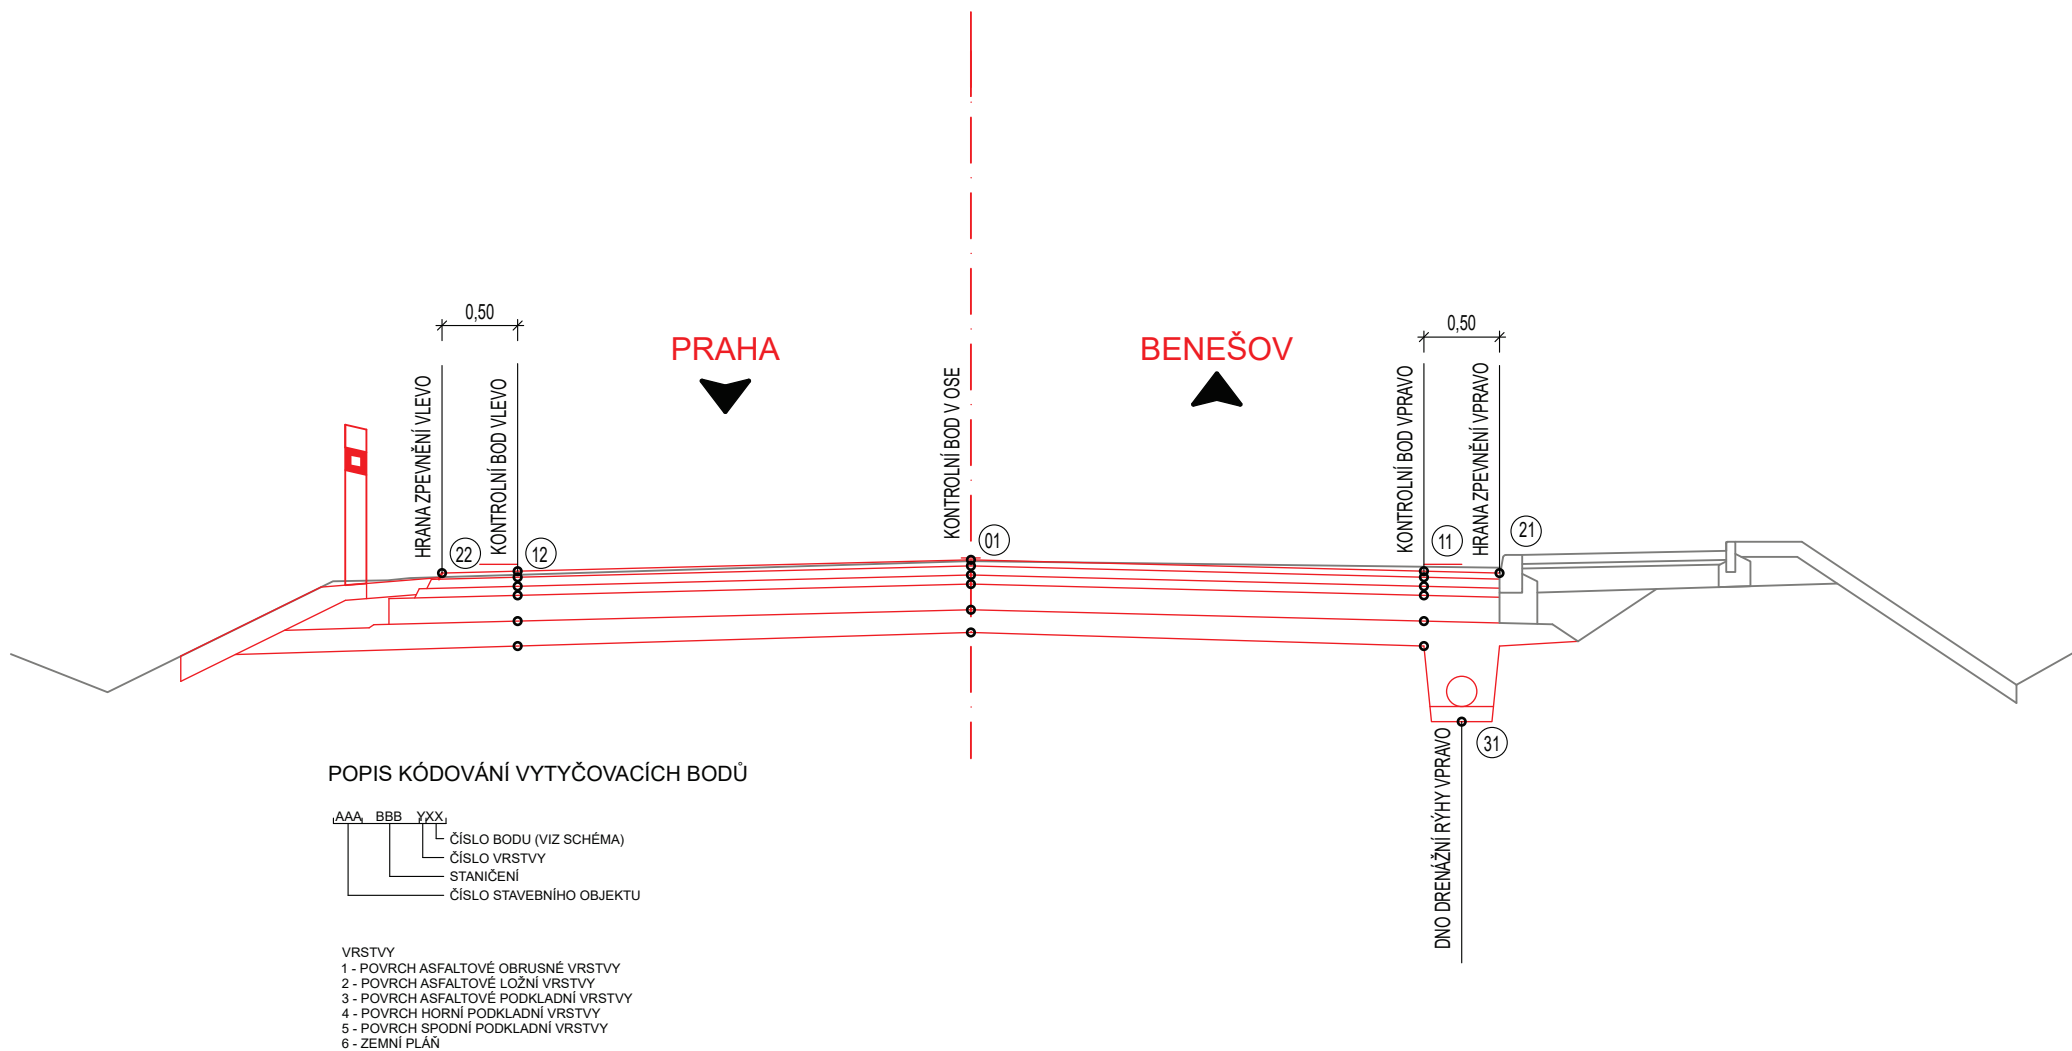

staničení	21				11				01				12				22			
	D	Y	X	Z	D	Y	X	Z	D	Y	X	Z	D	Y	X	Z	D	Y	X	Z
2,360	-3,792	733 980,502	1 063 039,208	434,859	-3,292	733 980,992	1 063 039,307	434,829	0,000	733 984,220	1 063 039,954	434,629	4,086	733 988,226	1 063 040,757	434,381	4,586	733 988,716	1 063 040,856	434,351
2,380	-3,660	733 977,630	1 063 059,369	434,382	-3,160	733 978,128	1 063 059,418	434,360	0,000	733 981,273	1 063 059,727	434,217	3,867	733 985,122	1 063 060,105	434,043	4,367	733 985,619	1 063 060,154	434,020
2,400	-3,691	733 976,609	1 063 079,689	433,914	-3,191	733 977,109	1 063 079,690	433,899	0,000	733 980,301	1 063 079,696	433,805	3,000	733 983,301	1 063 079,701	433,717	3,500	733 983,801	1 063 079,702	433,702
2,420	-3,667	733 977,374	1 063 099,936	433,508	-3,167	733 977,872	1 063 099,901	433,501	0,000	733 981,032	1 063 099,678	433,457	3,000	733 984,024	1 063 099,467	433,382	3,500	733 984,523	1 063 099,431	433,370
2,440	-3,500	733 979,463	1 063 119,991	433,236	-3,000	733 979,960	1 063 119,933	433,236	0,000	733 982,939	1 063 119,585	433,241	3,000	733 985,919	1 063 119,237	433,166	3,500	733 986,416	1 063 119,179	433,154
2,460	-3,500	733 982,021	1 063 139,893	432,997	-3,000	733 982,516	1 063 139,826	433,006	0,000	733 985,489	1 063 139,421	433,057	3,000	733 988,462	1 063 139,017	432,982	3,500	733 988,957	1 063 138,950	432,970

	11				01				12			
staničení	D	Y	X	Z	D	Y	X	Z	D	Y	X	Z
2,360	-3,292	733 980,992	1 063 039,307	434,789	0,000	733 984,220	1 063 039,954	434,589	4,086	733 988,226	1 063 040,757	434,341
2,380	-3,160	733 978,128	1 063 059,418	434,320	0,000	733 981,273	1 063 059,727	434,177	3,867	733 985,122	1 063 060,105	434,003
2,400	-3,191	733 977,109	1 063 079,690	433,859	0,000	733 980,301	1 063 079,696	433,765	3,000	733 983,301	1 063 079,701	433,677
2,420	-3,167	733 977,872	1 063 099,901	433,461	0,000	733 981,032	1 063 099,678	433,417	3,000	733 984,024	1 063 099,467	433,342
2,440	-3,000	733 979,960	1 063 119,933	433,196	0,000	733 982,939	1 063 119,585	433,201	3,000	733 985,919	1 063 119,237	433,126
2,460	-3,000	733 982,516	1 063 139,826	432,966	0,000	733 985,489	1 063 139,421	433,017	3,000	733 988,462	1 063 139,017	432,942

	11				01				12			
staničení	D	Y	X	Z	D	Y	X	Z	D	Y	X	Z
2,360	-3,292	733 980,992	1 063 039,307	434,729	0,000	733 984,220	1 063 039,954	434,529	4,086	733 988,226	1 063 040,757	434,281
2,380	-3,160	733 978,128	1 063 059,418	434,260	0,000	733 981,273	1 063 059,727	434,117	3,867	733 985,122	1 063 060,105	433,943
2,400	-3,191	733 977,109	1 063 079,690	433,799	0,000	733 980,301	1 063 079,696	433,705	3,000	733 983,301	1 063 079,701	433,617
2,420	-3,167	733 977,872	1 063 099,901	433,401	0,000	733 981,032	1 063 099,678	433,357	3,000	733 984,024	1 063 099,467	433,282
2,440	-3,000	733 979,960	1 063 119,933	433,136	0,000	733 982,939	1 063 119,585	433,141	3,000	733 985,919	1 063 119,237	433,066
2,460	-3,000	733 982,516	1 063 139,826	432,906	0,000	733 985,489	1 063 139,421	432,957	3,000	733 988,462	1 063 139,017	432,882

	11				01				12			
staničení	D	Y	X	Z	D	Y	X	Z	D	Y	X	Z
2,360	-3,292	733 980,992	1 063 039,307	434,669	0,000	733 984,220	1 063 039,954	434,469	4,086	733 988,226	1 063 040,757	434,221
2,380	-3,160	733 978,128	1 063 059,418	434,200	0,000	733 981,273	1 063 059,727	434,057	3,867	733 985,122	1 063 060,105	433,883
2,400	-3,191	733 977,109	1 063 079,690	433,739	0,000	733 980,301	1 063 079,696	433,645	3,000	733 983,301	1 063 079,701	433,557
2,420	-3,167	733 977,872	1 063 099,901	433,341	0,000	733 981,032	1 063 099,678	433,297	3,000	733 984,024	1 063 099,467	433,222
2,440	-3,000	733 979,960	1 063 119,933	433,076	0,000	733 982,939	1 063 119,585	433,081	3,000	733 985,919	1 063 119,237	433,006
2,460	-3,000	733 982,516	1 063 139,826	432,846	0,000	733 985,489	1 063 139,421	432,897	3,000	733 988,462	1 063 139,017	432,822

	11				01				12			
staničení	D	Y	X	Z	D	Y	X	Z	D	Y	X	Z
2,360	-3,292	733 980,992	1 063 039,307	434,499	0,000	733 984,220	1 063 039,954	434,299	4,086	733 988,226	1 063 040,757	434,051
2,380	-3,160	733 978,128	1 063 059,418	434,030	0,000	733 981,273	1 063 059,727	433,887	3,867	733 985,122	1 063 060,105	433,713
2,400	-3,191	733 977,109	1 063 079,690	433,569	0,000	733 980,301	1 063 079,696	433,475	3,000	733 983,301	1 063 079,701	433,387
2,420	-3,167	733 977,872	1 063 099,901	433,171	0,000	733 981,032	1 063 099,678	433,127	3,000	733 984,024	1 063 099,467	433,052
2,440	-3,000	733 979,960	1 063 119,933	432,906	0,000	733 982,939	1 063 119,585	432,911	3,000	733 985,919	1 063 119,237	432,836
2,460	-3,000	733 982,516	1 063 139,826	432,676	0,000	733 985,489	1 063 139,421	432,727	3,000	733 988,462	1 063 139,017	432,652

	31				11				01				12			
staničení	D	Y	X	Z	D	Y	X	Z	D	Y	X	Z	D	Y	X	Z
2,360					-3,292	733 980,992	1 063 039,307	434,349	0,000	733 984,220	1 063 039,954	434,149	4,086	733 988,226	1 063 040,757	433,901
2,380					-3,160	733 978,128	1 063 059,418	433,880	0,000	733 981,273	1 063 059,727	433,737	3,867	733 985,122	1 063 060,105	433,563
2,400					-3,191	733 977,109	1 063 079,690	433,419	0,000	733 980,301	1 063 079,696	433,323	3,000	733 983,301	1 063 079,701	433,233
2,420					-3,167	733 977,872	1 063 099,901	433,013	0,000	733 981,032	1 063 099,678	432,918	3,000	733 984,024	1 063 099,467	432,828
2,440	-3,250	733 979,711	1 063 119,962	432,242	-3,000	733 979,960	1 063 119,933	432,742	0,000	733 982,939	1 063 119,585	432,761	3,000	733 985,919	1 063 119,237	432,671
2,460	-3,250	733 982,269	1 063 139,859	431,987	-3,000	733 982,516	1 063 139,826	432,487	0,000	733 985,489	1 063 139,421	432,577	3,000	733 988,462	1 063 139,017	432,487