


SO 101 - SITUACE STAVBY
M 1:500

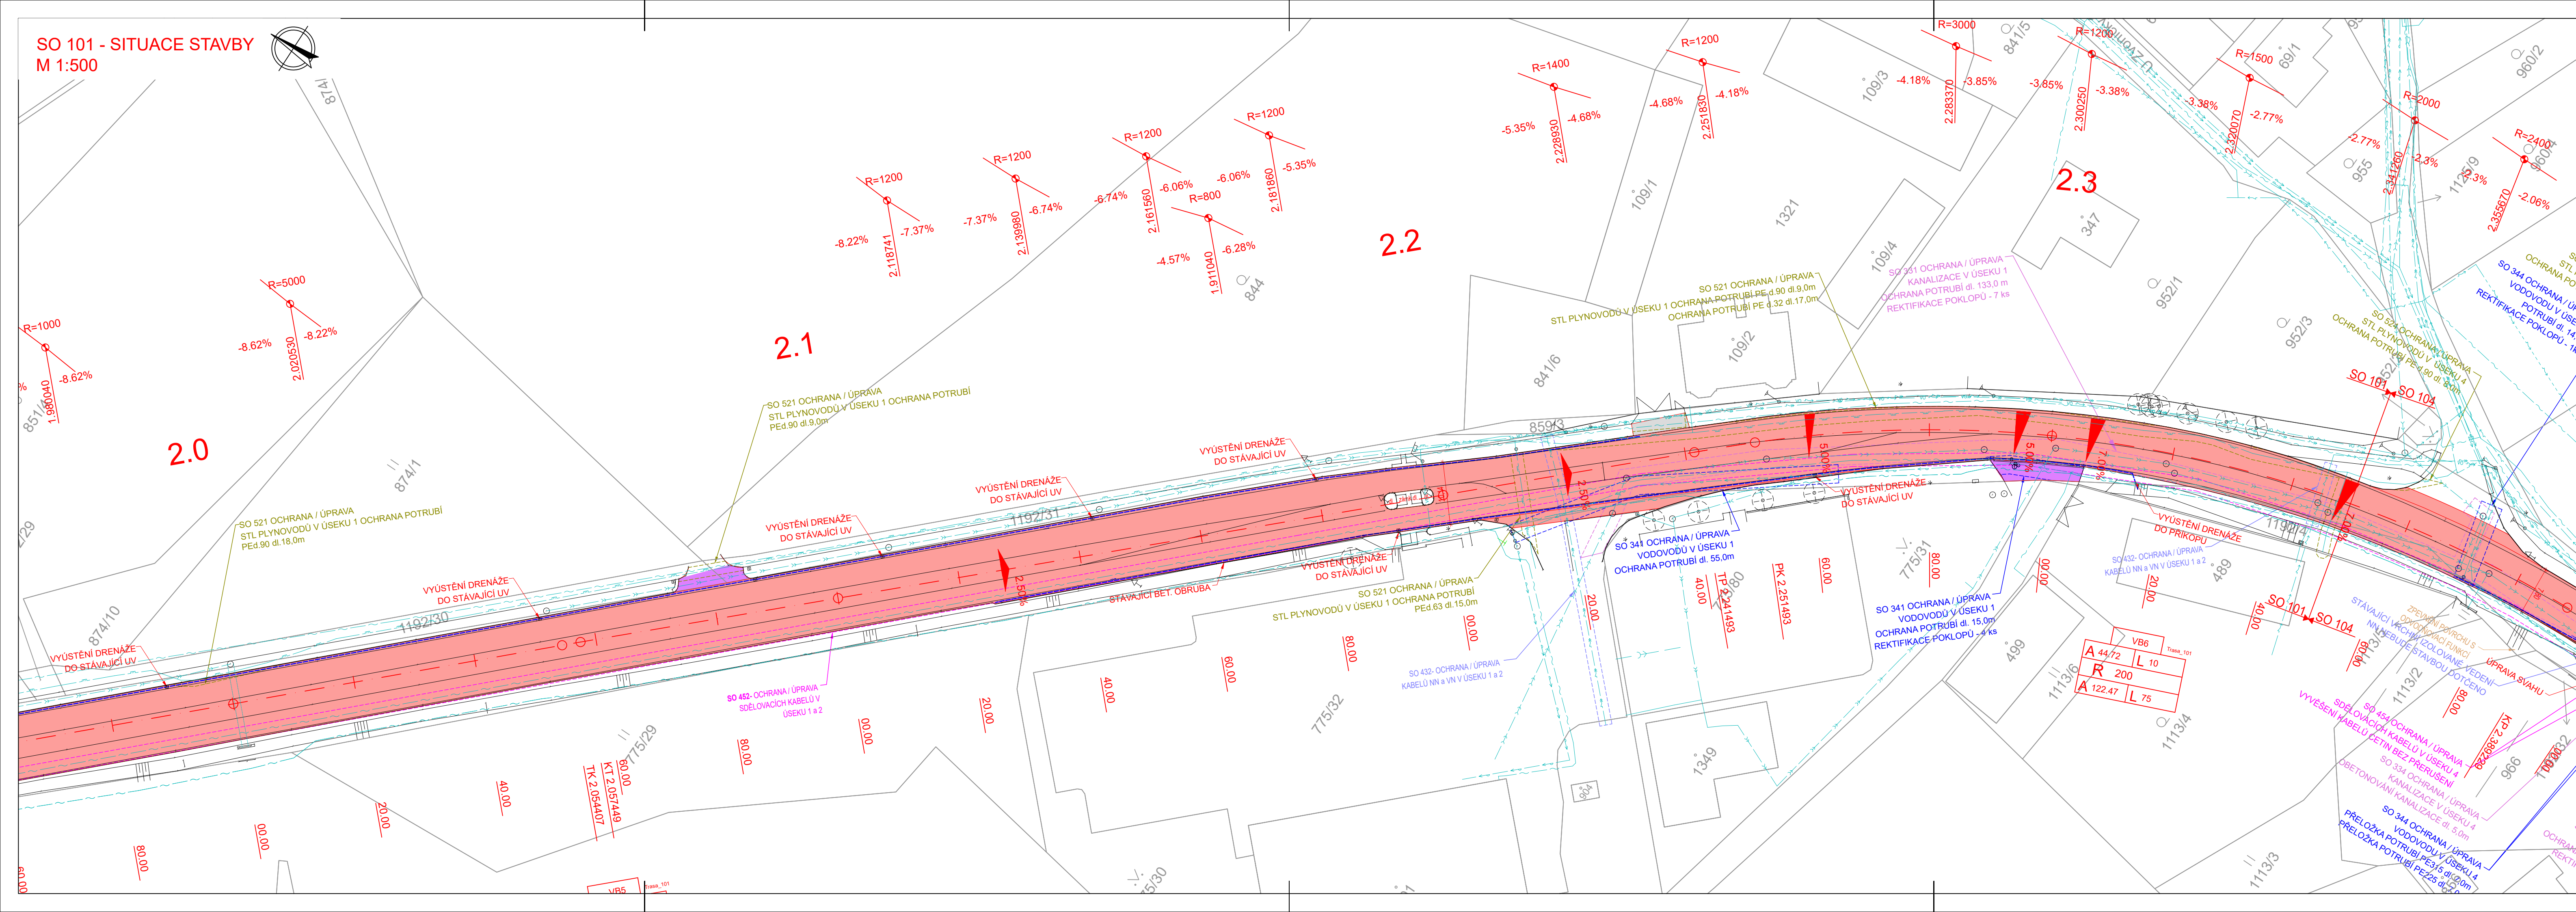

SEZNAM STAVEBNÍCH OBJEKTŮ:

100 - OBJEKTY POZEMNÍCH KOMUNIKACÍ

SO 101 - SILNICE II/603 ÚSEK 1 - INTRAVILÁN
SO 101.1 - SILNICE II/603 ÚSEK 1 - INTRAVILÁN CHODNÍK 2,721-2,797
SO 101.2 - OZELENÍ NEZPEVNĚNÉ PLOCHY ULICE RINGHOFFEROVA
SO 101.3 - SILNICE II/603 ÚSEK 1 - INTRAVILÁN - OPRAVA POVRCHU
SO 101.4 - SILNICE II/603 ÚSEK 1 - KOMPLEXNÍ OPRAVA 2,471-2,509
SO 102 - SILNICE II/603 ÚSEK 2 - EXTRAVILÁN
SO 103 - SILNICE II/603 ÚSEK 3 - OKRUŽNÍ KŘÍŽOVATKA
SO 104 - SILNICE II/603 ÚSEK 4 - PROPUSTEK 1
SO 105 - SILNICE II/603 ÚSEK 5 - PROPUSTEK 2
SO 106 - SILNICE II/603 ÚSEK 6 - NOVÁ HOSPODA
SO 107 - SILNICE II/603 ÚSEK 7 - ZPOMALOVACÍ OSTRŮVEK
SO 161 - DOPRAVNÍ INŽENÝRSKÉ OPATŘENÍ (NENÍ ZOBRAZENO)

300 - VODOHOSPODÁRSKÉ OBJEKTY

SO 331 - OCHRANA / ÚPRAVA KANALIZACE V ÚSEKU 1
SO 334 - OCHRANA / ÚPRAVA KANALIZACE V ÚSEKU 4
SO 335 - OCHRANA / ÚPRAVA KANALIZACE V ÚSEKU 5
SO 335.1 - OCHRANA / ÚPRAVA DEŠŤOVÉ KANALIZACE V ÚSEKU 5
SO 336 - OCHRANA / ÚPRAVA KANALIZACE V ÚSEKU 6
SO 337 - OCHRANA / ÚPRAVA KANALIZACE V ÚSEKU 7
SO 341 - OCHRANA / ÚPRAVA VODOVODŮ V ÚSEKU 1
SO 343 - OCHRANA / ÚPRAVA VODOVODŮ V ÚSEKU 3
SO 344 - OCHRANA / ÚPRAVA VODOVODŮ V ÚSEKU 4
SO 345 - OCHRANA / ÚPRAVA VODOVODŮ V ÚSEKU 5
SO 346 - OCHRANA / ÚPRAVA VODOVODŮ V ÚSEKU 6

400 - ELEKTRO A SDĚLOVACÍ OBJEKTY

SO 413 - PŘELOŽKA VEDENÍ VN V ÚSEKU 3
SO 414 - OCHRANA / ÚPRAVA VEDENÍ VN A VN V ÚSEKU 4
SO 432 - OCHRANA / ÚPRAVA KABELŮ NN A VN V ÚSEKU 1 A 2
SO 434 - OCHRANA / ÚPRAVA VEDENÍ NN V ÚSEKU 4
SO 435 - OCHRANA / ÚPRAVA VEDENÍ NN V ÚSEKU 5
SO 437 - OCHRANA / ÚPRAVA VEDENÍ NN V ÚSEKU 7
SO 441 - DOPLNĚNÍ A ÚPRAVA VO V ÚSEKU 1, KM 2,756
SO 443 - DOPLNĚNÍ A ÚPRAVA VO V ÚSEKU 3 - OK
SO 444 - OCHRANA / ÚPRAVA KABELŮ VO V ÚSEKU 4
SO 445 - OCHRANA / ÚPRAVA KABELŮ VO V ÚSEKU 5
SO 446 - OCHRANA / ÚPRAVA KABELŮ VO V ÚSEKU 6
SO 447 - DOPLNĚNÍ A ÚPRAVA VO V ÚSEKU 7 - ZPOMALOVACÍ OSTRŮVEK
SO 452 - OCHRANA / ÚPRAVA SDĚLOVACÍCH KABELŮ V ÚSEKU 1 A 2
SO 453 - OCHRANA / ÚPRAVA SDĚLOVACÍCH KABELŮ V ÚSEKU 3
SO 454 - OCHRANA / ÚPRAVA SDĚLOVACÍCH KABELŮ V ÚSEKU 4
SO 455 - OCHRANA / ÚPRAVA SDĚLOVACÍCH KABELŮ V ÚSEKU 5
SO 457 - OCHRANA / ÚPRAVA SDĚLOVACÍCH KABELŮ V ÚSEKU 7

500 - OBJEKTY TRUBNÍCH VEDENÍ

SO 515 - OCHRANA / ÚPRAVA VLT PLYNOVODŮ V ÚSEKU 5
SO 521 - OCHRANA / ÚPRAVA STL PLYNOVODŮ V ÚSEKU 1
SO 524 - OCHRANA / ÚPRAVA STL PLYNOVODŮ V ÚSEKU 4
SO 525 - OCHRANA / ÚPRAVA STL PLYNOVODŮ V ÚSEKU 5
SO 526 - OCHRANA / ÚPRAVA STL PLYNOVODŮ V ÚSEKU 6
SO 527 - OCHRANA / ÚPRAVA STL PLYNOVODŮ V ÚSEKU 7

LEGENDA:

ČÁRY A HRANY

- HRANY KOMUNIKACE
- OSA KOMUNIKACE
- SOUVISEJÍCÍ STAVBA
- ZAMĚŘENÍ STÁVAJÍCÍHO STAVU
- KATASTRÁLNÍ MAPA
- DRENÁŽ

PLOCHY

- PLOCHA KOMUNIKACE - SKLADBA 1 (INTRAVILÁN)
- PLOCHA KOMUNIKACE - SKLADBA 2 (EXTRAVILÁN)
- PLOCHA KOMUNIKACE - SKLADBA 3 (OPRAVA OBRUSU)
- PLOCHA KOMUNIKACE - SKLADBA 4 (POJÍZDNÁ DLAŽBA OK)
- PLOCHA KOMUNIKACE - SKLADBA 5 (NEPOJÍZDNÁ DLAŽBA CHODNÍKY)
- PLOCHA KOMUNIKACE - SKLADBA 6 (POJÍZDNÁ DLAŽBA)
- OBNOVA NÁPOJENÍ SJEZDŮ (ŠTĚRK)
- OBNOVA NÁPOJENÍ SJEZDŮ (DLAŽBA POJÍZDNÁ)
- OBNOVA NÁPOJENÍ SJEZDŮ (ASFALT)
- NEZPEVNĚNÁ KRAJNICE
- ZPEVNĚNÍ POVRCHU S ODVODŇOVACÍ FUNKCÍ
- OZELENÍ, NEZPEVNĚNÁ PLOCHA, TERÉNNÍ ÚPRAVY

LEGENDA INŽENÝRSKÝCH SÍTÍ:

STÁVAJÍCÍ

- VODOVOD, PŘÍPOJKY
- PODZEMNÍ VEDENÍ NN
- NADZEMNÍ VEDENÍ NN
- PODZEMNÍ VEDENÍ VN
- NADZEMNÍ VEDENÍ VN
- SDĚLOVACÍ VEDENÍ - BEZ ROZLUŠENÍ
- VEREJNÉ OSVĚTLENÍ
- PLYNOVÉ STL
- PLYNOVÉ VTL
- KANALIZACE - BEZ ROZLUŠENÍ

POZN. POLOHA INŽ. SÍTÍ JE POUZE ORIENTAČNÍ. PŘED PROVÁDĚNÍM STAVEBNÍCH PRACÍ JE NEZBYTNÉ PROVĚST VYTÝČENÍ VEŠKERÝCH INŽENÝRSKÝCH SÍTÍ.

REVIZE:	PŘEDMĚT ZMĚNY:	DATUM:	VYPRACOVAL:
a			
b			
c			

NÁZEV STAVBY: II/603 SULICE - ŽELIVEC, REK. SILNICE A MOSTŮ	ČÍSLO OBJEKTU: SO 101
--	--------------------------

INVESTOR STAVBY č.1: KRAJSKÁ SPRÁVA A ÚDRŽBA SILNIC STŘEDOČESKÉHO KRAJE p.o. Zborovská 81/11, 150 21 Praha 5	RAZÍTKO: DATUM: PODPIS:
---	----------------------------

INVESTOR STAVBY č.2: OBEC KAMENICE Ringhofferovo náměstí 434 Olešovice, 251 68 Kamenice	RAZÍTKO: DATUM: PODPIS:
---	----------------------------

TECHNICKÝ DOZOR INVESTORA REALSTAV MB, spol. s r.o. Klaudiánova 124, 293 01 Mladá Boleslav	RAZÍTKO: KONTOLOVAL: DATUM: PODPIS:
---	---

ZHOTOVITEL STAVBY: M - SILNICE, a.s. Husova 1697, Bílé Předměstí, 530 03 Pardubice	RAZÍTKO: KONTOLOVAL: DATUM: PODPIS:
---	---

KOORDINÁTOR RDS: M - PROJEKCE, s.r.o. Resslova 956/13, 500 02 Hradec Králové	RAZÍTKO: KONTOLOVAL: DATUM: PODPIS:
---	---

SOUŘADNICOVÝ SYSTÉM: S-JTSK
VÝŠKOVÝ SYSTÉM: B.P.V.

ETAPA 1+2 (KM 0,000-2,880)

ČISTOPIS

NÁZEV STAVBY: II/603 SULICE - ŽELIVEC, REKONSTRUKCE SILNICE A MOSTŮ					
ČÁST / STAVEBNÍ OBJEKT: SO 101 - SILNICE II/603 ÚSEK 1 - INTRAVILÁN					
PŘÍLOHA: SITUACE STAVBY (KM 1,980 - 2,360)					
ZHOTOVITEL RDS: M - PROJEKCE, s.r.o. Resslova 956/13 500 02 Hradec Králové	HLAVNÍ INŽENÝR PROJEKTU: Bc. R. MĚSTECKÝ	PARÉ:			
	ZODPOVĚDNÝ PROJEKTANT: Ing. M. STEJSKAL				
	VYPRACOVAL: Ing. M. ŠPRONGL				
	KONTROLA: Ing. P. KELČA				
	MĚŘÍTKO: 1:500	Č. ZAKÁZKY: 25-118-03	STUPEŇ: RDS	DATUM: 06/2026	ČÁST: 101
					PŘÍLOHA: 2.4