

SO 101 - PODÉLNÝ PROFIL - 2. ČÁST
M 1:1000/100

DRUH POVRCHU ÚZEMÍ:
KATASTRÁLNÍ ÚZEMÍ:
OKRES:
KRAJ:

OSTATNÍ PLOCHA - silnice
SULICE (759431)
PRAHA - VÝCHOD
STŘEDOČESKÝ

OSTATNÍ PLOCHA - silnice
SULICE (759431)
PRAHA - V
STŘEDOČESKÝ

SKLONOVÉ POMĚRY

DRENÁŽ VPRAVO
DRENÁŽ VLEVO

MĚŘITKA:
1: 1000, 1: 100

KÓTY NIVELETY


KÓTY TERÉNU

SROVNÁVACÍ ROVINA:

STANIČENÍ

VZDÁLENOST PŘ. ŘEZŮ:

SMĚROVÉ POMĚRY

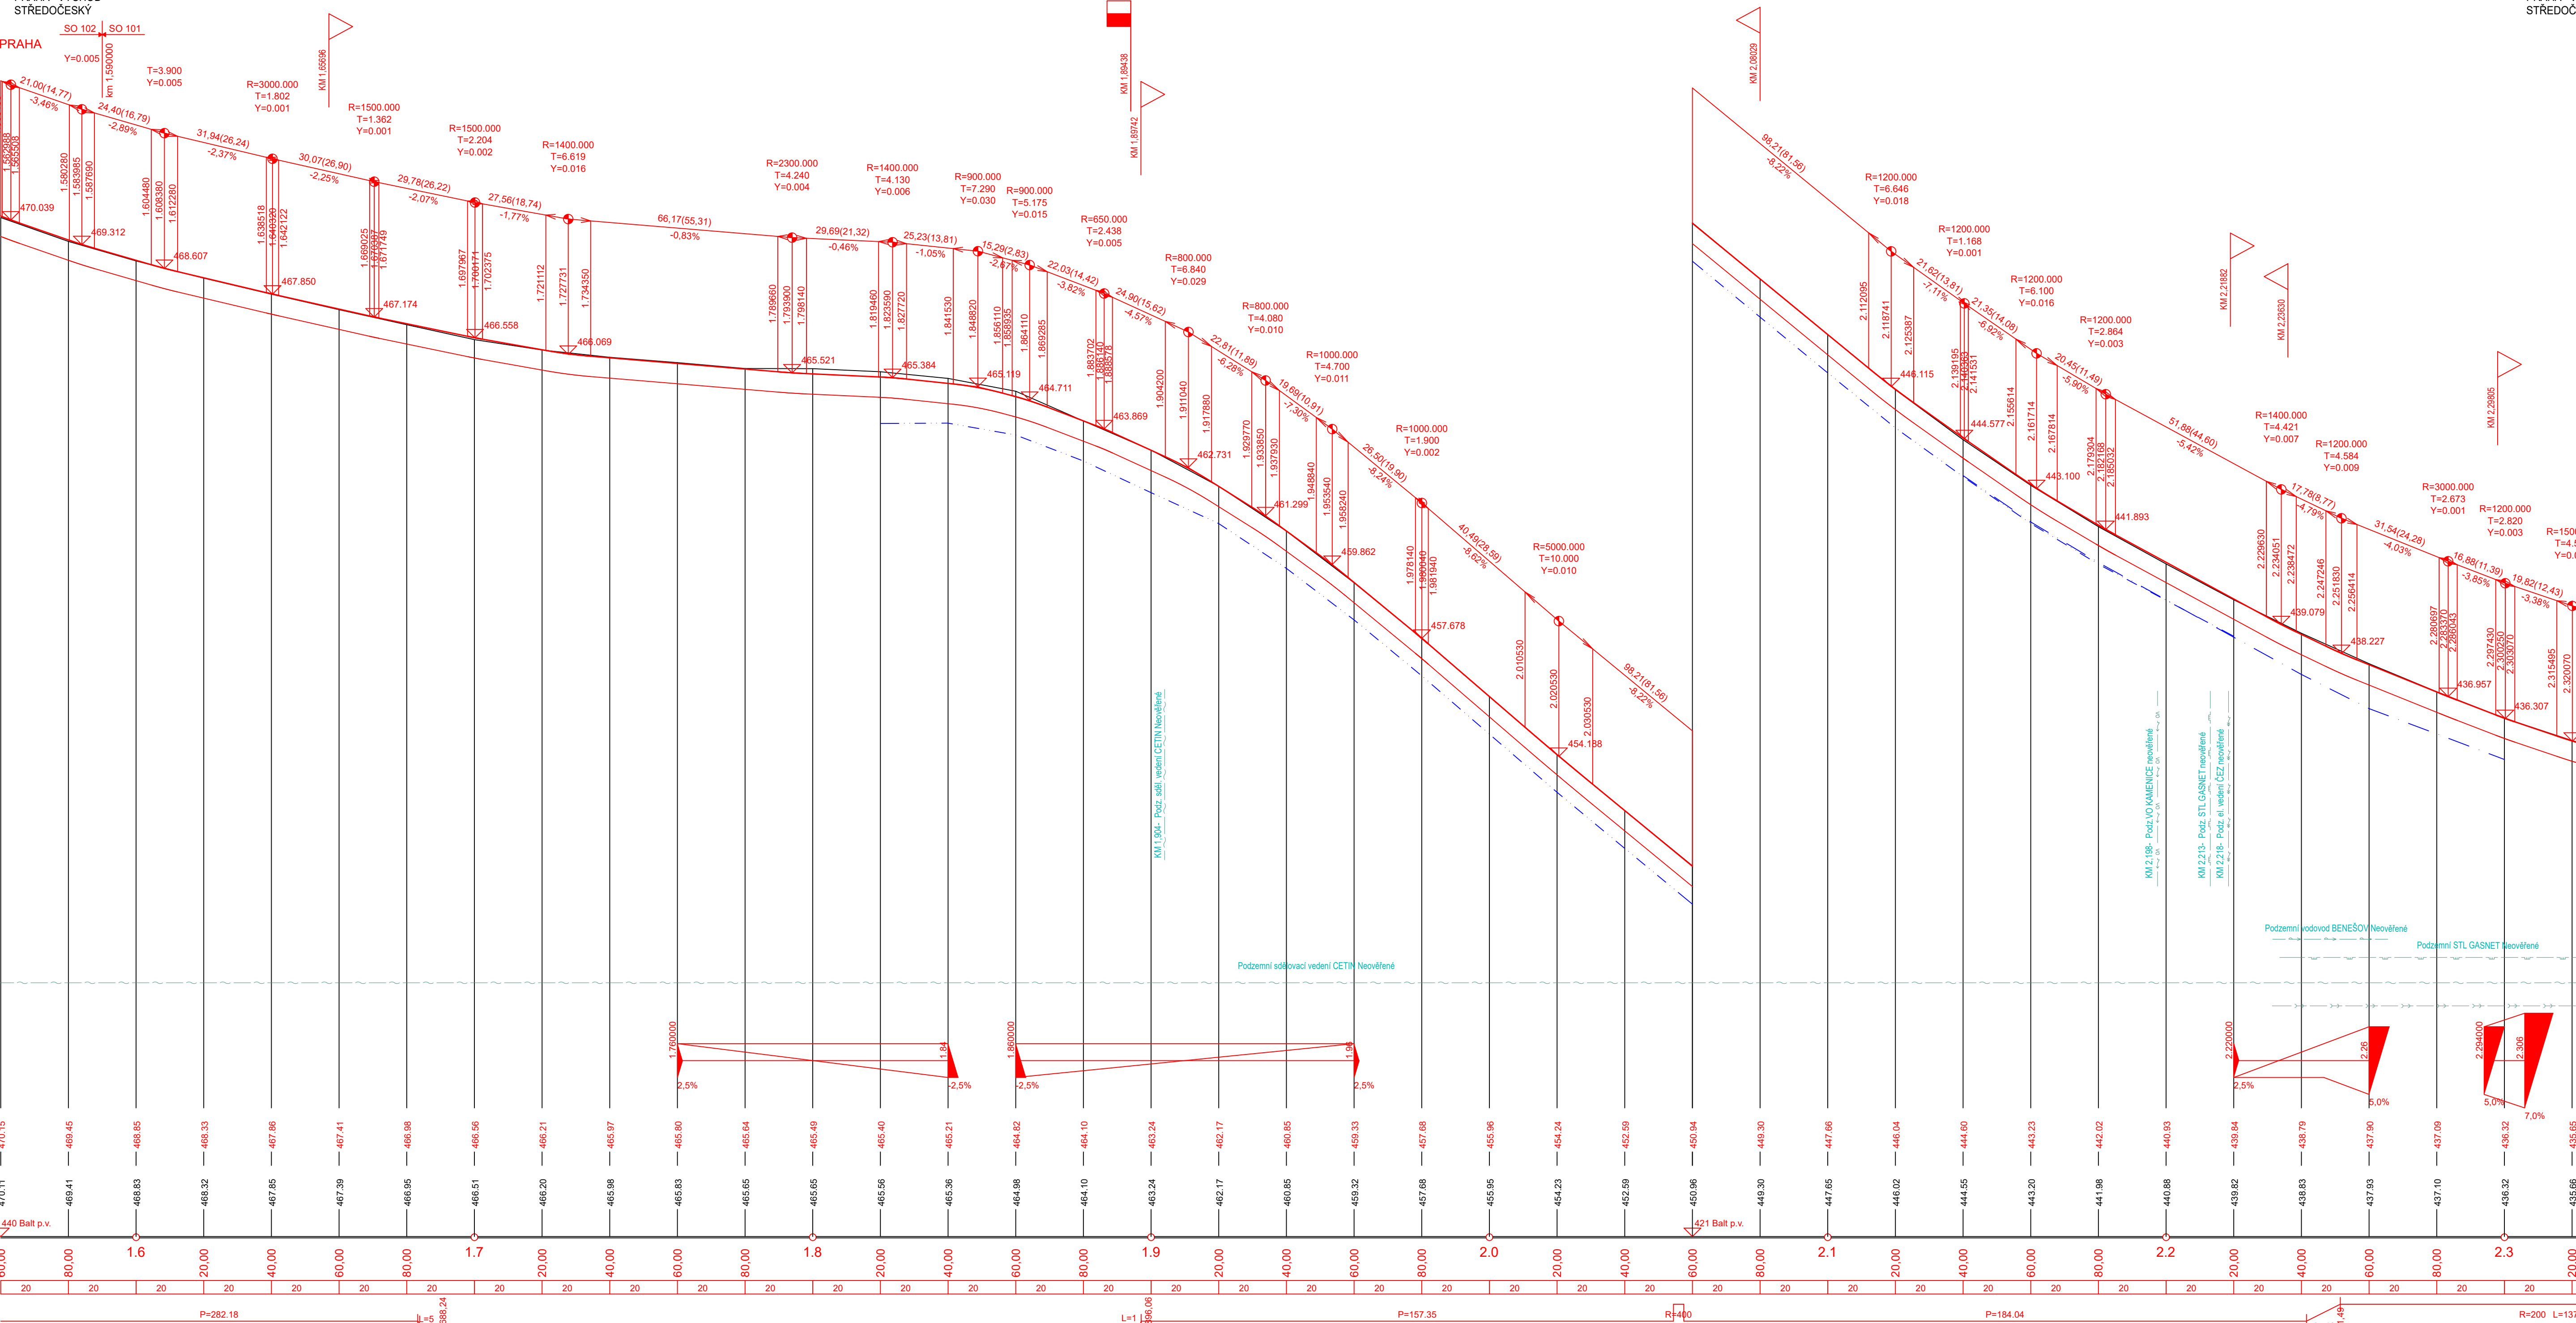

REVIZE:	PŘEDMĚT ZMĚNY:	DATUM:	VYPRACOVAL:
a			
b			
c			
NÁZEV STAVBY: II/603 SULICE - ŽELIVEC, REK. SILNICE A MOSTŮ		ČÍSLO OBJEKTU: SO 101	
INVESTOR STAVBY č. 1:  KRAJSKÁ SPRÁVA A ÚDRŽBA SILNIC STŘEDOČESKÉHO KRAJE p.o. Zborovská 81/11, 150 21 Praha 5		RAŽITKO: DATUM: PODPIS:	
INVESTOR STAVBY č. 2:  OBEC KAMENICE Ringhofferovo náměstí 434 Olešovice, 251 68 Kamenice		RAŽITKO: DATUM: PODPIS:	
TECHNICKÝ DOZOR INVESTORA  REALSTAV MB, s.r.o. Klaudiánova 124, 293 01 Mladá Boleslav		RAŽITKO: KONTROLOVAL: DATUM: PODPIS:	
ZHOTOVITEL STAVBY:  M - SILNICE, a.s. Husova 1697, Bílé Předměstí, 530 03 Pardubice		RAŽITKO: KONTROLOVAL: DATUM: PODPIS:	
KOORDINÁTOR RDS:  M - PROJEKCE, s.r.o. Reslsova 956/13, 500 02 Hradec Králové		RAŽITKO: KONTROLOVAL: DATUM: PODPIS:	

SOUŘADNICOVÝ SYSTÉM: S-JTSK VÝŠKOVÝ SYSTÉM: B.P.V.		ETAPA 1+2 (KM 0,000-2,880)		ČISTOPIS	
NÁZEV STAVBY: II/603 SULICE - ŽELIVEC, REKONSTRUKCE SILNICE A MOSTŮ					
ČÁST / STAVEBNÍ OBJEKT: SO 101 - SILNICE II/603 ÚSEK 1 - INTRAVILÁN					
PŘÍLOHA: PODÉLNÝ PROFIL - 2. ČÁST					
ZHOTOVITEL RDS:  M - PROJEKCE, s.r.o. Reslsova 956/13 500 02 Hradec Králové		HLAVNÍ INŽENÝR PROJEKTU: Bc. R. MĚSTECKÝ ZODPOVĚDNÝ PROJEKTANT: Ing. M. STEJSKAL VYPRACOVAL: Bc. R. MĚSTECKÝ KONTROLA: Ing. P. KELČA		PARÉ:   	
		MĚŘITKO: Č. ZAKÁZKY: STUPEŇ: DATUM: ČÁST: PŘÍLOHA: 1:1000/100 25-118-03 RDS 06/2026 101 3.2			