


SO 101 - PODÉLNÝ PROFIL - 3. ČÁST
M 1:1000/100

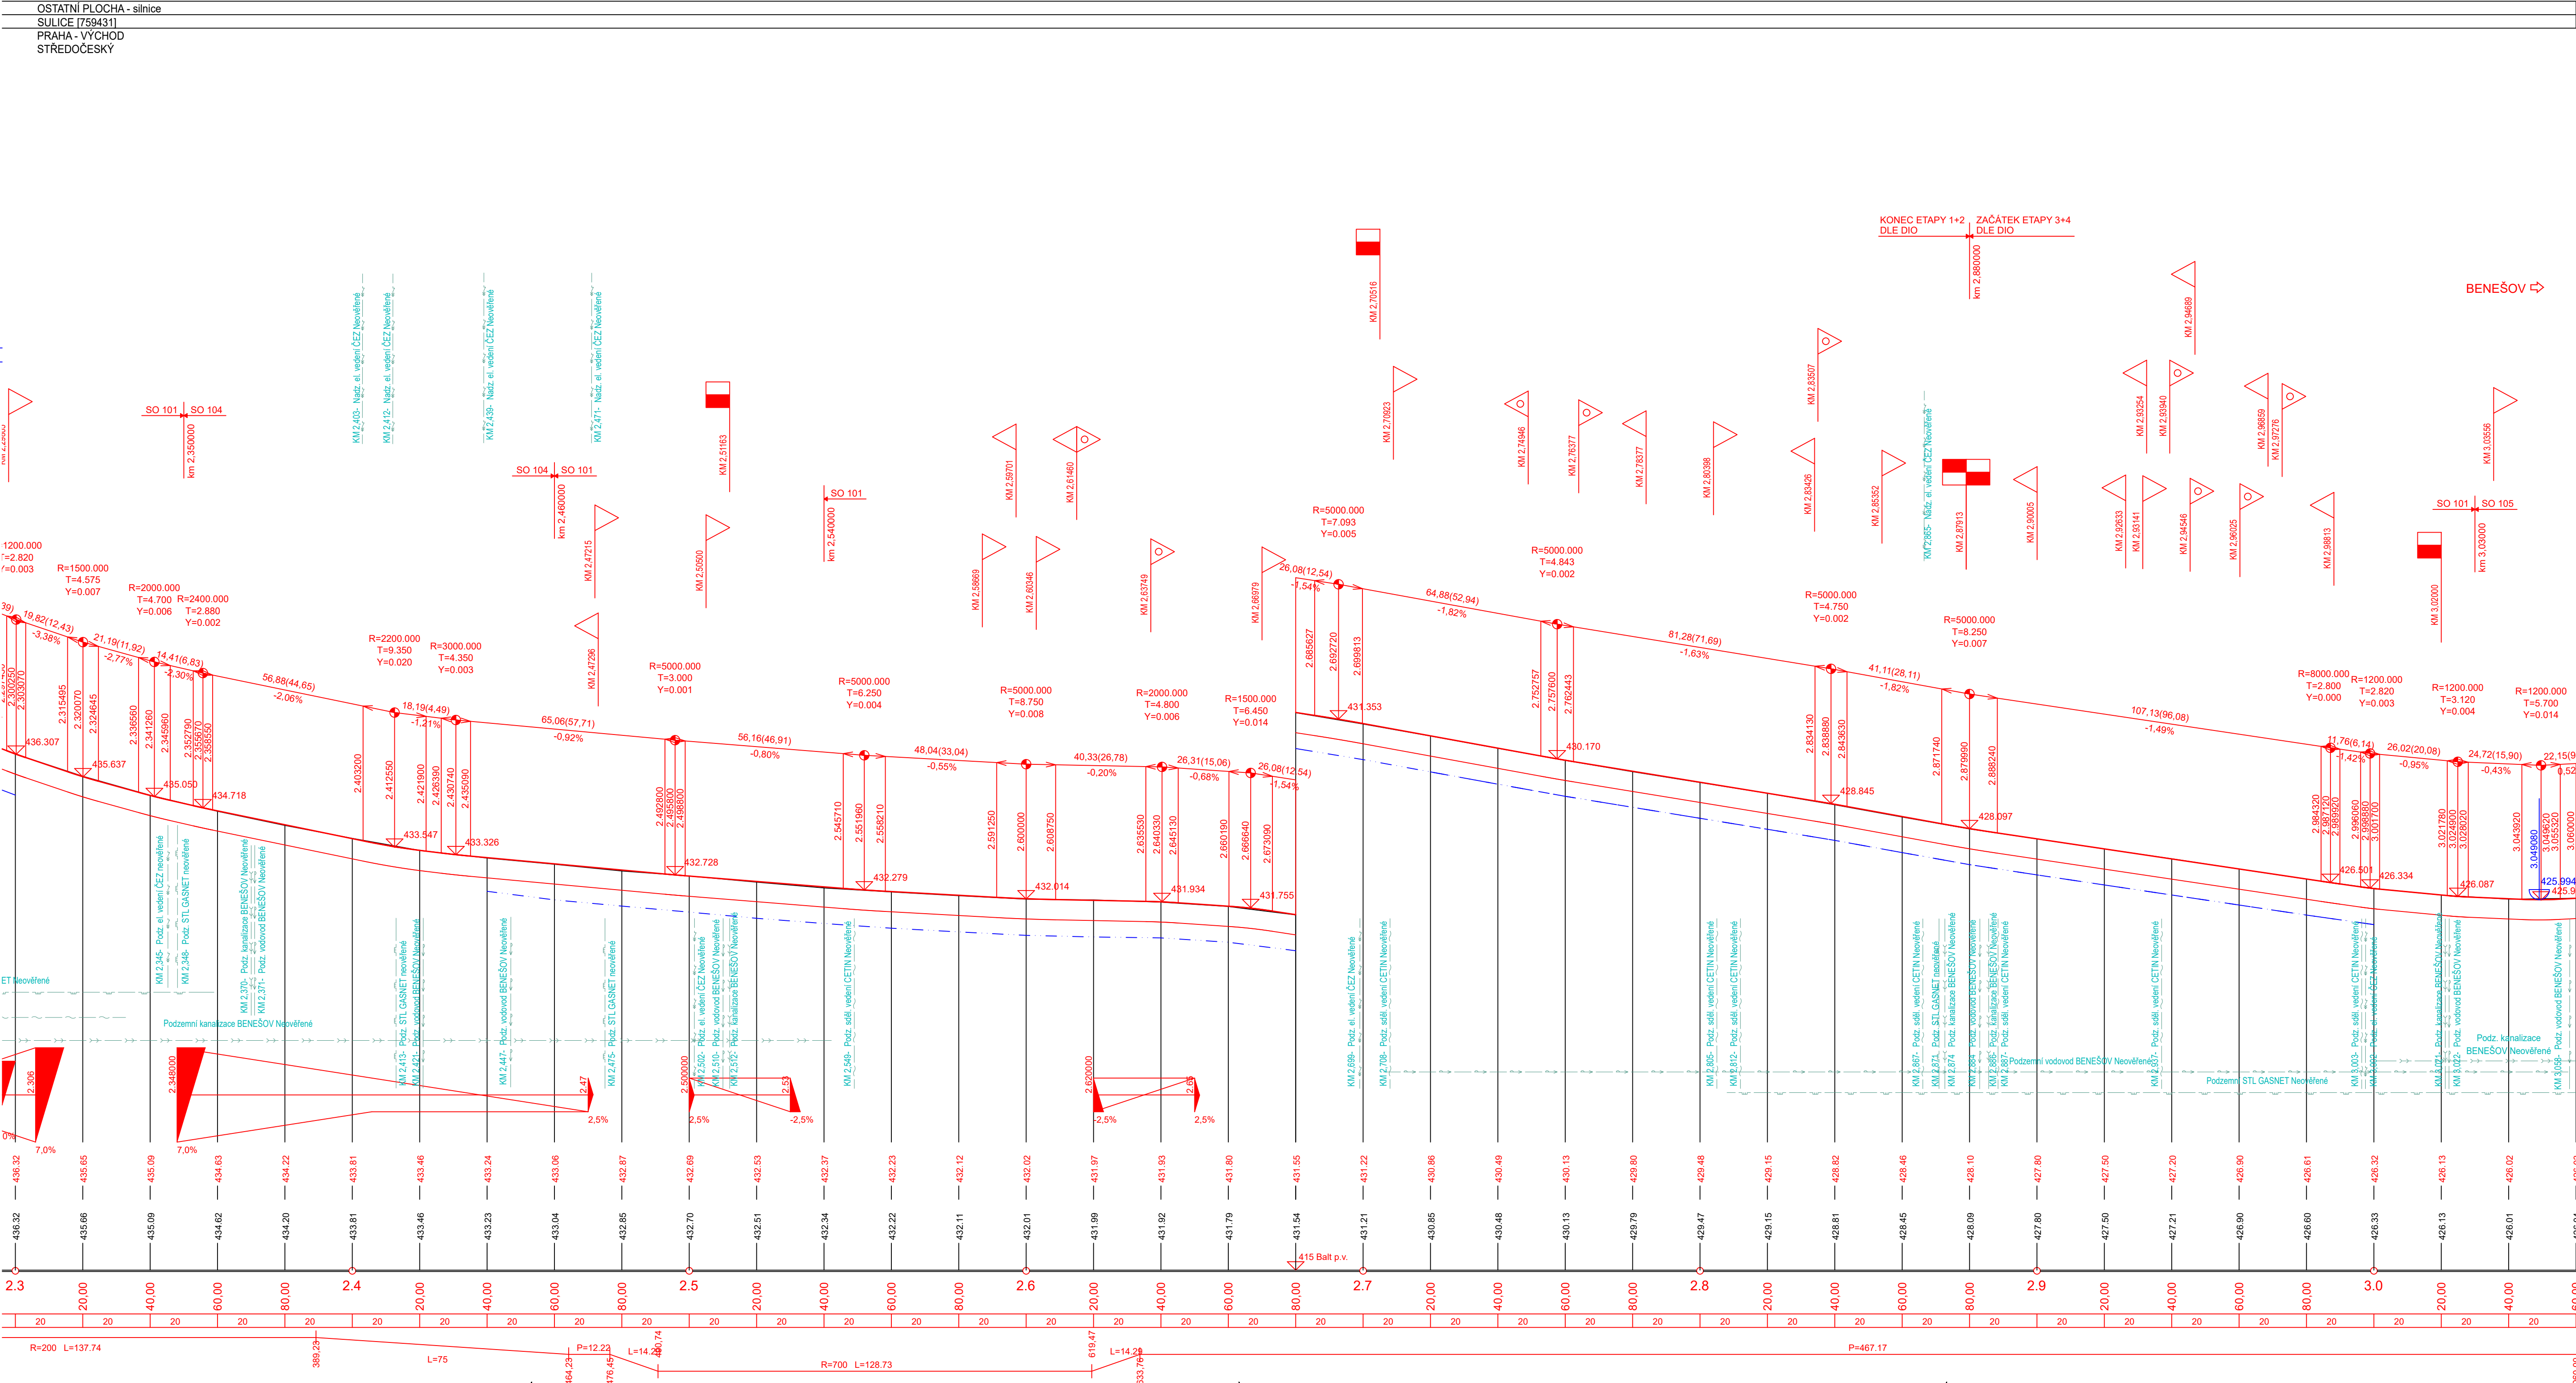

REVIZE:	PŘEDMĚT ZMĚNY:	DATUM:	VYPRACOVAL:
a			
b			
c			
NÁZEV STAVBY: II/603 SULICE - ŽELIVEC, REK. SILNICE A MOSTŮ		ČÍSLO OBJEKTU: SO 101	
INVESTOR STAVBY č.1: K SÚS KRAJSKÁ SPRÁVA A ÚDRŽBA SILNIC STŘEDOČESKÉHO KRAJE p.o. Zborovská 81/11, 150 21 Praha 5		RAŽITKO: DATUM: PODPIS:	
INVESTOR STAVBY č.2: O B E C K A M E N I C E Ringhofferovo náměstí 434 Olešovice, 251 68 Kamenice		RAŽITKO: DATUM: PODPIS:	
TECHNICKÝ DOZOR INVESTORA REALSTAV MB spol. s r.o. Klaudánova 124, 293 01 Mladá Boleslav		RAŽITKO: KONTROLOVAL: DATUM: PODPIS:	
ZHOTOVITEL STAVBY: M - SILNICE Husova 1697, Bílé Předměstí, 530 03 Pardubice		RAŽITKO: KONTROLOVAL: DATUM: PODPIS:	
KOORDINÁTOR RDS: M - PROJEKCE Reslsova 956/13, 500 02 Hradec Králové		RAŽITKO: KONTROLOVAL: DATUM: PODPIS:	

SOUŘADNICOVÝ SYSTÉM: S-JTSK VÝŠKOVÝ SYSTÉM: B.P.V.		ETAPA 1+2 (KM 0,000-2,880)		ČISTOPIS		
NÁZEV STAVBY: II/603 SULICE - ŽELIVEC, REKONSTRUKCE SILNICE A MOSTŮ						
ČÁST / STAVEBNÍ OBJEKT: SO 101 - SILNICE II/603 ÚSEK 1 - INTRAVILÁN						
PŘÍLOHA: PODÉLNÝ PROFIL - 3. ČÁST						
ZHOTOVITEL RDS:  M - PROJEKCE, s.r.o. Reslsova 956/13 500 02 Hradec Králové		HLAVNÍ INŽENÝR PROJEKTU: Bc. R. MĚSTECKÝ			PARÉ:	
		ZODPOVĚDNÝ PROJEKTANT: Ing. M. STEJSKAL				
		VYPRACOVAL: Bc. R. MĚSTECKÝ				
		KONTROLA: Ing. P. KELČA				
MĚŘITKO: 1:1000/100		Č. ZAKÁZKY: 25-118-03	STUPEŇ: RDS	DATUM: 06/2026	ČÁST: 101	PŘÍLOHA: 3.3