

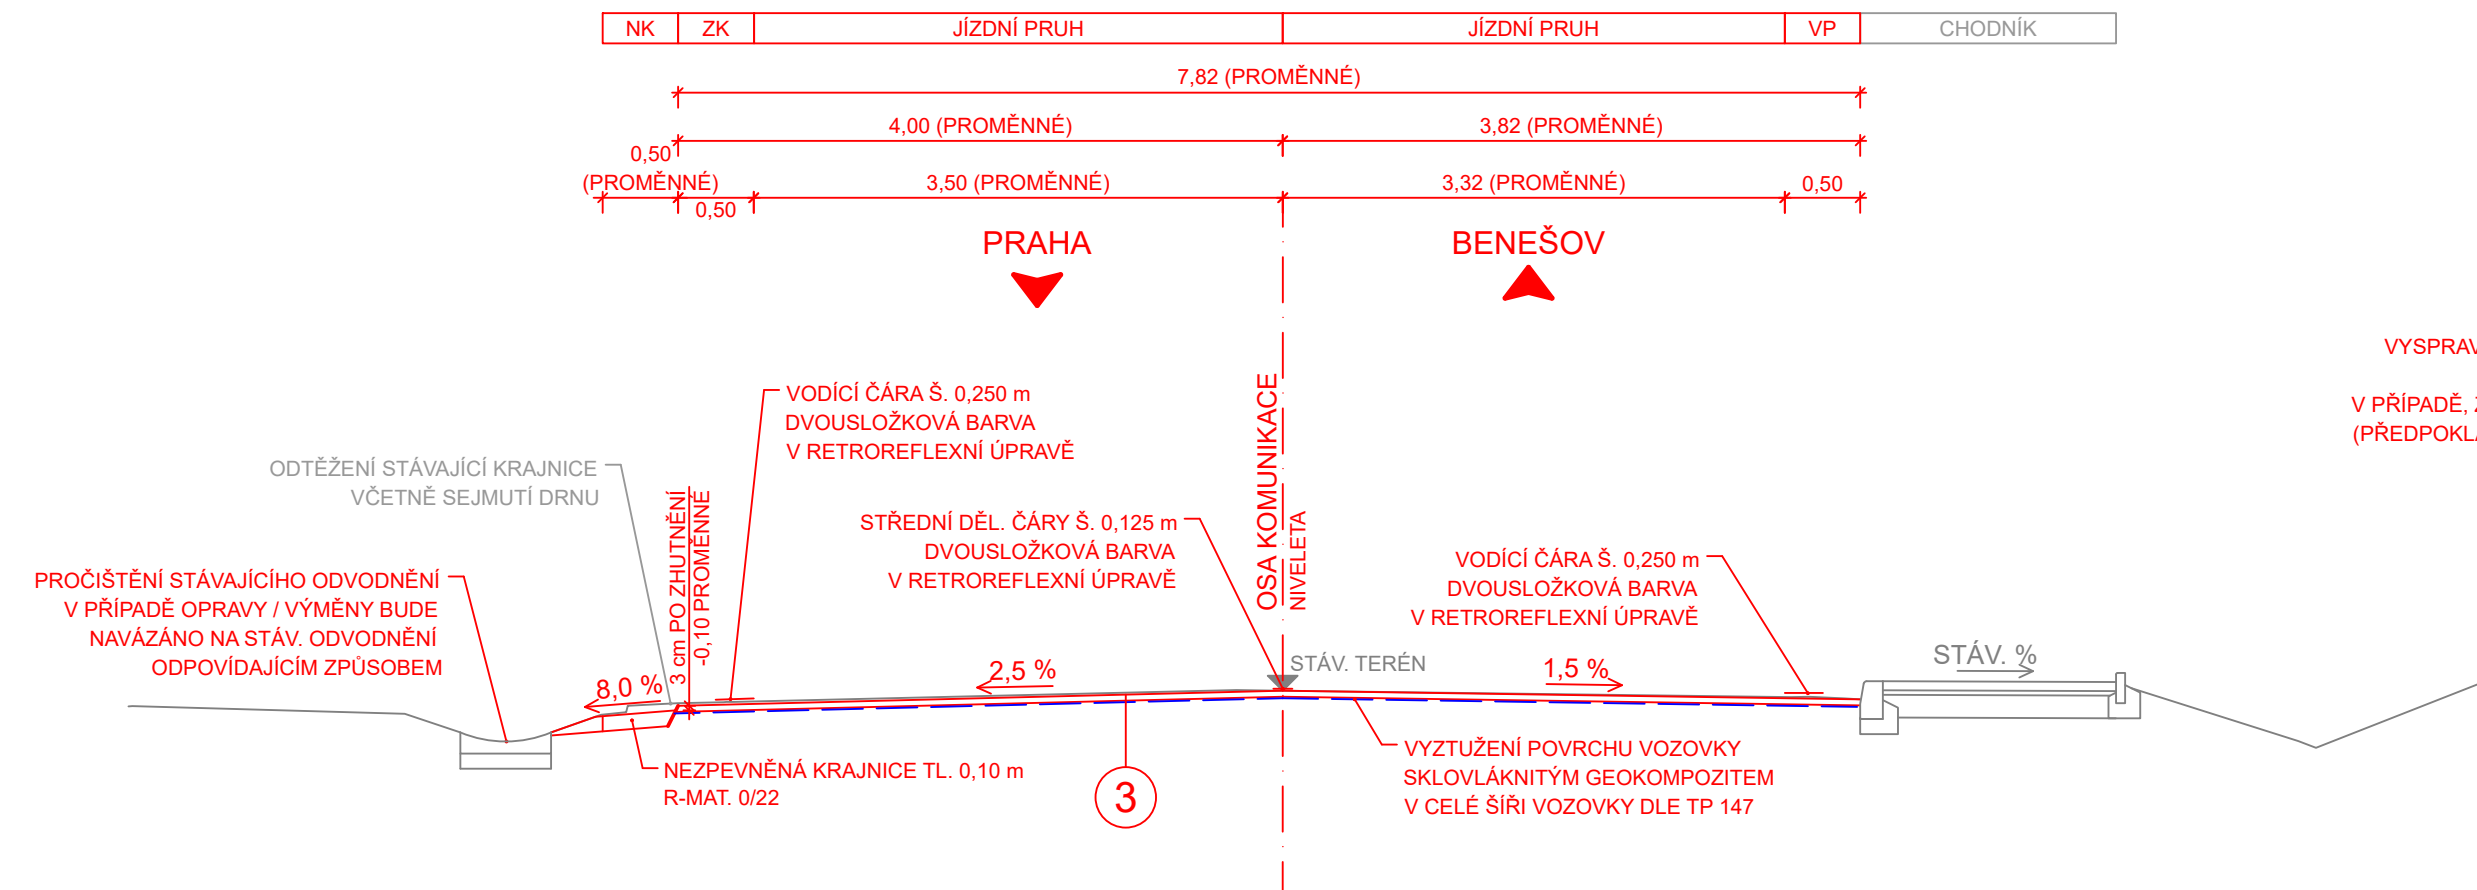


SO 101 - VZOROVÉ PŘÍČNÉ ŘEZY
M 1:50, M 1:25

SO 101.3 - SILNICE II/603
≈ MS-/8/50 ODVOZENÁ
INTRAVILÁN OPRAVA
OBRUSU (KM 0,000-0,190)

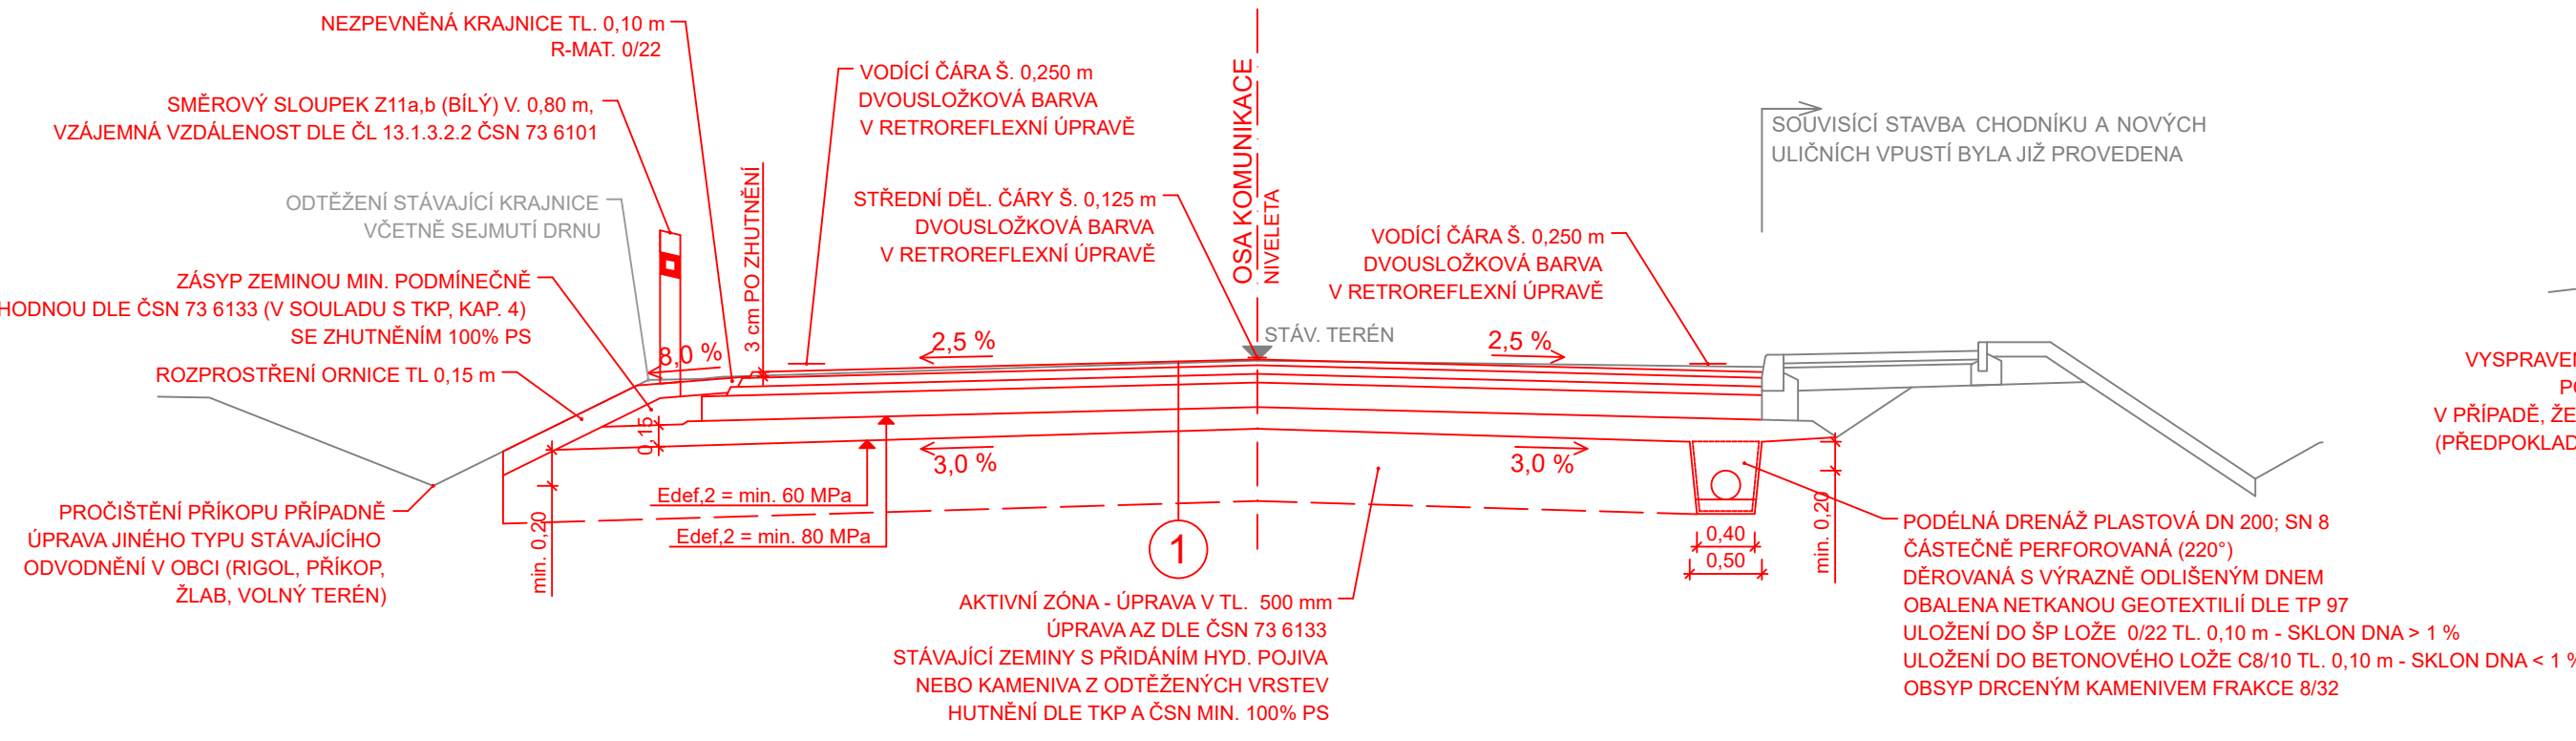


SO 101 - SILNICE II/603
≈ MS2 -/8/50 ODVOZENÁ
INTRAVILÁN (KM 0,600)

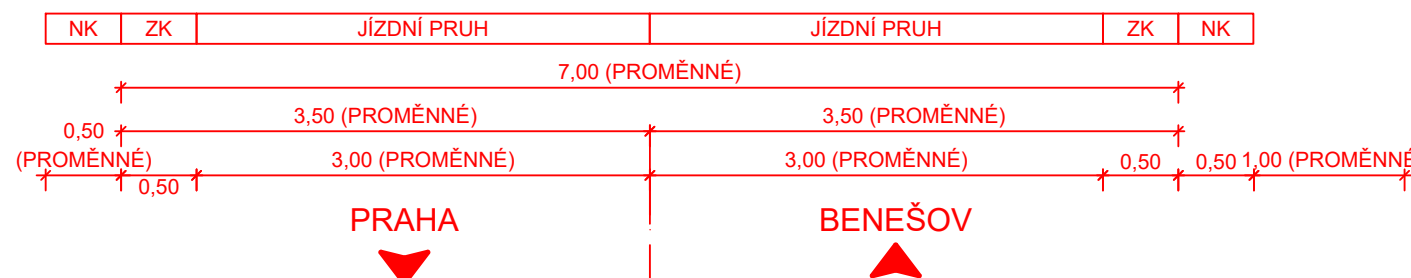

DETAIL A - NÁPOJENÍ KONSTRUKCÍ


M 1:50

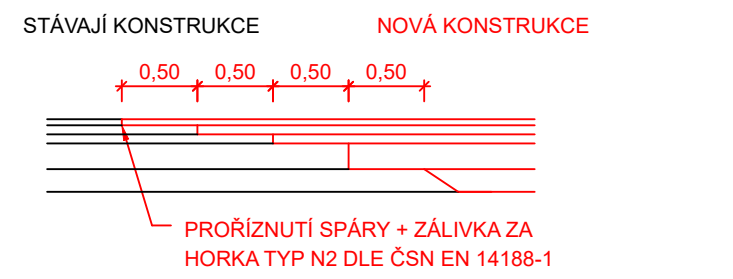


DETAIL B - OPRAVY PORUCH NA

ODFRÉZOVANÉM ASFALT. POVRCHU

M 1:50

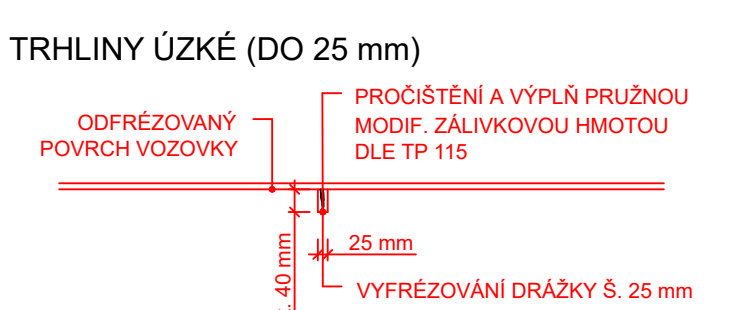


TRHLINY ŠÍROKÉ (NAD 25 mm),
ROZVĚTVENÉ NEBO MOZAIKOVÉ
(PLOŠNÁ SANACE)

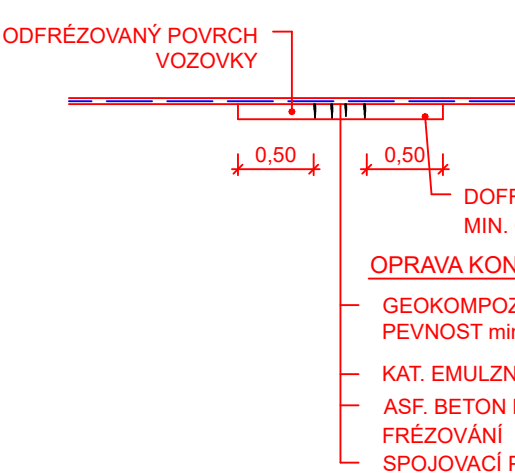


DETAIL C - SPÁRY MEZI ASF. VOZOVKOU
A BETONOVÝM (KAMENNÝM) PRVKEM

M 1:25

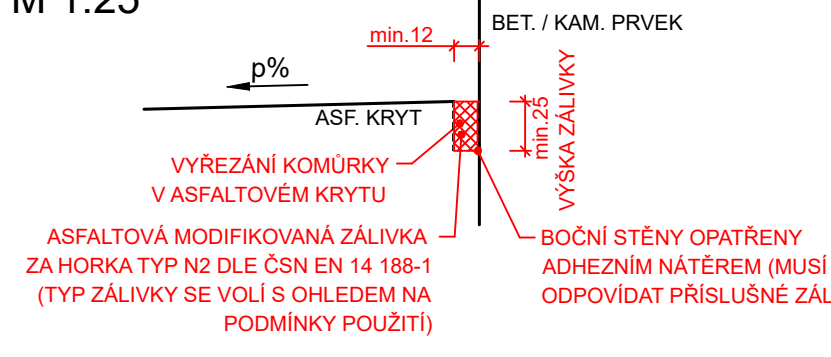


SO 101 - SILNICE II/603
≈ MS2 -/8/50 ODVOZENÁ
BUS (KM 1,825 00)

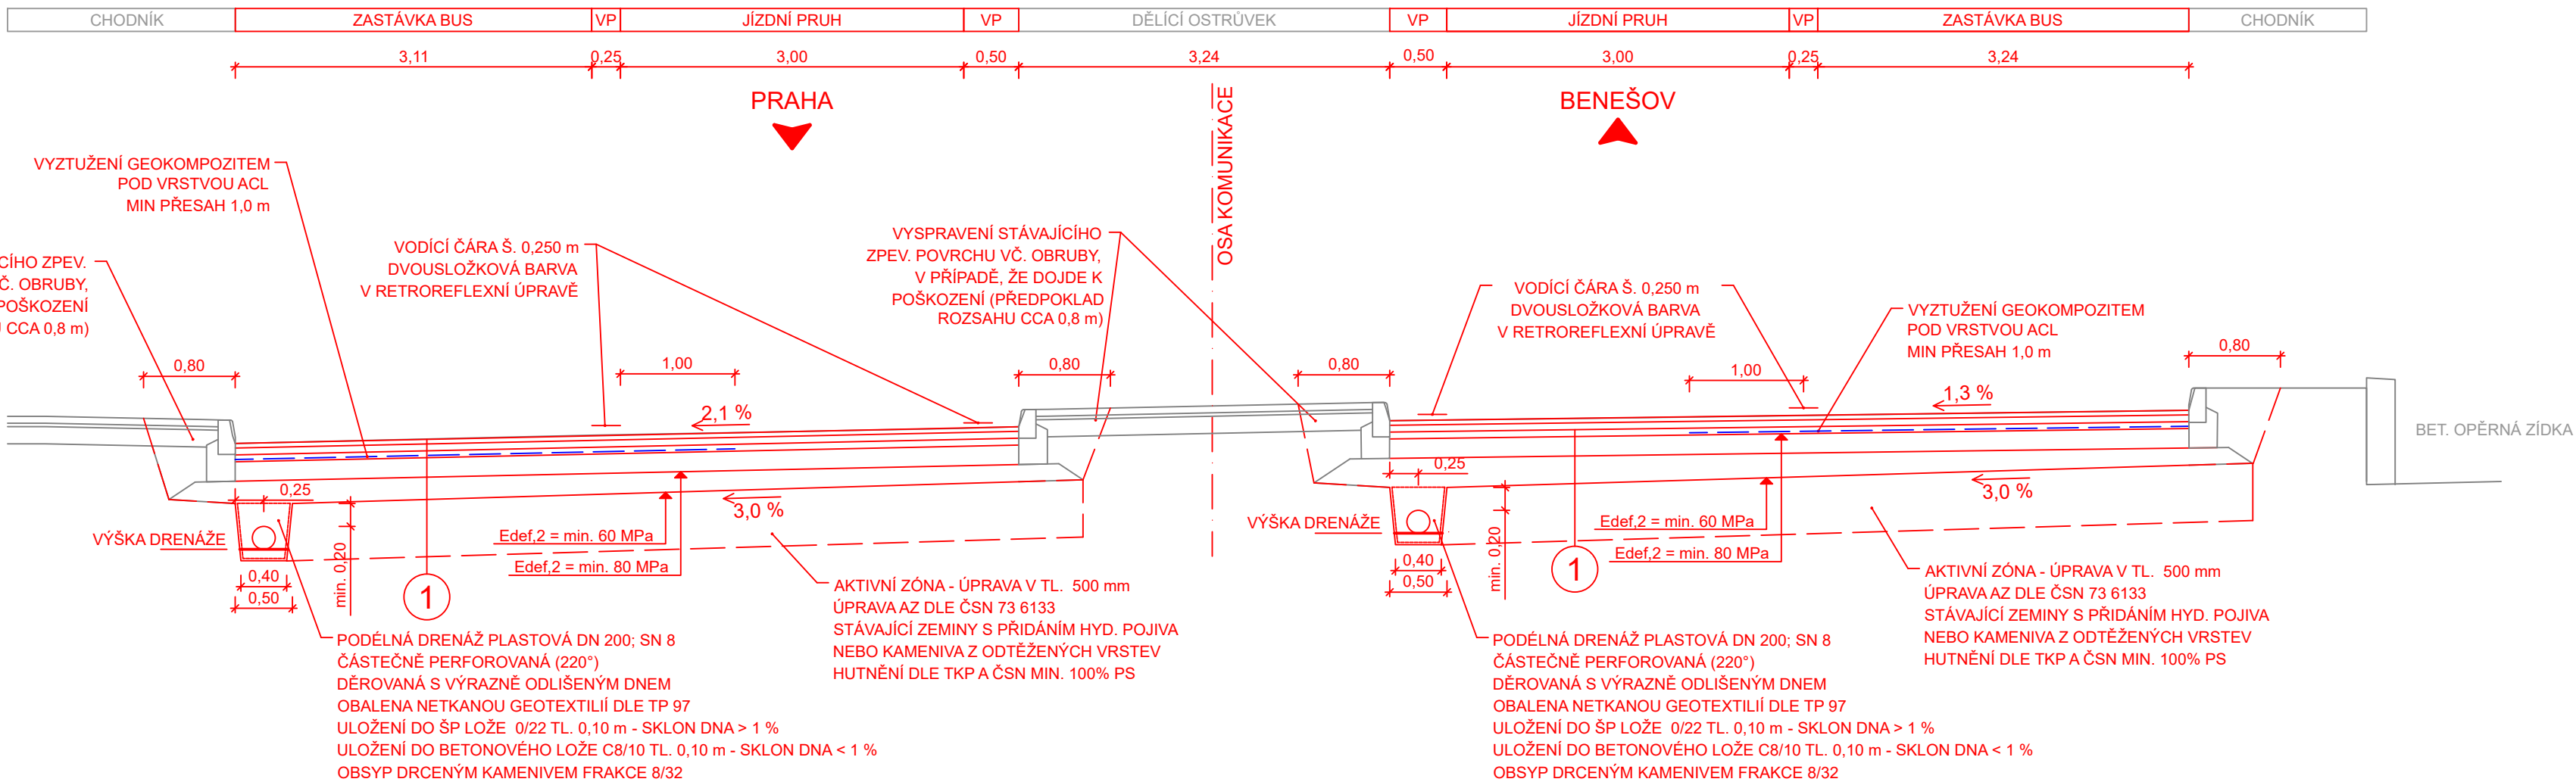


SO 101 - SILNICE II/603
≈ MS2 -/8/50 ODVOZENÁ
(KM 2,000)

ZVÝŠENÝ POČET JÍZDNÍCH PRUHŮ VE STOUPÁNÍ

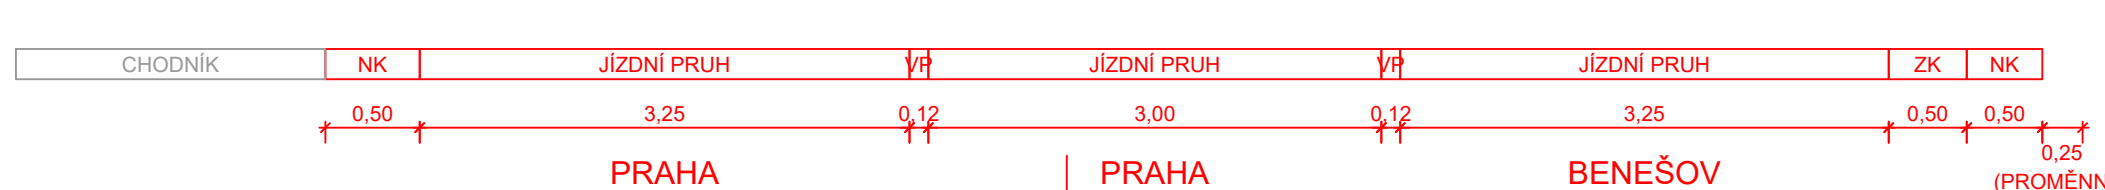

SO 101 - SILNICE II/603
≈ MS2 -/8/50 ODVOZENÁ
(KM 2,460-3,030)

ŠIRŠÍ ZPEVNĚNÁ KRAJNICE A PODÉLNÁ DRENÁŽ

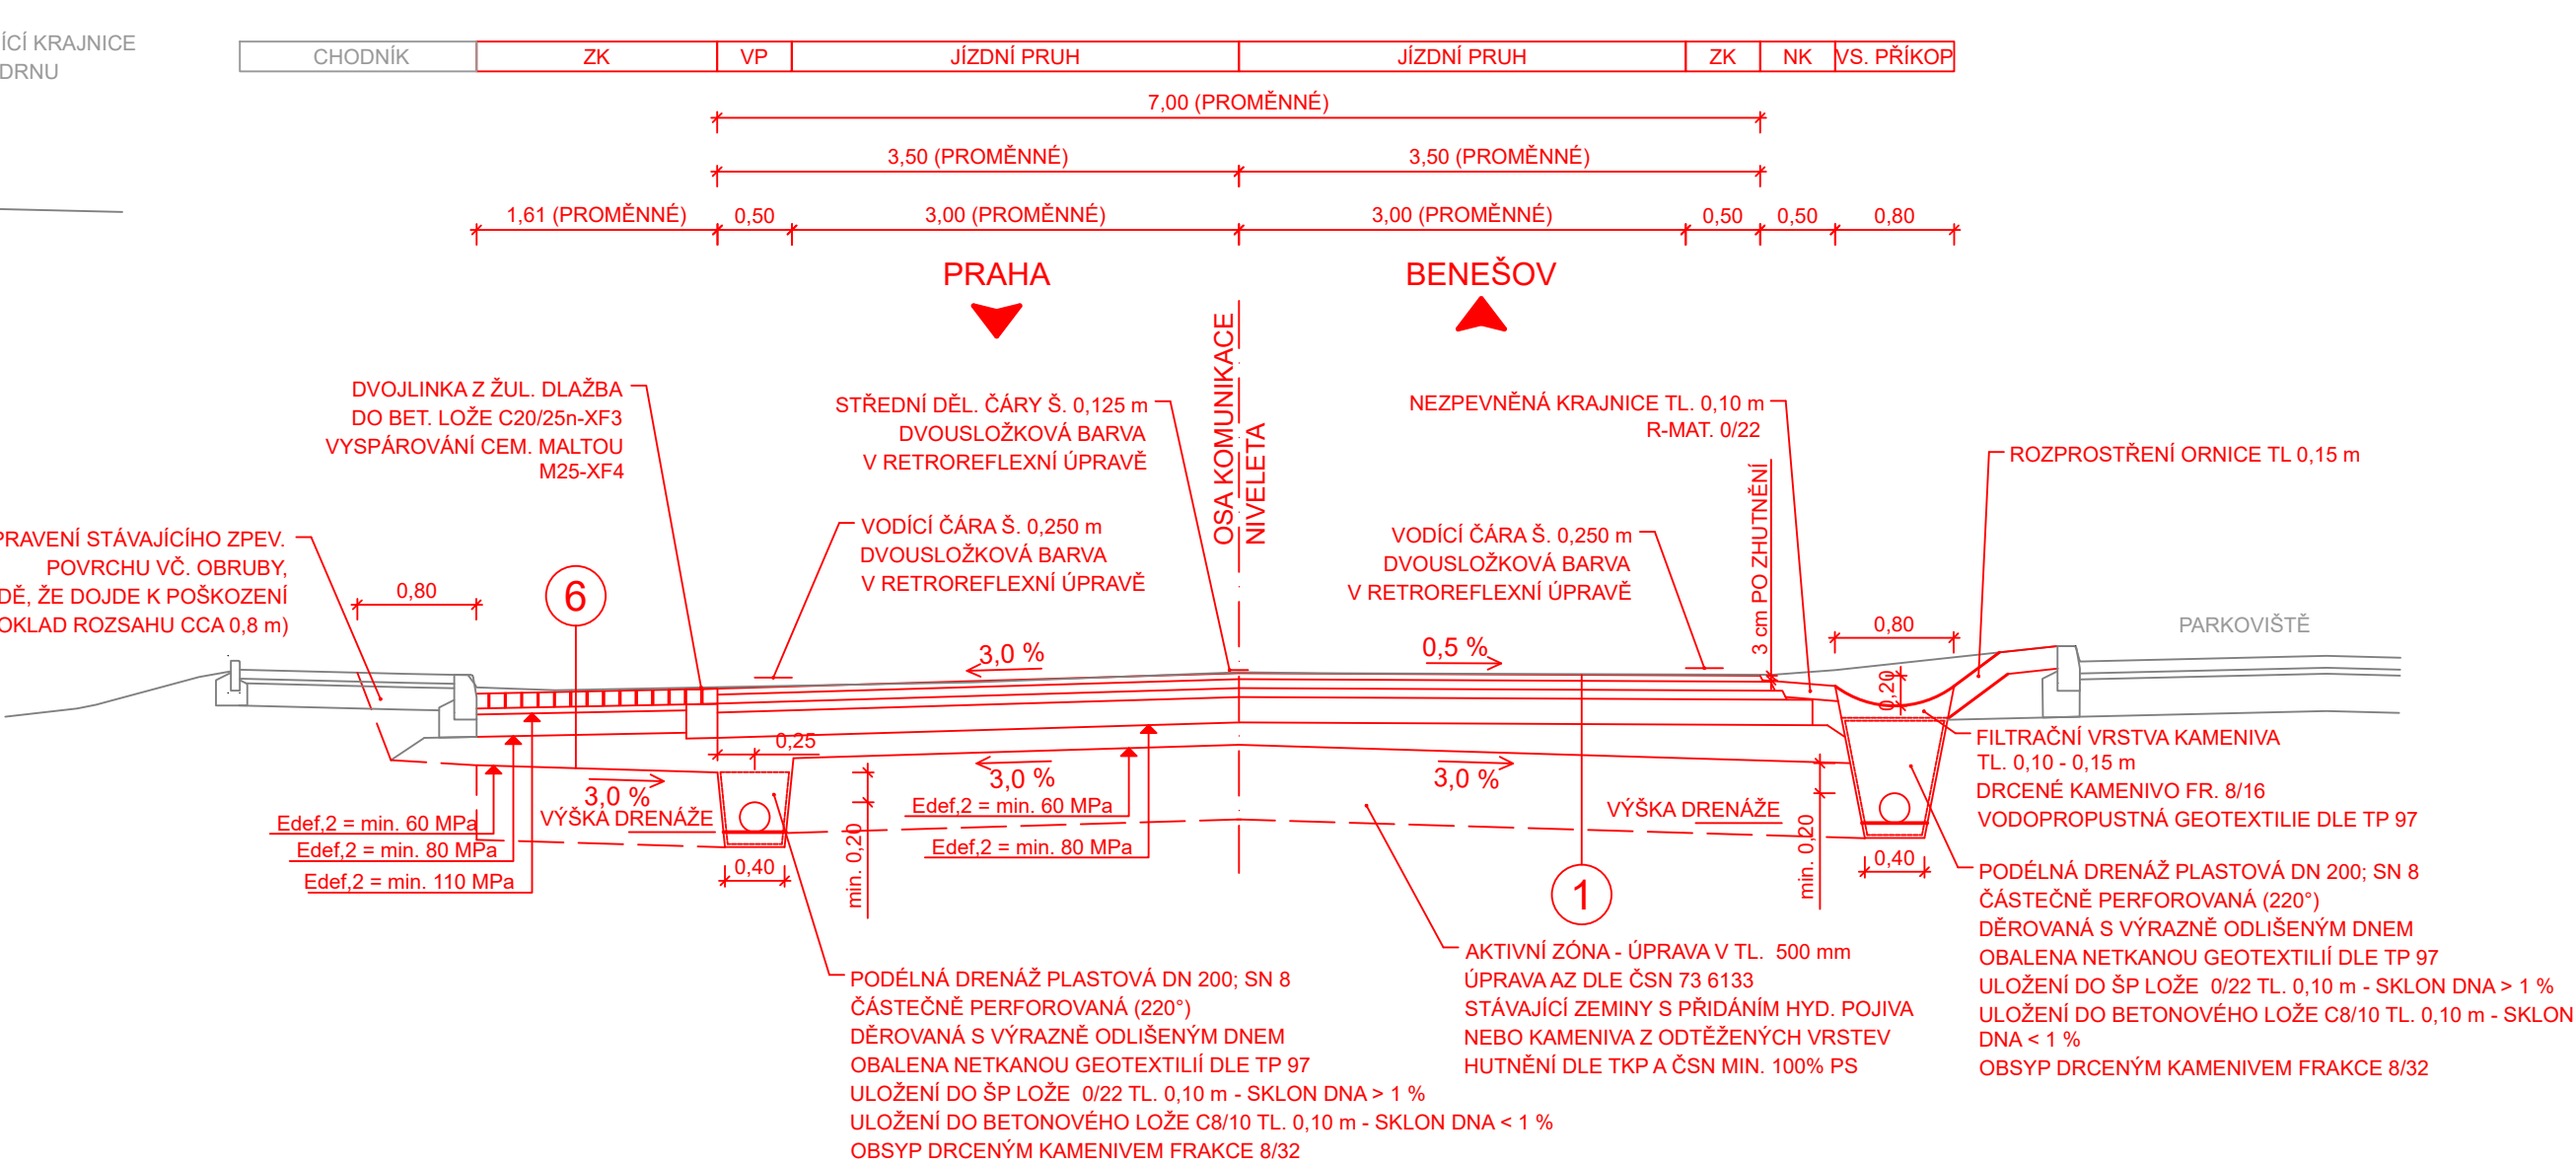

3 SKLADBA KONSTRUKCE Č. 3

ASF. BETON OBRUSNÝ MODIF.	ACO 11+ PMB 45/80-65	40 mm	ČSN 73 6121
VYZTUŽENÍ POVRCHU VOZOVKY SKLOVLÁKNITÝM GEOKOMPOZITEM V CELE ŠÍŘI	PS-CP	0,40 kg/m ²	ČSN 73 6129
SPOJOVACÍ POSTŘÍK MOD. ASF. EMULZÍ	ACP 16 S 50/70	50 mm	ČSN 73 6121
LOKÁLNÍ SANACE V PŘÍPADĚ TRHLIN	PS-C	0,30 kg/m	ČSN 73 6129
SPOJOVACÍ POSTŘÍK	PS-C	min. 40 mm	
KONSTRUKCE CELKEM			
FRÉZOVÁNÍ OBRUSNÉ VRSTVY			
NÁVÝŠENÍ NIVELETY			

1 SKLADBA KONSTRUKCE Č. 1

ASF. BETON OBRUSNÝ MODIF.	ACO 11+ PMB 45/80-65	40 mm	ČSN 73 6121
SPOJOVACÍ POSTŘÍK MODIF.	PS-CP	0,40 kg/m ²	ČSN 73 6129
ASF. BETON LŮŽNÍ MODIF.	ACL 22S PMB 25/55-65	60 mm	ČSN 73 6121
SPOJOVACÍ POSTŘÍK MODIF.	PS-CP	0,40 kg/m ²	ČSN 73 6129
VYROVNÁVACÍ VRSTVA	ACP 16S 50/70	60 mm	ČSN 73 6121
RECYKLACE	RS CA 0/32 (045)	170 mm	ČSN 736147
ŠTERKODŘŤ	ŠDa 0/32 GE	150 mm	ČSN 736126-1
KONSTRUKCE CELKEM		480 mm	
FRÉZOVÁNÍ		-100 mm	
NÁVÝŠENÍ NIVELETY			

6 SKLADBA KONSTRUKCE Č. 3

KAMENNÁ DLAŽBA POJIZDOVÁ	DL	100 mm	ČSN 73 6131
LOŽE (DRBNÉ DRČENÉ KAMENIVO 4-8 MM)	L 4/8	40 mm	ČSN 73 6131
ŠTERKODŘŤ	ŠDa 0/32 GE	150 mm	ČSN 73 6126-1
KONSTRUKCE CELKEM	ŠDa 0/32 GE	190 mm	ČSN 73 6126-1

POZNÁMKY:

- NA AUTOBUSOVÝCH ZASTÁVKÁCH, V PROSTORU AUTOBUSOVÝCH ZÁLIVŮ BUDE NÁVÝŠENÍ NIVELETY KONSTRUKCE VOZOVKY MAXIMÁLNĚ DO 30 MM A KOMUNIKACE BUDE VYZTUŽENA GEOKOMPOZITEM POD VRSTVOU ACL S MINIMÁLNÍM PŘESAHEM 1,0 m. DLE TP 147
- AKTIVNÍ ZÓNA JE NAVRŽENA Z UPRAVĚNÝCH ZEMIN V PODLOŽÍ - PŘEDPOKLAD VYUŽITÍ STÁVAJÍCÍ KONSTRUKCE S PŘIDÁNÍM HYDRAULICKÉHO POJIVA NA TLOUŠKU 500 mm (ZÁVISÍ NA VLASTNOSTECH AKTIVNÍ ZÓNY) NEBO VÝMĚNA PODLOŽÍ S VYUŽITÍM STÁVAJÍCÍCH ODTĚŽENÝCH VRSTEV S PAU A ULOŽENÍM TECHNOLOGIE RECYKLACE ZA STUDENA. JEDNÁ SE O STÁVAJÍCÍ ZEMINŮV PODMÍNEČNĚ VHODNÉ, KTERÉ JE MOŽNO POUŽÍVAT DLE TP 170 PŘI HOODNĚ CBR < 15% ZA TYP PII PŘI OPTIMÁLNÍCH PODMÍNKÁCH VLHKOSTI NEBO ÚPRAVOU ZEMIN AZ S HYDRAULICKÝM POJIVEM MIN. PII A PŘI DOSAŽENÍ VYŠŠÍHO CBR 30% ZA TYP PI
- PŘED POKLÁDKOU VOZOVKOVÝCH VRSTEV JE NUTNÉ OVĚRIT DOSAŽENÍ POŽADOVANÉ HOODNOTY Ed_{af}2, ZEJMÉNA NA PLÁNI
- DOKONČENÁ ZEMNÍ PLÁŇ MUSÍ BÝT CHRÁNĚNA PŘED NEPŘÍZNIVÝMI KLIMATICKÝMI VLIVY. POKUD NEDODJE, ZEJMÉNA PŘED ZIMNÍM OBDOBÍM, K ZAKRYTÍ PLÁNE STMELENOU VRSTVOU KONSTRUKCE VOZOVKY, BUDE V NÁSLEDUJÍCÍ SEZONĚ NUTNĚ ODPSTRANIT NARUŠENOU VRSTVOU A PLÁŇ MATERIÁLEM DO PŘEDPISANÉHO VÝŠKOVÉHO VEDENÍ, NA PLÁNI BUDE TŘEBA PROVĚST OPĚTOVNĚ VŠECHNY POŽADOVANÉ ZKOUSKY
- ODTĚŽENÉ VRSTVY VOZOVEK S OBSAHEM PAU LZE POUŽÍT V SOULADU S VYHLÁŠKOU 283/2023 SB. DO AKTIVNÍ ZÓNY, POKUD BUDOU ULOŽENY DLE ČSN 73 6147 RECYKLACE KONSTRUKČNÍCH VRSTEV VOZOVEK ZA STUDENA.
- PŘED SAMOTNOU REALIZACÍ JE NUTNĚ VHODNOST ZPĚTNÉHO POUŽITÍ VYTĚŽENÝCH MATERIÁLŮ OVĚRIT ODPověDNÝM GEOTECHNIKEM
- NA STYKU ASFALTOBETONOVÉ VOZOVKY S BETONOVÝMI NEBO KAMENNÝMI PRVKY BUDE PRORÁZNUTA SPÁRA (MIN. 25x12 mm) A ZALITA ZÁLIVKOU ZA HORKA DLE ČSN EN 14188-1:
 - TYP N1 U NEPOJIZDĚNÝCH PLOCH
 - TYP N2 U POJIZDĚNÝCH PLOCH
- ZÁLIVKA NA STYKU S MODIFIKOVANÝMI ASFALTY SE PROVEDE TAKÉ MODIFIKOVANÁ
- BETONOVÉ VÝROBKÝ BUDOU Z MATERIÁLU ODOLÁVÁJÍCÍMU PROSTŘEDÍ XF4

REVIZE: PŘEDMĚT ZMĚNY: DATUM: VYPRACOVAL:

a			
b			
c			

NÁZEV STAVBY:	II/603 SULICE - ŽELIVEC, REK. SILNICE A MOSTŮ	ČÍSLO OBJEKTU:	SO 101
---------------	---	----------------	--------

INVESTOR STAVBY č.1:	KRAJSKÁ SPRÁVA A ÚDRŽBA SILNIC STŘEDOČESKÉHO KRAJE p.o. Zborovská 81/11, 150 21 Praha 5	RAŽITKO:	
		DATUM:	PODPIS:

INVESTOR STAVBY č.2:	OBEC KAMENICE Ringhoferovo náměstí 434 Olešovice, 251 68 Kamenice	RAŽITKO:	
		DATUM:	PODPIS:

TECHNICKÝ DOZOR INVESTORA	REALSTAV MB, s.r.o. Klaudianova 124, 293 01 Mladá Boleslav	RAŽITKO:	
		KONTROLOVAL:	
		DATUM:	PODPIS:

ZHOTOVITEL STAVBY:	M - SILNICE, a.s. Husova 1697, Bile Předměstí, 530 03 Pardubice	RAŽITKO:	
		KONTROLOVAL:	
		DATUM:	PODPIS:

KOORDINÁTOR RDS:	M - PROJEKCE, s.r.o. Reslsova 956/13, 500 02 Hradec Králové	RAŽITKO:	
		KONTROLOVAL:	
		DATUM:	PODPIS:

SOURADNICOVÝ SYSTÉM: S-JTSK
VÝŠKOVÝ SYSTÉM: B.P.V.

ETAPA 1+2 (KM 0,000-2,880)

ČISTOPIS

NÁZEV STAVBY:	II/603 SULICE - ŽELIVEC, REKONSTRUKCE SILNICE A MOSTŮ				
ČÁST / STAVEBNÍ OBJEKT:	SO 101 - SILNICE II/603 ÚSEK 1 - INTRAVILÁN				
PŘÍLOHA:	VZOROVÉ PŘÍČNÉ ŘEZY				
ZHOTOVITEL RDS:	HLAVNÍ INŽENÝR PROJEKTU:	Ing. M. STEJSKAL		PARÉ:	
	ZODPOVĚDNÝ PROJEKTANT:	Ing. M. STEJSKAL			
	VYPRACOVAL:	Ing. M. ŠPORNGL			
	KONTROLA:	Ing. M. STEJSKAL			
	MĚŘÍTKO:	Č. ZÁKÁZKY:	STUPEŇ:	DATUM:	ČÁST: PŘÍLOHA:
	1:50	25-118-03	RDS	06/2026	101 4