


SO 101 - CHARAKTERISTICKÉ ŘEZY
M 1:100



REVIZE:	PŘEDMĚT ZMĚNY:	DATUM:	VYPRACOVAL:	
a				
b				
c				
NÁZEV STAVBY: II/603 SULICE - ŽELIVEC, REK. SILNICE A MOSTŮ		ČÍSLO OBJEKTU: SO 101		
INVESTOR STAVBY č.1:  KRAJSKÁ SPRÁVA A ÚDRŽBA SILNIC STŘEDOČESKÉHO KRAJE p.o. Zborovská 81/11, 150 21 Praha 5		RAZÍTKO: DATUM: PODPIS:		
INVESTOR STAVBY č.2:  OBEC KAMENICE Ringhofferovo náměstí 434 Olešovice, 251 68 Kamenice		RAZÍTKO: DATUM: PODPIS:		
TECHNICKÝ DOZOR INVESTORA  REALSTAV MB, s.r.o. Klaudánova 124, 293 01 Mladá Boleslav		RAZÍTKO: KONTROLOVAL: DATUM: PODPIS:		
ZHOVITEL STAVBY:  M - SILNICE, a.s. Husova 1697, Bílé Předměstí, 530 03 Pardubice		RAZÍTKO: KONTROLOVAL: DATUM: PODPIS:		
KOORDINÁTOR RDS:  M - PROJEKCE, s.r.o. Resslova 956/13, 500 02 Hradec Králové		RAZÍTKO: KONTROLOVAL: DATUM: PODPIS:		
SOUŘADNICOVÝ SYSTÉM: S-JTSK VÝŠKOVÝ SYSTÉM: B.P.V.				
ETAPA 1+2 (KM 0,000-2,880)				
ČISTOPIS				
NÁZEV STAVBY: II/603 SULICE - ŽELIVEC, REKONSTRUKCE SILNICE A MOSTŮ				
ČÁST / STAVEBNÍ OBJEKT: SO 101 - SILNICE II/603 ÚSEK 1 - INTRAVILÁN				
PŘÍLOHA: CHARAKTERISTICKÉ PŘÍČNÉ ŘEZY - 2. ČÁST				
ZHOVITEL RDS:  M - PROJEKCE, s.r.o. Resslova 956/13 500 02 Hradec Králové		HLAVNÍ INŽENÝR PROJEKTU: Bc. R. MĚSTECKÝ  ZODPOVĚDNÝ PROJEKTANT: Ing. M. ŠTEJSKAL  VYPRACOVAL: Bc. R. MĚSTECKÝ  KONTROLA: Ing. P. KELČA  MĚŘÍTKO: 1:100 Č. ZAKÁZKY: 25-118-03 STUPEŇ: RDS DATUM: 06/2026 ČÁST: 101 PŘÍLOHA: 5.2		PARÉ: