


SO 101 - CHARAKTERISTICKÉ ŘEZY
M 1:100



REVIZE:	PŘEDMĚT ZMĚNY:	DATUM:	VYPRACOVAL:
a			
b			
c			
NÁZEV STAVBY: II/603 SULICE - ŽELIVEC, REK. SILNICE A MOSTŮ		ČÍSLO OBJEKTU: SO 101	
INVESTOR STAVBY č.1:  KRAJSKÁ SPRÁVA A ÚDRŽBA SILNIC STŘEDOČESKÉHO KRAJE p.o. Zborovská 81/11, 150 21 Praha 5		RAŽITKO: DATUM: PODPIS:	
INVESTOR STAVBY č.2:  OBEC KAMENICE Ringhofferovo náměstí 434 Olešovice, 251 68 Kamenice		RAŽITKO: DATUM: PODPIS:	
TECHNICKÝ DOZOR INVESTORA  REALSTAV MB, s.r.o. Klaudánova 124, 293 01 Mladá Boleslav		RAŽITKO: KONTROLOVAL: DATUM: PODPIS:	
ZHOTOVITEL STAVBY:  M - SILNICE, a.s. Husova 1697, Bílé Předměstí, 530 03 Pardubice		RAŽITKO: KONTROLOVAL: DATUM: PODPIS:	
KOORDINÁTOR RDS:  M - PROJEKCE, s.r.o. Reslova 956/13, 500 02 Hradec Králové		RAŽITKO: KONTROLOVAL: DATUM: PODPIS:	
SOUŘADNICOVÝ SYSTÉM: S-JTSK VÝŠKOVÝ SYSTÉM: B.P.V.		ETAPA 1+2 (KM 0,000-2,880)	
NÁZEV STAVBY: II/603 SULICE - ŽELIVEC, REKONSTRUKCE SILNICE A MOSTŮ		ČISTOPIS	
ČÁST / STAVEBNÍ OBJEKT:		SO 101 - SILNICE II/603 ÚSEK 1 - INTRAVILÁN	
PŘÍLOHA:		CHARAKTERISTICKÉ PŘÍČNÉ ŘEZY - 3. ČÁST	
ZHOTOVITEL RDS:  M - PROJEKCE, s.r.o. Reslova 956/13 500 02 Hradec Králové	HLAVNÍ INŽENÝR PROJEKTU:	Bc. R. MĚSTECKÝ	PARÉ:
	ZODPOVĚDNÝ PROJEKTANT:	Ing. M. STEJSKAL	
	VYPRACOVAL:	Bc. R. MĚSTECKÝ	
	KONTROLA:	Ing. P. KELČA	
MĚŘITKO:		Č. ZAKÁZKY:	STUPEŇ:
1:100		25-118-03	RDS
DATUM:		ČÁST:	PŘÍLOHA:
06/2026		101	5.3