


SO 101 - CHARAKTERISTICKÉ ŘEZY
M 1:100

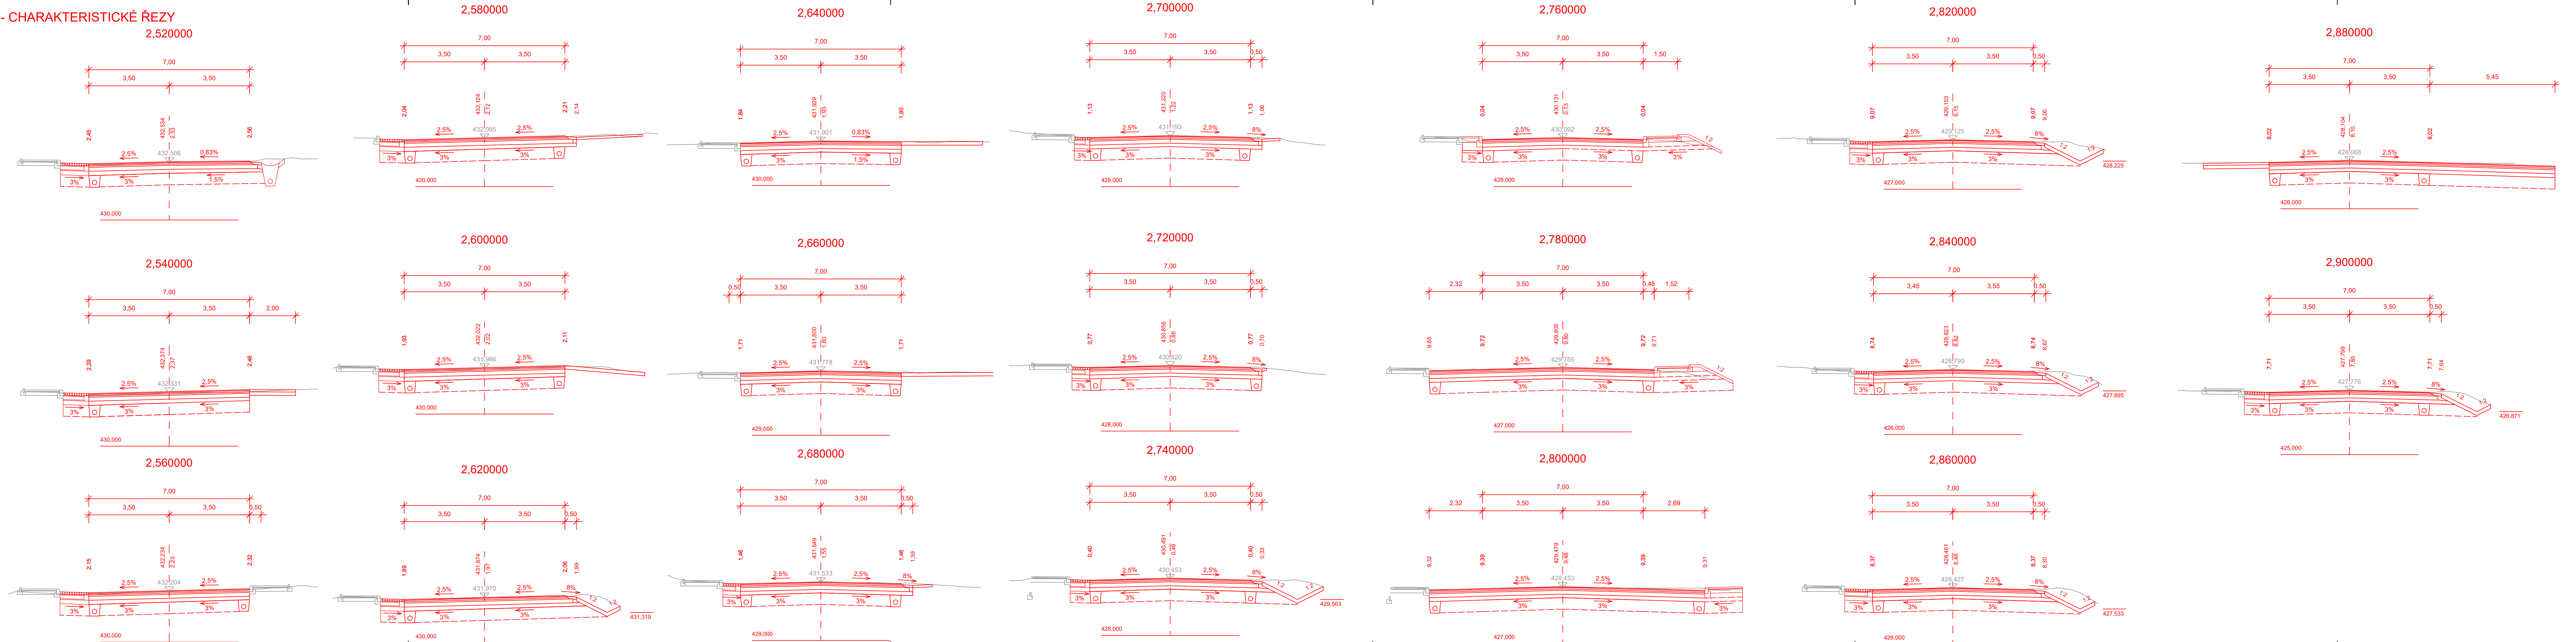

REVIZE:	PŘEDMĚT ZMĚNY:	DATUM:	VYPRACOVAL:			
a						
b						
c						
NÁZEV STAVBY: II/603 SULICE - ŽELIVEC, REK. SILNICE A MOSTŮ		ČÍSLO OBJEKTU: SO 101				
INVESTOR STAVBY č.1:  KRAJSKÁ SPRÁVA A ÚDRŽBA SILNIC STŘEDOČESKÉHO KRAJE p.o. Zborovská 81/11, 150 21 Praha 5		RAŽÍTKO: DATUM: PODPIS:				
INVESTOR STAVBY č.2:  OBEC KAMENICE Ringhofferovo náměstí 434 Olešovice, 251 68 Kamenice		RAŽÍTKO: DATUM: PODPIS:				
TECHNICKÝ DOZOR INVESTORA  REALSTAV MB, s.r.o. Klaudánova 124, 293 01 Mladá Boleslav		RAŽÍTKO: KONTOLOVAL: DATUM: PODPIS:				
ZHOTOVITEL STAVBY:  M - SILNICE, a.s. Husova 1697, Bílé Předměstí, 530 03 Pardubice		RAŽÍTKO: KONTOLOVAL: DATUM: PODPIS:				
KOORDINÁTOR RDS:  M - PROJEKCE, s.r.o. Resslova 956/13, 500 02 Hradec Králové		RAŽÍTKO: KONTOLOVAL: DATUM: PODPIS:				
SOÚŘADNICOVÝ SYSTÉM: S-JTSK VÝŠKOVÝ SYSTÉM: B.P.V.		ETAPA 1+2 (KM 0,000-2,880)				
NÁZEV STAVBY: II/603 SULICE - ŽELIVEC, REKONSTRUKCE SILNICE A MOSTŮ		ČISTOPIS				
ČÁST / STAVEBNÍ OBJEKT: SO 101 - SILNICE II/603 ÚSEK 1 - INTRAVILÁN						
PŘÍLOHA: CHARAKTERISTICKÉ PŘÍČNÉ ŘEZY - 4. ČÁST						
ZHOTOVITEL RDS:  M - PROJEKCE, s.r.o. Resslova 956/13 500 02 Hradec Králové	HLAVNÍ INŽENÝR PROJEKTU:	Bc. R. MĚSTECKÝ		PARÉ:		
	ZODPOVĚDNÝ PROJEKTANT:	Ing. M. STEJSKAL				
	VYPRACOVAL:	Bc. R. MĚSTECKÝ				
	KONTROLA:	Ing. P. KELČA				
	MĚŘÍTKO:	Č. ZAKÁZKY:	STUPEŇ:	DATUM:	ČÁST:	PŘÍLOHA:
	1:100	25-118-03	RDS	06/2026	101	5.4