SO 101 - SITUACE DOPRAVNÍHO ZNAČENÍ
M 1:500

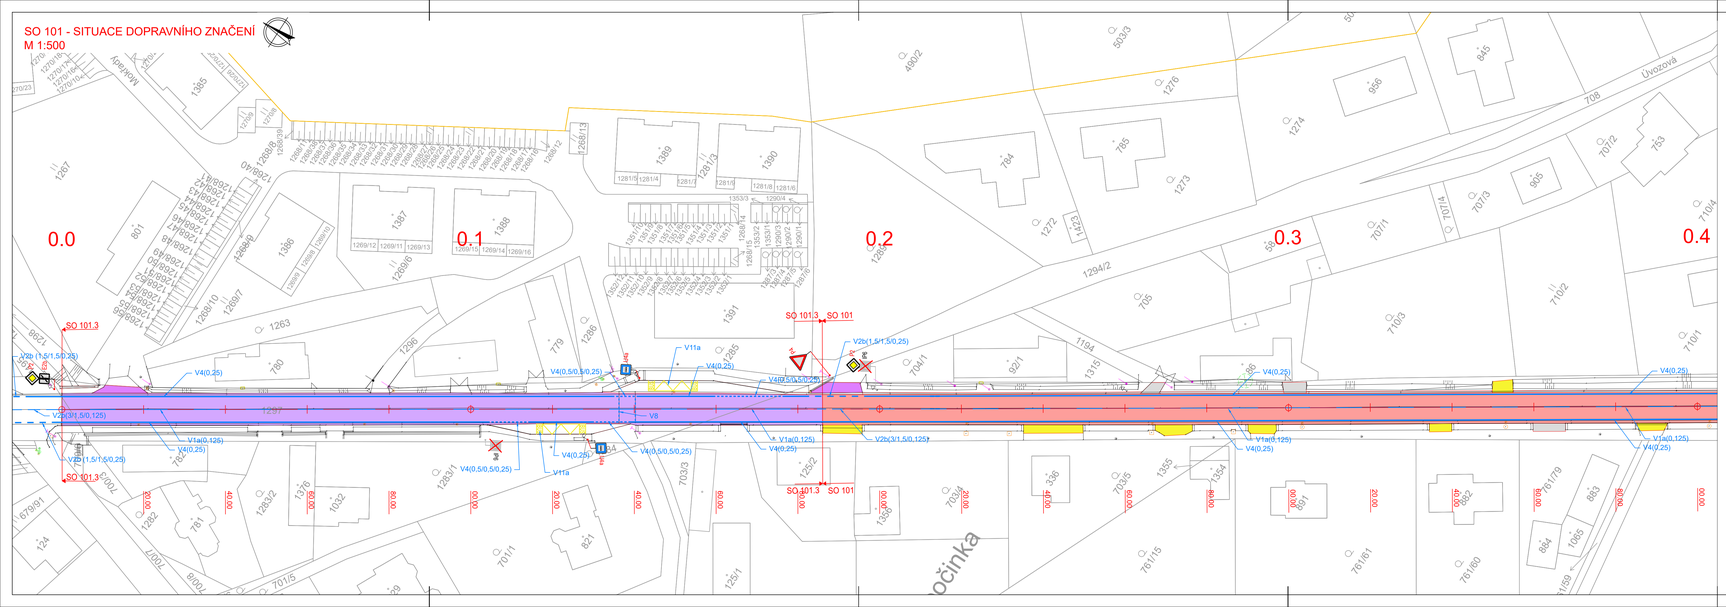

SEZNAM STAVEBNÍCH OBJEKTŮ:

100 - OBJEKTY POZEMNÍCH KOMUNIKACÍ

SO 101 - SLNICE II/603 ÚSEK 1 - INTRAVILÁN
SO 101.1 - SLNICE II/603 ÚSEK 1- INTRAVILÁN CHODNÍK 2,721-2,797
SO 101.2 - OZELENĚNÍ NEZPEVNĚNÉ PLOCHY ULICE RINGHOFFEROVA
SO 101.3 - SLNICE II/603 ÚSEK 1 - INTRAVILÁN - OPRAVA POVRCHU
SO 101.4 - SLNICE II/603 ÚSEK 1 - KOMPLEXNÍ OPRAVA 2,471-2,508
SO 102 - SLNICE II/603 ÚSEK 2 - EXTRAVILÁN
SO 103 - SLNICE II/603 ÚSEK 3 - OKRUŽNÍ KŘIŽOVATKA
SO 104 - SLNICE II/603 ÚSEK 4 - PROPUSTEK 1
SO 105 - SLNICE II/603 ÚSEK 5 - PROPUSTEK 2
SO 106 - SLNICE II/603 ÚSEK 6 - NOVÁ HOSPODA
SO 107 - SLNICE II/603 ÚSEK 7 - ZPOMALOVACÍ OSTROVÉK
SO 161 - DOPRAVNÍ INŽENÝRSKÉ ZAŘÍZENÍ (NENÍ ZOBRAZENO)

300 - VODOHOSPODÁŘSKÉ OBJEKTY

SO 331 - OCHRANA I OPRAVA KANALIZACE V ÚSEKU 1
SO 334 - OCHRANA I OPRAVA KANALIZACE V ÚSEKU 4
SO 335 - OCHRANA I OPRAVA KANALIZACE V ÚSEKU 5
SO 335.1 - OCHRANA I OPRAVA DEŠŤOVÉ KANALIZACE V ÚSEKU 5
SO 336 - OCHRANA I OPRAVA KANALIZACE V ÚSEKU 6
SO 337 - OCHRANA I OPRAVA KANALIZACE V ÚSEKU 7
SO 341 - OCHRANA I OPRAVA VODOVODU V ÚSEKU 1
SO 343 - OCHRANA I OPRAVA VODOVODU V ÚSEKU 3
SO 344 - OCHRANA I OPRAVA VODOVODU V ÚSEKU 4
SO 345 - OCHRANA I OPRAVA VODOVODU V ÚSEKU 5
SO 346 - OCHRANA I OPRAVA VODOVODU V ÚSEKU 6

400 - ELEKTRO A SDĚLOVACÍ OBJEKTY

SO 413 - PŘÍLOŽKA VEDENÍ VN V ÚSEKU 3
SO 414 - OCHRANA I ÚPRAVA VEDENÍ VN V ÚSEKU 4
SO 432 - OCHRANA I ÚPRAVA KABELU VN A NN V ÚSEKU 1 A 2
SO 434 - OCHRANA I ÚPRAVA VEDENÍ NN V ÚSEKU 4
SO 435 - OCHRANA I ÚPRAVA VEDENÍ NN V ÚSEKU 5
SO 437 - OCHRANA I ÚPRAVA VEDENÍ NN V ÚSEKU 7
SO 441 - DOPLNĚNÍ A ÚPRAVA VO V ÚSEKU 1, KM 2,756
SO 443 - DOPLNĚNÍ A ÚPRAVA VO V ÚSEKU 3 - OK
SO 444 - OCHRANA I ÚPRAVA KABELŮ VO V ÚSEKU 4
SO 445 - OCHRANA I ÚPRAVA KABELŮ VO V ÚSEKU 5
SO 446 - OCHRANA I ÚPRAVA KABELŮ VO V ÚSEKU 6
SO 447 - DOPLNĚNÍ A ÚPRAVA VO V ÚSEKU 7 - ZPOMALOVACÍ OSTROVÉK
SO 482 - OCHRANA I ÚPRAVA SDĚLOVACÍCH KABELŮ V ÚSEKU 1 A 2
SO 483 - OCHRANA I ÚPRAVA SDĚLOVACÍCH KABELŮ V ÚSEKU 3
SO 484 - OCHRANA I ÚPRAVA SDĚLOVACÍCH KABELŮ V ÚSEKU 4
SO 485 - OCHRANA I ÚPRAVA SDĚLOVACÍCH KABELŮ V ÚSEKU 5
SO 487 - OCHRANA I ÚPRAVA SDĚLOVACÍCH KABELŮ V ÚSEKU 7

500 - OBJEKTY TRUBNÍCH VEDENÍ

SO 515 - OCHRANA I ÚPRAVA VLT PLYNOVODU V ÚSEKU 5
SO 521 - OCHRANA I ÚPRAVA STL PLYNOVODU V ÚSEKU 1
SO 524 - OCHRANA I ÚPRAVA STL PLYNOVODU V ÚSEKU 4
SO 525 - OCHRANA I ÚPRAVA STL PLYNOVODU V ÚSEKU 5
SO 526 - OCHRANA I ÚPRAVA STL PLYNOVODU V ÚSEKU 6
SO 527 - OCHRANA I ÚPRAVA STL PLYNOVODU V ÚSEKU 7

LEGENDA:

ČÁRY A HRANY

- HRANY KOMUNIKACE
- OSA KOMUNIKACE
- SOUVISEJÍCÍ STAVBA
- ZAMĚŘENÍ STÁVAJÍCÍHO STAVU
- KATASTRÁLNÍ MAPA
- DRNÁŽ
- 553/5
- NOVÉ SVISLÉ DZ
- STÁVAJÍCÍ SVISLÉ DZ
- STÁVAJÍCÍ SVISLÉ DZ - ZRUŠÍ SE
- VODOROVNÉ DOPRAVNÍ ZNAČENÍ

PLOCHY

- PLOCHA KOMUNIKACE - SKLADBA 1 (INTRAVILÁN)
- PLOCHA KOMUNIKACE - SKLADBA 2 (EXTRAVILÁN)
- PLOCHA KOMUNIKACE - SKLADBA 3 (OPRAVA DŮRUSU)
- PLOCHA KOMUNIKACE - SKLADBA 4 (POJEZDNÁ ZLAŽBA OK)
- PLOCHA KOMUNIKACE - SKLADBA 5 (NEPOJEZDNÁ ZLAŽBA CHODNÍKY)
- PLOCHA KOMUNIKACE - SKLADBA 6 (POJEZDNÁ ZLAŽBA)
- OBNOVA NAPOJENÍ SJEZDU (ŠTĚRK)
- OBNOVA NAPOJENÍ SJEZDU (ZLAŽBA POJEZDNÁ)
- OBNOVA NAPOJENÍ SJEZDU (ASFALT)
- NEZPEVNĚNÁ KRAJNICE
- ZPEVNĚNÍ POVRCHU S ODVODŇOVACÍ FUNKCÍ
- OZELENĚNÁ, NEZPEVNĚNÁ PLOCHA, TERÉNNÍ ÚPRAVY

REVIZE:	PŘEDMĚT ZMĚNY:	DATUM:	VYPRACOVAL:
a			
b			
c			

NÁZEV STAVBY:
II/603 SULICE - ŽELIVEC, REK. SILNICE A MOSTŮ

ČÍSLO OBJEKTU:
SO 101

INVESTOR STAVBY č.1:
KRAJSKÁ SPRÁVA a ÚDRŽBA SILNIC STŘEDOČESKÉHO KRAJE p.o.
Zborovská 81/11, 150 21 Praha 5

RAZÍTKO:
DATUM: PODPIS:

INVESTOR STAVBY č.2:
OBEC KAMENICE
Ringhofferovo náměstí 434
Oleškovice, 251 68 Kamenice

RAZÍTKO:
DATUM: PODPIS:

TECHNICKÝ DOZOR INVESTORA
REALSTAV MB, s.r.o.
Klaudiánova 124, 293 01 Mladá Boleslav

RAZÍTKO:
KONTROLOVAL:
DATUM: PODPIS:

ZHOTOVITEL STAVBY:
M - SILNICE, a.s.
Husova 1697, Bílé Předměstí, 530 03 Pardubice

RAZÍTKO:
KONTROLOVAL:
DATUM: PODPIS:

KOORDINÁTOR RDS:
M - PROJEKCE, s.r.o.
Resslova 958/13, 500 02 Hradec Králové

RAZÍTKO:
KONTROLOVAL:
DATUM: PODPIS:

SOUŘADNICOVÝ SYSTÉM: S-JTSK
VÝŠKOVÝ SYSTÉM: B.P.V.

ETAPA 1+2 (KM 0,000-2,880)

ČISTOPIS

NÁZEV STAVBY:
II/603 SULICE - ŽELIVEC, REKONSTRUKCE SILNICE A MOSTŮ

ČÁST / STAVEBNÍ OBJEKT:
SO 101 - SILNICE II/603 ÚSEK 1 - INTRAVILÁN

PŘÍLOHA:
SITUACE DOPRAVNÍHO ZNAČENÍ (KM 0,000 - 0,400)

ZHOTOVITEL RDS:
M - PROJEKCE, s.r.o.
Resslova 958/13
500 02 Hradec Králové

		PARÉ:
HLAVNÍ INŽENÝR PROJEKTU:	Bc. R. MĚSTECKÝ	
ZODPOVĚDNÝ PROJEKTANT:	Ing. M. STEJSKAL	
VYPRACOVAL:	Ing. M. ŠPRONGL	
KONTROLA:	Ing. P. KELČA	

MĚŘÍTKO:	Č. ZAKÁZKY:	STUPEŇ:	DATUM:	ČÁST:	PŘÍLOHA:
1:500	25-118-03	RDS	06/2026	101	6.1