


SO 102 - VZOROVÉ PŘÍČNÉ ŘEZY
M 1:50


SO 102 - Silnice II/603 - extravilán
≈ S7,5/50 odvozená
(Skladba č.2) (km 1,000)
Souběh s pravostranným chodníkem

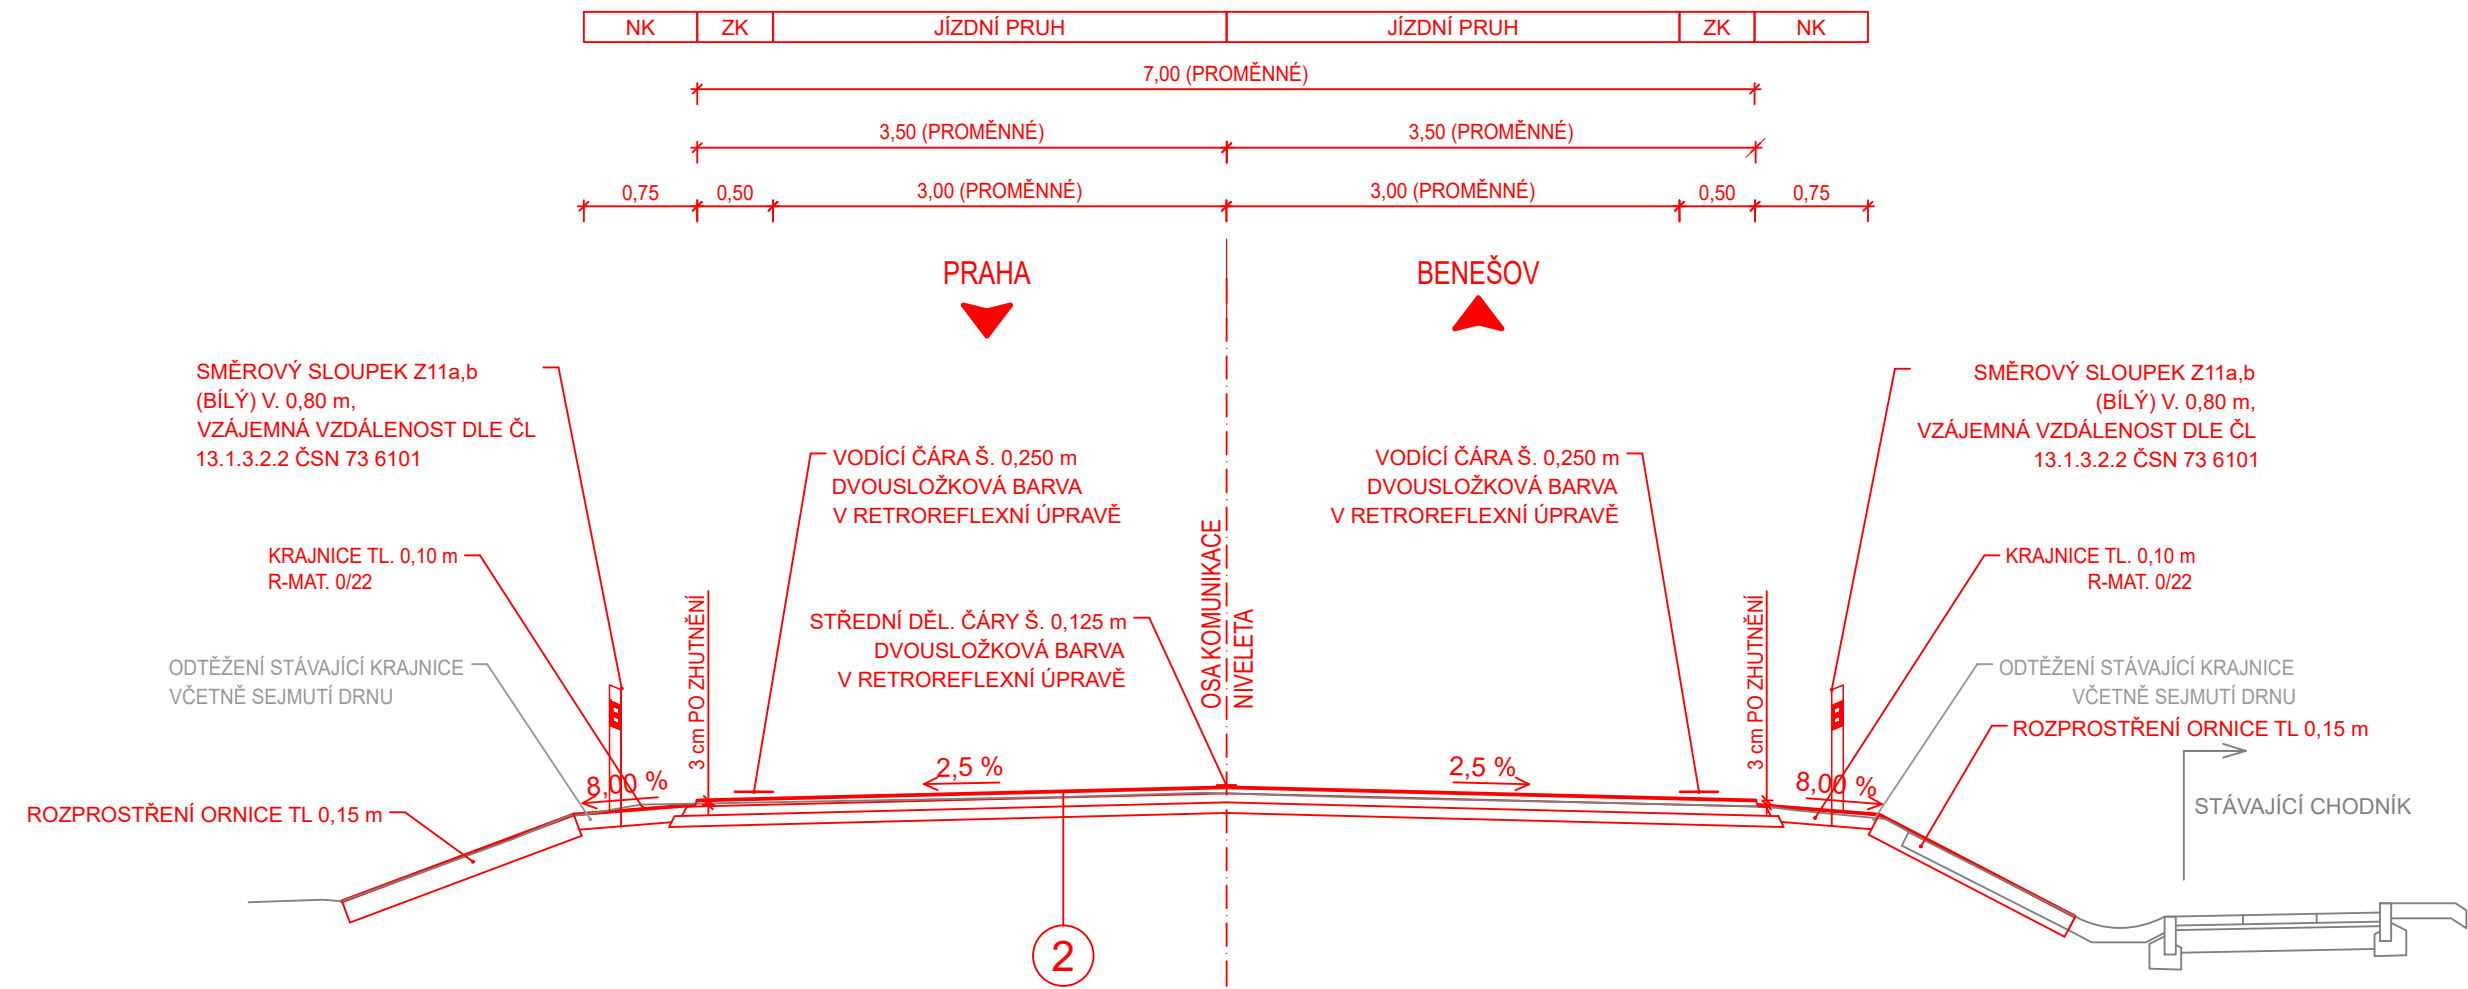

2 SKLADBA KONSTRUKCE Č. 2			
ASF. BETON OBRUSNÝ MODIF.	ACO 11+ PMB 45/80-65	40 mm	ČSN 73 6121
SPOJOVACÍ POSTŘÍK MODIF.	PS-CP	0,40 kg/m ²	ČSN 73 6129
ASF. BETON LOŽNÍ MODIF.	ACL 16S PMB 25/55-65	60 mm	ČSN 73 6121
SPOJOVACÍ POSTŘÍK MODIF.	PS-CP	0,40 kg/m ²	ČSN 73 6129
ASF. BETON PODKLADNÍ	ACP 22S 50/70	70 mm	ČSN 73 6121
SPOJOVACÍ POSTŘÍK	PI C	0,60 kg/m ²	ČSN 73 6129
VYSTUŽENÍ POVRCHU VOZOVKY SKLOVLÁKNITÝM GEOKOMPOZITEM (min. šířka 1,5 m)			
KONSTRUKCE CELKEM		170 mm	
FRÉZOVÁNÍ		-140 mm	
NAVÝŠENÍ NIVELETY		±30 mm	

- POZNÁMKY:
- POSTŘÍKY JSOU UVEDENY V MNOŽSTVÍ ZBYTKOVÉHO POJIVA.
 - V MÍSTECH KDE BUDOU PŘI PROHLÍDKĚ VYFRÉZOVANÉHO POVRCHU ČI SANACÍCH ZAZNAMENÁNY KONSTRUČNÍ PORUCHY VOZOVKY, NEDOSTATEČNÁ ZBYTKOVÁ KONSTRUKCE BUDE SE SOUHLASEM TDI PROVEDENA HLOUBKOVÁ SANACE. PŘEDPOKLÁDANÁ SANACE PODKLADNÍCH VRSTEV: SC (3/4) 150 mm, ŠDa 150 mm. V PŘÍPADĚ NEDOSTATEČNÉ ÚNOSNOSTI PODLOŽÍ (min Edef2 = 45 MPa) BUDE PROVEDENO ZLEPŠENÍ AZ

SO 102 - Silnice II/603 - extravilán
≈ S7,5/50 odvozená
(Skladba č.2) (km 1,400)
Souběh s levostranným chodníkem

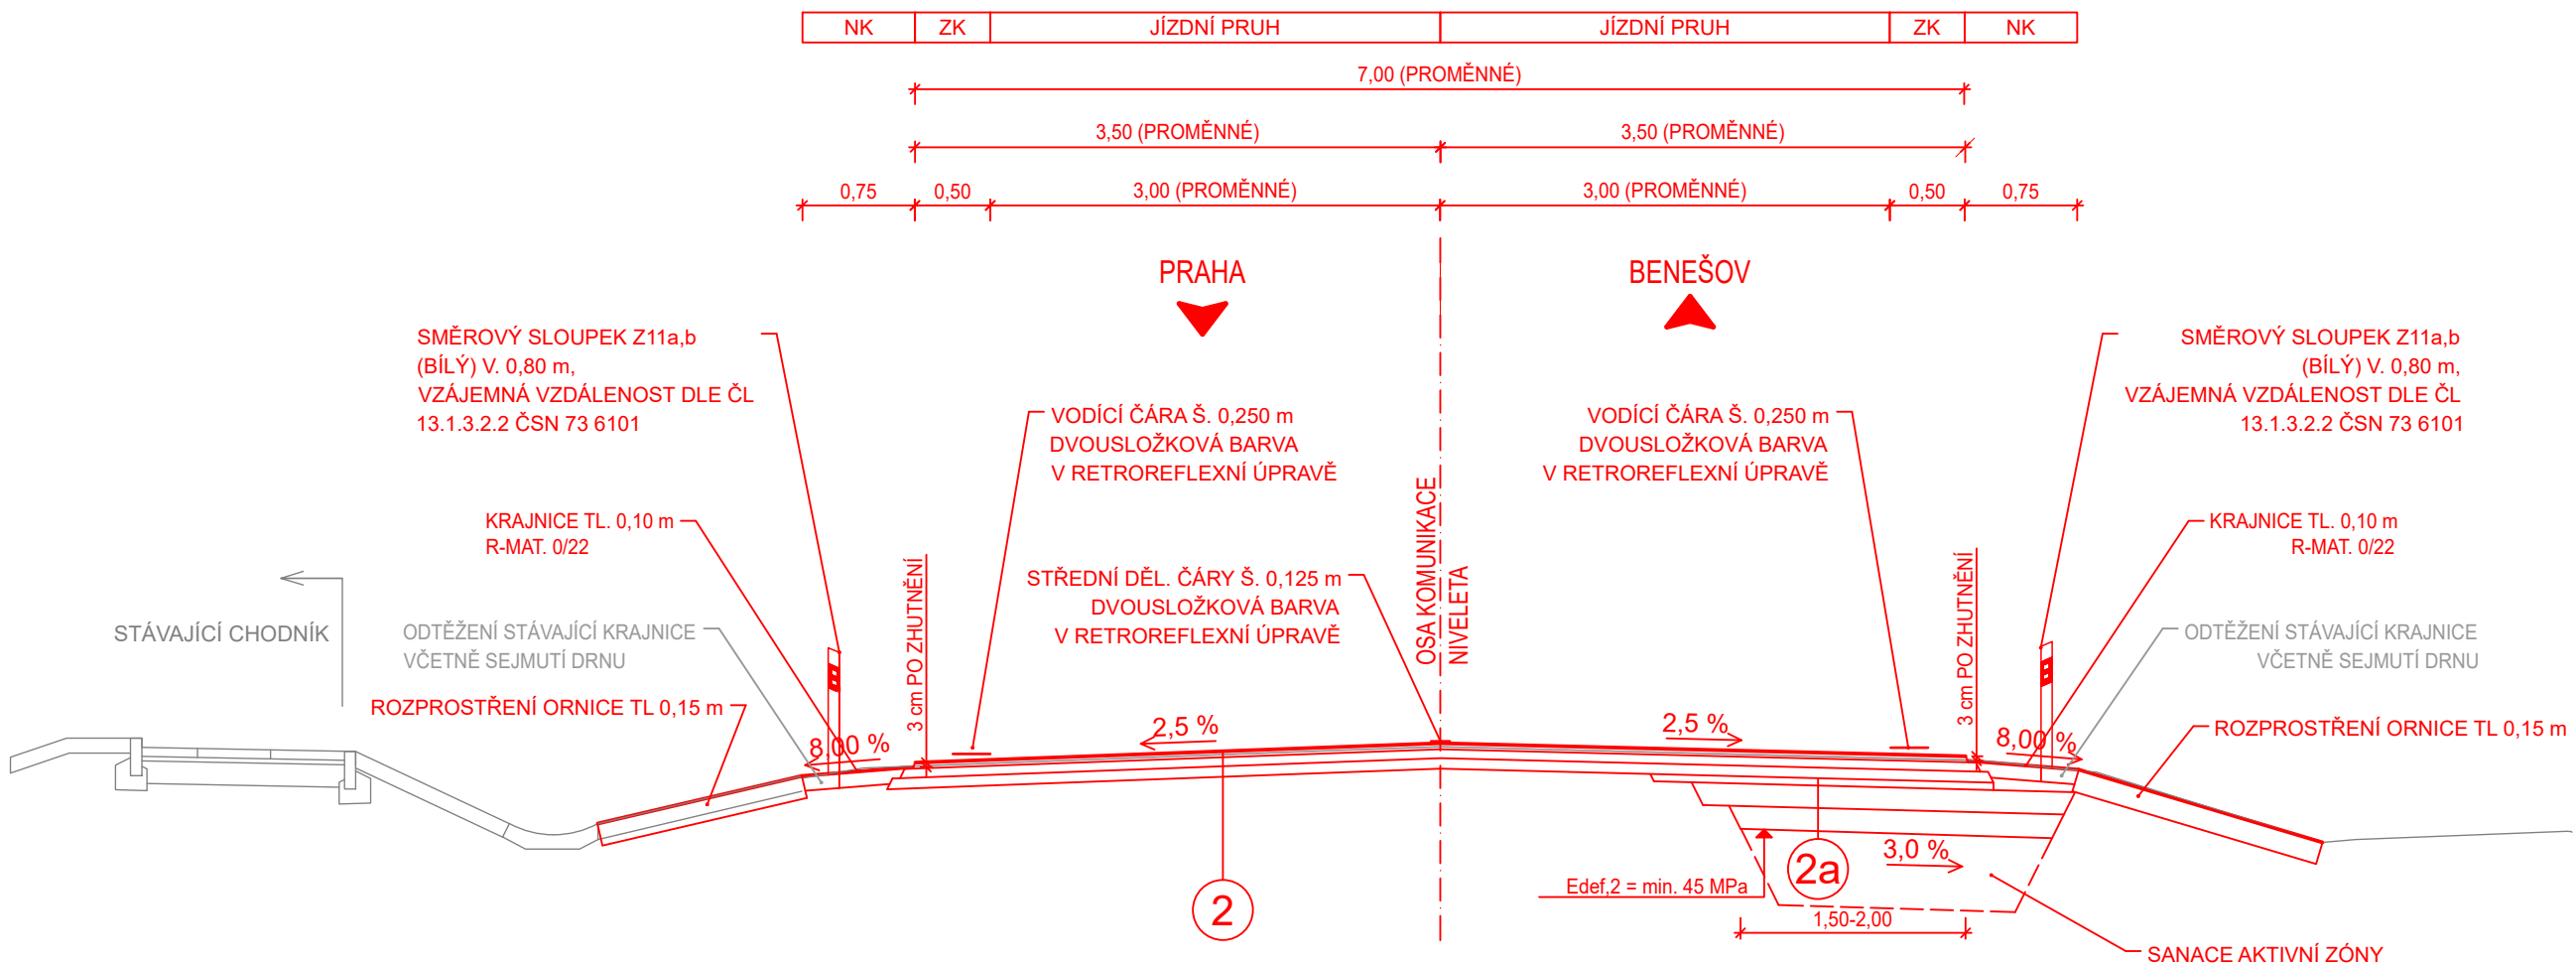

2 SANACE KRAJŮ VOZOVKY: UVAŽOVÁNO 10-15% Z CELKOVÉ PLOCHY			
ASF. BETON PODKLADNÍ	ACP 16S 50/70	50 mm	ČSN 73 6121
SMĚS Z KAM. STMELENÉ CEMENTEM	SC C3/4	150 mm	ČSN EN 14227-1
ŠTĚRKODŘT 0/63	ŠDa 0/63	150 mm	ČSN EN 13285
KONSTRUKCE CELKEM		350 mm	
FRÉZOVÁNÍ		-50 mm	

REVIZE:	PŘEDMĚT ZMĚNY:	DATUM:	VYPRACOVAL:
a			
b			
c			

NÁZEV STAVBY: II/603 SULICE - ŽELIVEC, REK. SILNICE A MOSTŮ	ČÍSLO OBJEKTU: SO 102
--	--------------------------

INVESTOR STAVBY č.1:  KRAJSKÁ SPRÁVA A ÚDRŽBA SILNIC STŘEDOČESKÉHO KRAJE p.o. Zborovská 81/11, 150 21 Praha 5	RAZÍTKO: DATUM: PODPIS:
---	-----------------------------------

INVESTOR STAVBY č.2:  OBEC KAMENICE Ringhofferovo náměstí 434 Olešovice, 251 68 Kamenice	RAZÍTKO: DATUM: PODPIS:
--	-----------------------------------

TECHNICKÝ DOZOR INVESTORA  REALSTAV MB, s.r.o. Klaudánova 124, 293 01 Mladá Boleslav	RAZÍTKO: KONTROLOVAL: DATUM: PODPIS:
---	---

ZHOTOVITEL STAVBY:  M - SILNICE, a.s. Husova 1697, Bílé Předměstí, 530 03 Pardubice	RAZÍTKO: KONTROLOVAL: DATUM: PODPIS:
--	---


KOORDINÁTOR RDS:  M - PROJEKCE, s.r.o. Resslova 956/13, 500 02 Hradec Králové	RAZÍTKO: KONTROLOVAL: DATUM: PODPIS:
--	---

SOUŘADNICOVÝ SYSTÉM: S-JTSK
VÝŠKOVÝ SYSTÉM: B.P.V.

ČISTOPIS

NÁZEV STAVBY: II/603 SULICE - ŽELIVEC, REKONSTRUKCE SILNICE A MOSTŮ
--

ČÁST / STAVEBNÍ OBJEKT: SO 102 - SILNICE II/603 ÚSEK 2 - EXTRAVILÁN
--

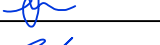PŘÍLOHA: VZOROVÉ PŘÍČNÉ ŘEZY					
 M - PROJEKCE, s.r.o. Resslova 956/13 500 02 Hradec Králové	ZHOTOVITEL RDS:	HLAVNÍ INŽENÝR PROJEKTU: Ing. M. STEJSKAL		PARÉ:	
		ZODPOVĚDNÝ PROJEKTANT: Ing. M. STEJSKAL			
		VYPRACOVAL: Ing. M. ŠPRONGL			
		KONTROLA: Ing. M. STEJSKAL			
		MĚŘÍTKO: Č. ZAKÁZKY: STUPEŇ: DATUM: ČÁST: PŘÍLOHA:			
		1:50 25-118-03 RDS 06/2026 102 4			