


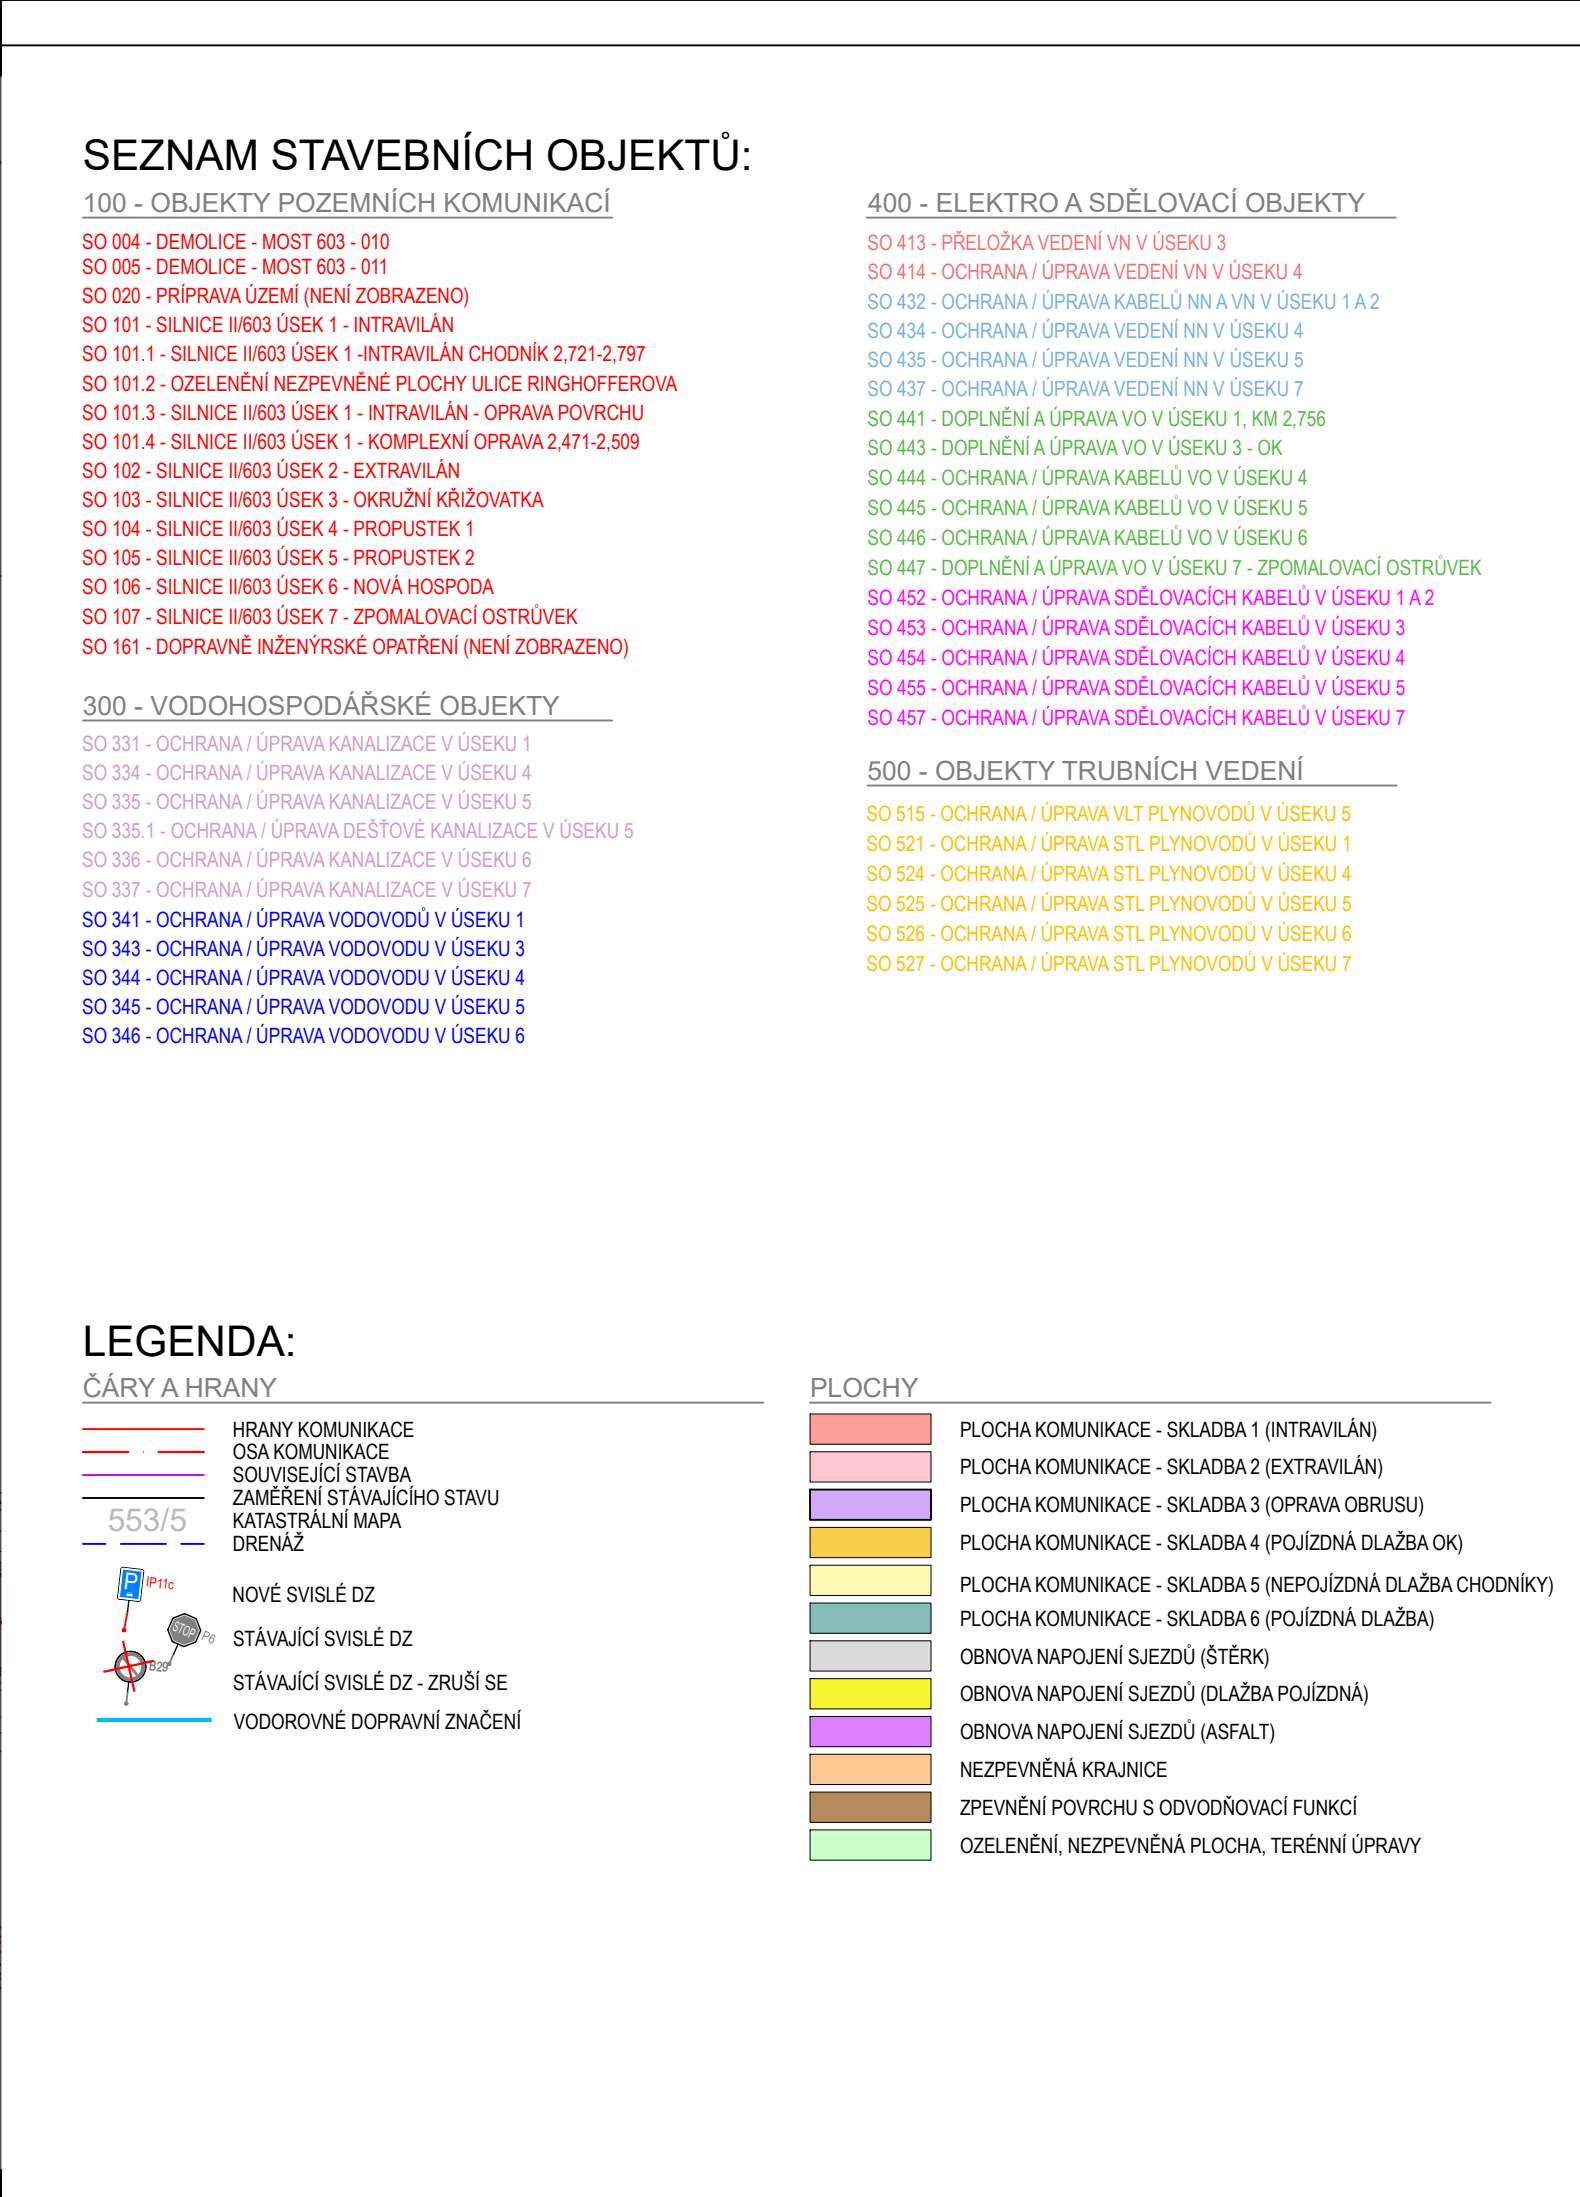

400 - ELEKTRO A SDĚLOVACÍ OBJEKTY

SO 413 - PŘELOŽKA VEDENÍ VN V ÚSEKU 3
SO 414 - OCHRANA / ÚPRAVA VEDENÍ VN V ÚSEKU 4
SO 432 - OCHRANA / ÚPRAVA KABELŮ NN A VN V ÚSEKU 1 A 2
SO 434 - OCHRANA / ÚPRAVA VEDENÍ VN V ÚSEKU 4
SO 435 - OCHRANA / ÚPRAVA VEDENÍ VN V ÚSEKU 5
SO 437 - OCHRANA / ÚPRAVA VEDENÍ VN V ÚSEKU 7
SO 441 - DOPLNĚNÍ A ÚPRAVA VO V ÚSEKU 1, KM 2,756
SO 443 - DOPLNĚNÍ A ÚPRAVA VO V ÚSEKU 3 - OK
SO 444 - OCHRANA / ÚPRAVA KABELŮ VO V ÚSEKU 4
SO 445 - OCHRANA / ÚPRAVA KABELŮ VO V ÚSEKU 5
SO 446 - OCHRANA / ÚPRAVA KABELŮ VO V ÚSEKU 6
SO 447 - DOPLNĚNÍ A ÚPRAVA VO V ÚSEKU 7 - ZPOMALOVACÍ OSTRŮVKE
SO 452 - OCHRANA / ÚPRAVA SĐELOVACÍCH KABELŮ V ÚSEKU 1 A 2
SO 453 - OCHRANA / ÚPRAVA SĐELOVACÍCH KABELŮ V ÚSEKU 3
SO 454 - OCHRANA / ÚPRAVA SĐELOVACÍCH KABELŮ V ÚSEKU 4
SO 455 - OCHRANA / ÚPRAVA SĐELOVACÍCH KABELŮ V ÚSEKU 5
SO 457 - OCHRANA / ÚPRAVA SĐELOVACÍCH KABELŮ V ÚSEKU 7

500 - OBJEKTY TRUBNÍCH VEDEN

SO 515 - OCHRANA / ÚPRAVA VLT PLYNOVODŮ V ÚSEKU
SO 521 - OCHRANA / ÚPRAVA STL PLYNOVODŮ V ÚSEKU
SO 524 - OCHRANA / ÚPRAVA STL PLYNOVODŮ V ÚSEKU
SO 525 - OCHRANA / ÚPRAVA STL PLYNOVODŮ V ÚSEKU
SO 526 - OCHRANA / ÚPRAVA STL PLYNOVODŮ V ÚSEKU
SO 527 - OCHRANA / ÚPRAVA STL PLYNOVODŮ V ÚSEKU

PLOCHY

	PLOCHA KOMUNIKACE - SKLADBA 1 (INTRAVILÁN)
	PLOCHA KOMUNIKACE - SKLADBA 2 (EXTRAVILÁN)
	PLOCHA KOMUNIKACE - SKLADBA 3 (OPRAVA OBRUSU)
	PLOCHA KOMUNIKACE - SKLADBA 4 (POJÍZDNÁ DLAŽBA OK)
	PLOCHA KOMUNIKACE - SKLADBA 5 (NEPOJÍZDNÁ DLAŽBA CHODNÍK)
	PLOCHA KOMUNIKACE - SKLADBA 6 (POJÍZDNÁ DLAŽBA)
	OBNOVA NAPOJENÍ SJEZDŮ (ŠTĚRK)
	OBNOVA NAPOJENÍ SJEZDŮ (DLAŽBA POJÍZDNÁ)
	OBNOVA NAPOJENÍ SJEZDŮ (ASFALT)
	NEZPEVNĚNÁ KRAJNICE
	ZPEVNĚNÍ POVRCHU S ODVODŇOVACÍ FUNKCÍ
	OZELENĚNÍ, NEZPEVNĚNÁ PLOCHA, TERÉNNÍ ÚPRAVY

SOUŘADNICOVÝ SYSTÉM: S-JTSK

VÝŠKOVÝ SYSTÉM: B.P.V.

ČISTOPIS

NÁZEV STAVBY:											
II/603 SULICE - ŽELIVEC, REKONSTRUKCE SILNICE A MOSTŮ											
ČÁST / STAVEBNÍ OBJEKT:											
SO 102 - SILNICE II/603 ÚSEK 2 - EXTRAVILÁN											
PŘÍLOHA:											
SITUACE DOPRAVNÍHO ZNAČENÍ (KM 1,300 - 1,600)											
ZHOTOVITEL RDS:  M - PROJEKCE, s.r.o. Resslova 956/13 500 02 Hradec Králové		HLAVNÍ INŽENÝR PROJEKTU:		Bc. R. MĚSTECKÝ				PARÉ:			
		ZODPOVĚDNÝ PROJEKTANT:		Ing. M. STEJSKAL							
		VYPRACOVAL:		Ing. M. ŠPRONGL							
		KONTROLA:		Ing. P. KELČA							
		MĚŘÍTKO:		Č. ZAKÁZKY:		STUPENĚ:		DATUM:		ČÁST:	
		1:500		25-118-03		RDS		06/2026		102	
								6.2			

ČISTOPIS