


SO 103 - SITUACE STAVBY
M 1:500

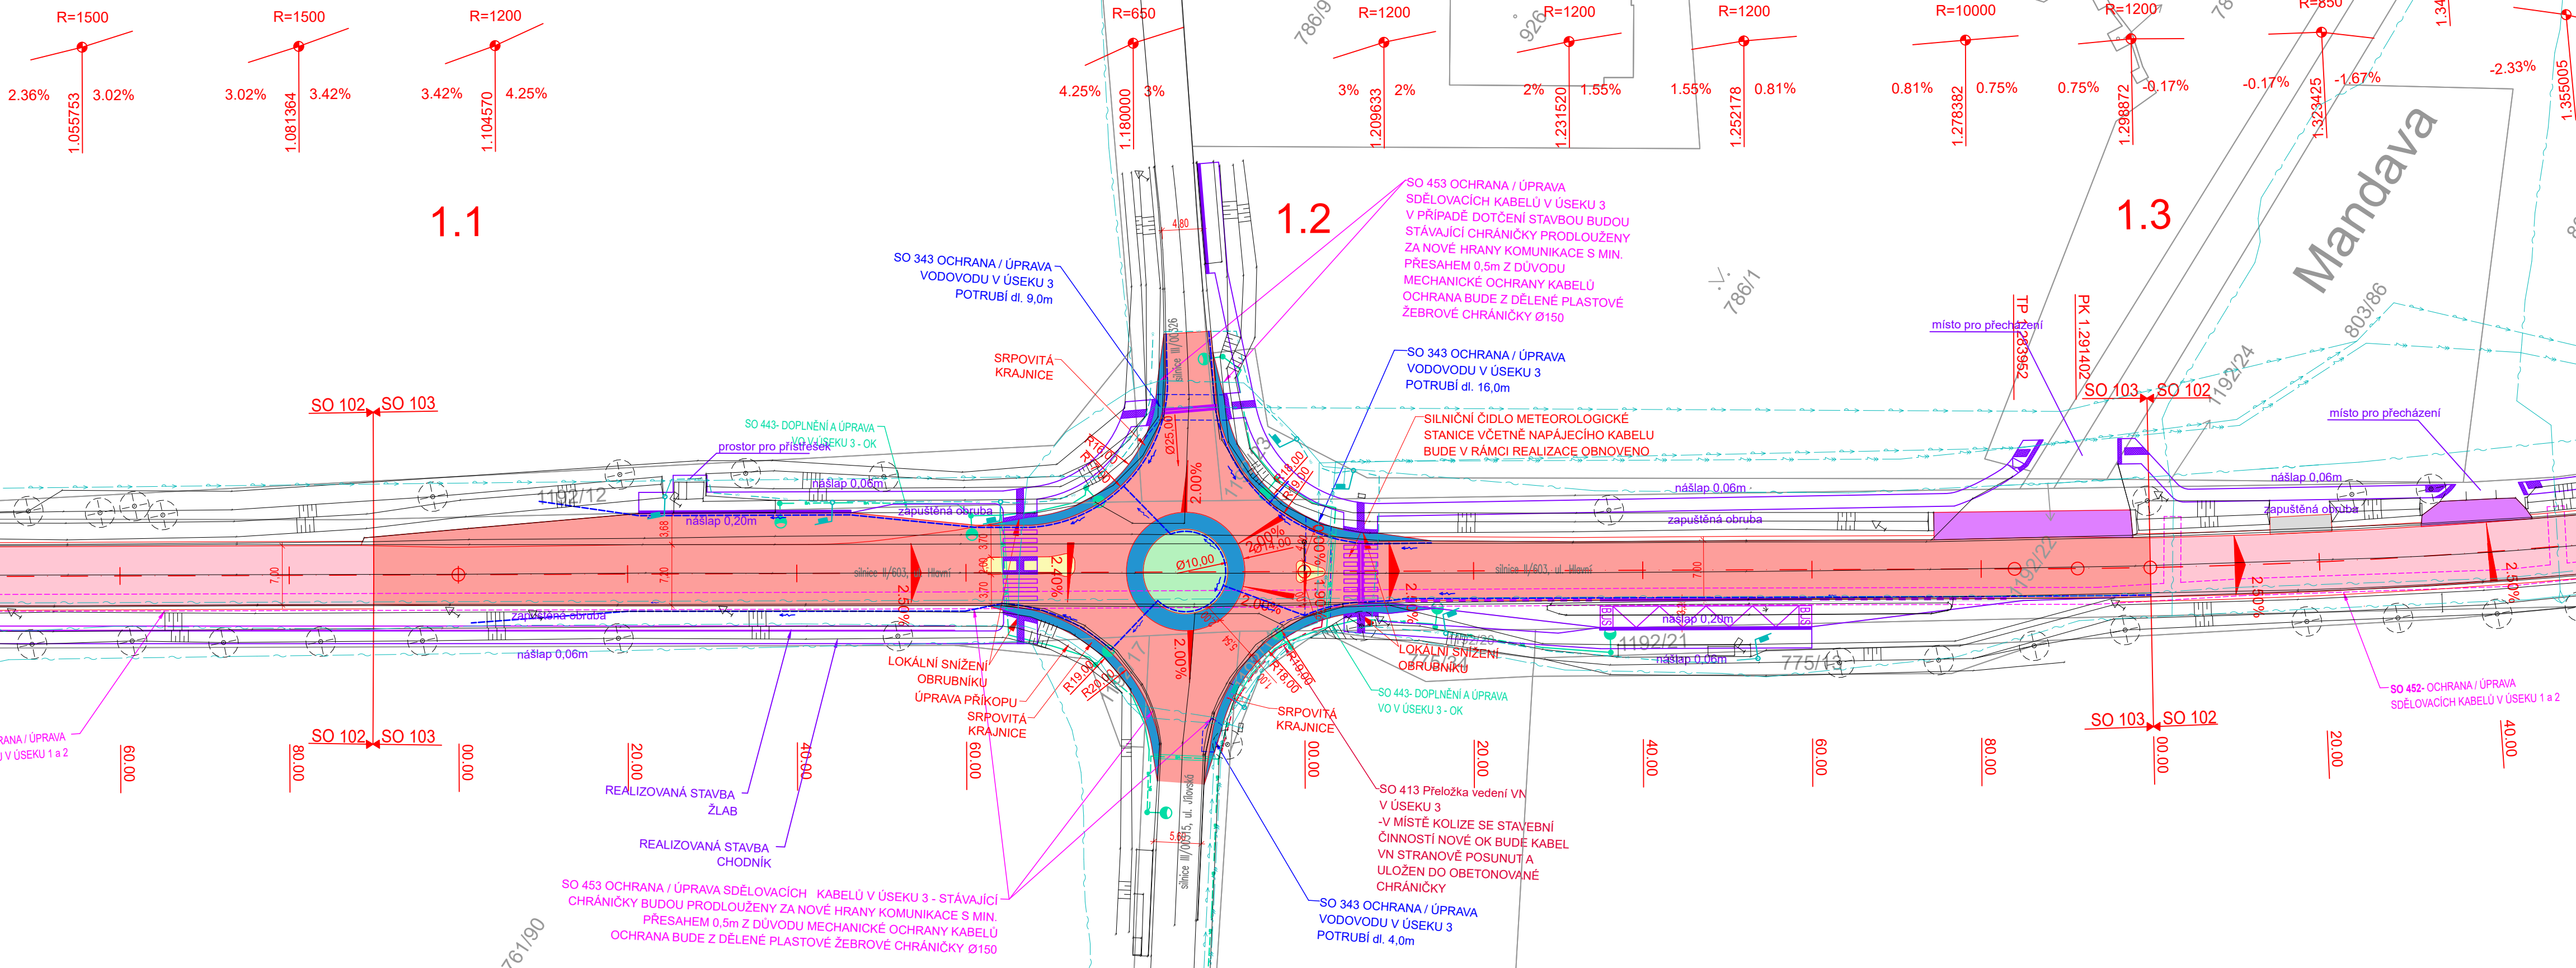

SEZNAM STAVEBNÍCH OBJEKTŮ:

100 - OBJEKTY POZEMNÍCH KOMUNIKACÍ

SO 101 - SILNICE II/603 ÚSEK 1 - INTRAVILÁN
SO 101.1 - SILNICE II/603 ÚSEK 1 - INTRAVILÁN CHODNÍK 2,721-2,797
SO 101.2 - OZELENÍ NEZPEVNĚNÉ PLOCHY ULICE RINGHOFFEROVA
SO 101.3 - SILNICE II/603 ÚSEK 1 - INTRAVILÁN - OPRAVA POVRCHU
SO 101.4 - SILNICE II/603 ÚSEK 1 - KOMPLEXNÍ OPRAVA 2,471-2,509
SO 102 - SILNICE II/603 ÚSEK 2 - EXTRAVILÁN
SO 103 - SILNICE II/603 ÚSEK 3 - OKRUŽNÍ KŘÍŽOVATKA
SO 104 - SILNICE II/603 ÚSEK 4 - PROPUSTEK 1
SO 105 - SILNICE II/603 ÚSEK 5 - PROPUSTEK 2
SO 106 - SILNICE II/603 ÚSEK 6 - NOVA HOSPODA
SO 107 - SILNICE II/603 ÚSEK 7 - ZPOMALOVACÍ OSTRŮVEK
SO 161 - DOPRAVNÍ INŽENÝRSKÉ OPATŘENÍ (NENÍ ZOBRAZENO)

300 - VODOHOSPODÁŘSKÉ OBJEKTY

SO 331 - OCHRANA / ÚPRAVA KANALIZACE V ÚSEKU 1
SO 334 - OCHRANA / ÚPRAVA KANALIZACE V ÚSEKU 4
SO 335 - OCHRANA / ÚPRAVA KANALIZACE V ÚSEKU 5
SO 335.1 - OCHRANA / ÚPRAVA DEŠŤOVÉ KANALIZACE V ÚSEKU 5
SO 336 - OCHRANA / ÚPRAVA KANALIZACE V ÚSEKU 6
SO 337 - OCHRANA / ÚPRAVA KANALIZACE V ÚSEKU 7
SO 341 - OCHRANA / ÚPRAVA VODOVODU V ÚSEKU 1
SO 343 - OCHRANA / ÚPRAVA VODOVODU V ÚSEKU 3
SO 344 - OCHRANA / ÚPRAVA VODOVODU V ÚSEKU 4
SO 345 - OCHRANA / ÚPRAVA VODOVODU V ÚSEKU 5
SO 346 - OCHRANA / ÚPRAVA VODOVODU V ÚSEKU 6

400 - ELEKTRO A SDĚLOVACÍ OBJEKTY

SO 413 - PŘELOŽKA VEDENÍ VN V ÚSEKU 3
SO 414 - OCHRANA / ÚPRAVA VEDENÍ VN V ÚSEKU 4
SO 432 - OCHRANA / ÚPRAVA KABELŮ NN A VN V ÚSEKU 1 A 2
SO 434 - OCHRANA / ÚPRAVA VEDENÍ NN V ÚSEKU 4
SO 435 - OCHRANA / ÚPRAVA VEDENÍ NN V ÚSEKU 5
SO 437 - OCHRANA / ÚPRAVA VEDENÍ NN V ÚSEKU 7
SO 441 - DOPLNĚNÍ A ÚPRAVA VO V ÚSEKU 1, KM 2,756
SO 443 - DOPLNĚNÍ A ÚPRAVA VO V ÚSEKU 3 - OK
SO 444 - OCHRANA / ÚPRAVA KABELŮ VO V ÚSEKU 4
SO 445 - OCHRANA / ÚPRAVA KABELŮ VO V ÚSEKU 5
SO 446 - OCHRANA / ÚPRAVA KABELŮ VO V ÚSEKU 6
SO 447 - DOPLNĚNÍ A ÚPRAVA VO V ÚSEKU 7 - ZPOMALOVACÍ OSTRŮVEK
SO 452 - OCHRANA / ÚPRAVA SDĚLOVACÍCH KABELŮ V ÚSEKU 1 A 2
SO 453 - OCHRANA / ÚPRAVA SDĚLOVACÍCH KABELŮ V ÚSEKU 3
SO 454 - OCHRANA / ÚPRAVA SDĚLOVACÍCH KABELŮ V ÚSEKU 4
SO 455 - OCHRANA / ÚPRAVA SDĚLOVACÍCH KABELŮ V ÚSEKU 5
SO 457 - OCHRANA / ÚPRAVA SDĚLOVACÍCH KABELŮ V ÚSEKU 7

500 - OBJEKTY TRUBNÍCH VEDENÍ

SO 515 - OCHRANA / ÚPRAVA VLT PLYNOVODŮ V ÚSEKU 5
SO 521 - OCHRANA / ÚPRAVA STL PLYNOVODŮ V ÚSEKU 1
SO 524 - OCHRANA / ÚPRAVA STL PLYNOVODŮ V ÚSEKU 4
SO 525 - OCHRANA / ÚPRAVA STL PLYNOVODŮ V ÚSEKU 5
SO 526 - OCHRANA / ÚPRAVA STL PLYNOVODŮ V ÚSEKU 6
SO 527 - OCHRANA / ÚPRAVA STL PLYNOVODŮ V ÚSEKU 7

LEGENDA:

ČÁRY A HRANY

--- HRANY KOMUNIKACE
--- OSA KOMUNIKACE
--- SOUVISEJÍCÍ STAVBA
--- ZAMĚŘENÍ STÁVAJÍCÍHO STAVU
--- KATASTRÁLNÍ MAPA
--- DRENAŽ

PLOCHY

PLOCHA KOMUNIKACE - SKLADBA 1 (INTRAVILÁN)
PLOCHA KOMUNIKACE - SKLADBA 2 (EXTRAVILÁN)
PLOCHA KOMUNIKACE - SKLADBA 3 (OPRAVA OBRUSU)
PLOCHA KOMUNIKACE - SKLADBA 4 (POJÍZDNÁ DLAŽBA OK)
PLOCHA KOMUNIKACE - SKLADBA 5 (NEPOJÍZDNÁ DLAŽBA CHODNÍKY)
PLOCHA KOMUNIKACE - SKLADBA 6 (POJÍZDNÁ DLAŽBA)
OBNOVA NAPOJENÍ SJEZDŮ (ŠTĚRK)
OBNOVA NAPOJENÍ SJEZDŮ (DLAŽBA POJÍZDNÁ)
OBNOVA NAPOJENÍ SJEZDŮ (ASFALT)
NEZPEVNĚNÁ KRAJNICE
ZPEVNĚNÍ POVRCHU S ODVODNOVACÍ FUNKCÍ
OZELENÍ, NEZPEVNĚNÁ PLOCHA, TERÉNNÍ ÚPRAVY

LEGENDA INŽENÝRSKÝCH SÍTÍ:

STÁVAJÍCÍ

--- VODOVOD, PŘÍPOJKY
--- PODZEMNÍ VEDENÍ NN
--- NADZEMNÍ VEDENÍ NN
--- PODZEMNÍ VEDENÍ VN
--- NADZEMNÍ VEDENÍ VN
--- SDĚLOVACÍ VEDENÍ - BEZ ROZLIŠENÍ
--- VĚŘEJNÉ OSVĚTLENÍ
--- PLYNOVÉ STL
--- PLYNOVÉ VTL
--- KANALIZACE - BEZ ROZLIŠENÍ

POZN. POLOHA INŽ. SÍTÍ JE POUZE ORIENTAČNÍ. PŘED
PROVÁDĚNÍM STAVEBNÍCH PRACÍ JE NEZBYTNÉ PROVĚST
VYTÝČENÍ VEŠKERÝCH INŽENÝRSKÝCH SÍTÍ.

REVIZE:	PŘEDMĚT ZMĚNY:	DATUM:	VYPRACOVAL:
a			
b			
c			

NÁZEV STAVBY:	ČÍSLO OBJEKTU:
II/603 SULICE - ŽELIVEC, REK. SILNICE A MOSTŮ	SO 103

INVESTOR STAVBY č.1:	RAŽITKO:
 KRAJSKÁ SPRÁVA A ÚDRŽBA SILNIC STŘEDOČESKÉHO KRAJE p.o. Zborovská 81/11, 150 21 Praha 5	DATUM: _____ PODPIS: _____

INVESTOR STAVBY č.2:	RAŽITKO:
 OBEC KAMENICE Ringhofferovo náměstí 434 Olešovice, 251 68 Kamenice	DATUM: _____ PODPIS: _____

TECHNICKÝ DOZOR INVESTORA	RAŽITKO:
 REALSTAV MB, s.r.o. Klaudíanova 124, 293 01 Mladá Boleslav	KONTROLOVAL: _____ DATUM: _____ PODPIS: _____

ZHOTOVITEL STAVBY:	RAŽITKO:
 M - SILNICE, a.s. Husova 1697, Bílé Předměstí, 530 03 Pardubice	KONTROLOVAL: _____ DATUM: _____ PODPIS: _____

KOORDINÁTOR RDS:	RAŽITKO:
 M - PROJEKCE, s.r.o. Resslova 956/13, 500 02 Hradec Králové	KONTROLOVAL: _____ DATUM: _____ PODPIS: _____

SOUŘADNICOVÝ SYSTÉM: S-JTSK
VÝŠKOVÝ SYSTÉM: B.P.V.

NÁZEV STAVBY:
II/603 SULICE - ŽELIVEC, REKONSTRUKCE SILNICE A MOSTŮ

ČÁST / STAVEBNÍ OBJEKT:
SO 103 - SILNICE II/603 ÚSEK 3 - OKRUŽNÍ KŘÍŽOVATKA

PŘÍLOHA:
SITUACE STAVBY (KM 1,090 - 1,300)

ZHOTOVITEL RDS:  M - PROJEKCE, s.r.o. Resslova 956/13 500 02 Hradec Králové	HLAVNÍ INŽENÝR PROJEKTU:		Bc. R. MĚSTECKÝ		<i>Městecký</i>		PARÉ:
	ZODPOVĚDNÝ PROJEKTANT:		Ing. M. STEJSKAL		<i>Stejskal</i>		
	VYPRACOVAL:		Ing. M. ŠPRONGL		<i>Šprongl</i>		
	KONTROLA:		Ing. P. KELČA		<i>Kelča</i>		
	MĚŘITKO:		Č. ZAKÁZKY:	STUPEŇ:	DATUM:	ČÁST:	
	1:500	25-118-03	RDS	06/2026	103	2	

ČISTOPIS