

SO 103 - PODÉLNÝ PROFIL
M 1:1000/100

DRUH POVRCHU ÚZEMÍ:
KATASTRÁLNÍ ÚZEMÍ:
OKRES:
KRAJ:

OSTATNÍ PLOCHA - silnice
SULICE [759431]
PRAHA - VÝCHOD
STŘEDOČESKÝ

BENEŠOV ⇄

⇄ PRAHA

MĚŘITKA:
1: 1000, 1: 100

SKLONOVÉ POMĚRY

KÓTY NIVELETY

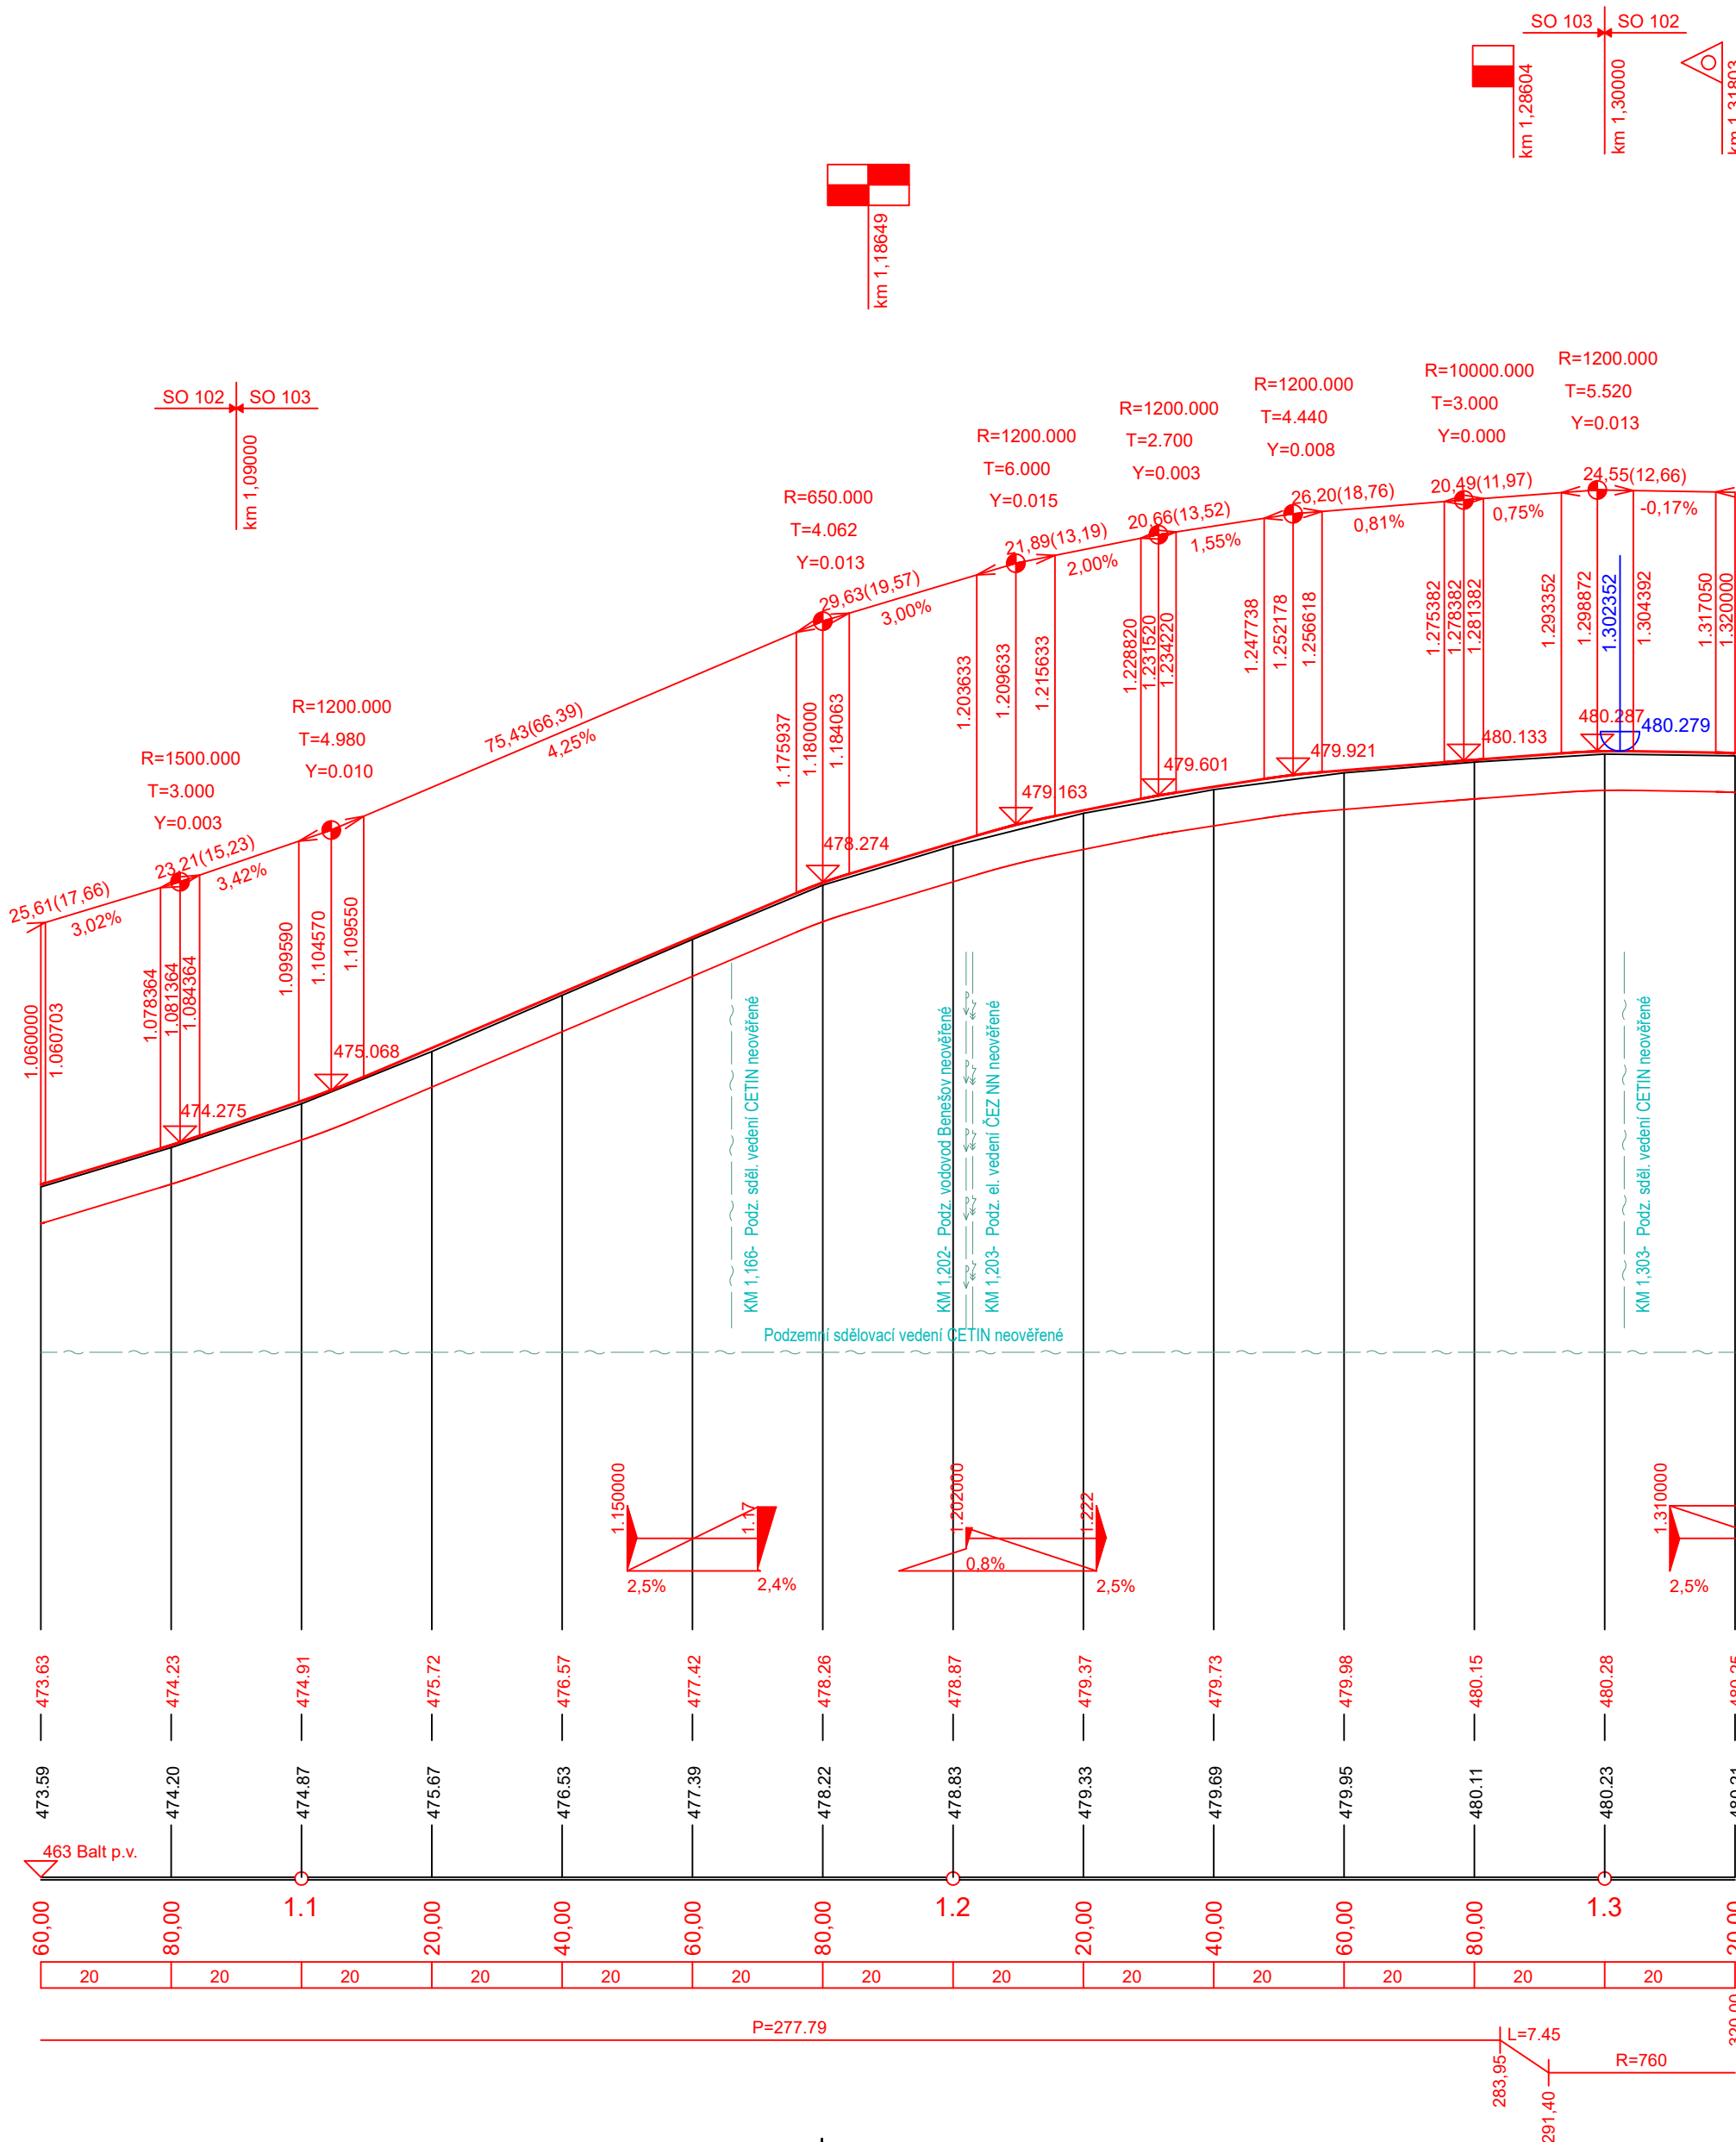
KÓTY TERÉNU

SROVNÁVACÍ ROVINA:

STANIČENÍ

VZDÁLENOST PŘ. ŘEZŮ:

SMĚROVÉ POMĚRY



DRUH POVRCHU ÚZEMÍ:
KATASTRÁLNÍ ÚZEMÍ:
OKRES:
KRAJ:

OSTATNÍ PLOCHA - silnice
SULICE [759431]
PRAHA - VÝCHOD
STŘEDOČESKÝ

SKLONOVÉ POMĚRY

MĚŘITKA:
1: 1000, 1: 100

KÓTY NIVELETY

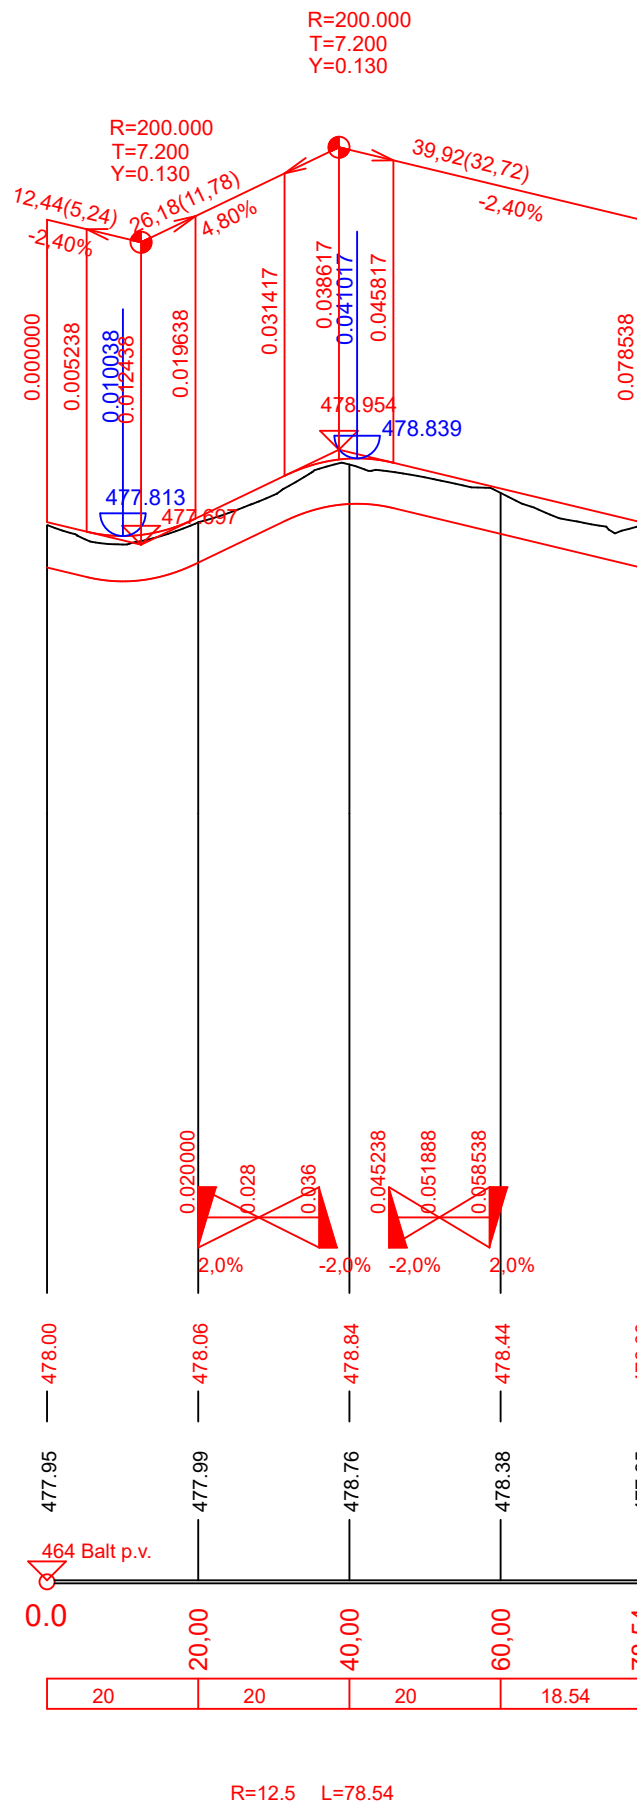
KÓTY TERÉNU

SROVNÁVACÍ ROVINA:

STANIČENÍ

VZDÁLENOST PŘ. ŘEZŮ:

SMĚROVÉ POMĚRY



REVIZE:	PŘEDMĚT ZMĚNY:	DATUM:	VYPRACOVAL:
a			
b			
c			

NÁZEV STAVBY: II/603 SULICE - ŽELIVEC, REK. SILNICE A MOSTŮ	ČÍSLO OBJEKTU: SO 103
--	--------------------------

INVESTOR STAVBY č.1:  KRAJSKÁ SPRÁVA A ÚDRŽBA SILNIC STŘEDOČESKÉHO KRAJE p.o. Zborovská 81/11, 150 21 Praha 5	RAŽITKO: DATUM: PODPIS:
---	----------------------------

INVESTOR STAVBY č.2:  OBEC KAMENICE Ringhofferovo náměstí 434 Olešovice, 251 68 Kamenice	RAŽITKO: DATUM: PODPIS:
---	----------------------------




TECHNICKÝ DOZOR INVESTORA  REALSTAV MB, s.r.o. Klaudánova 124, 293 01 Mladá Boleslav	RAŽITKO: Kontroloval: DATUM: PODPIS:
---	--

ZHOTOVITEL STAVBY:  M - SILNICE, a.s. Husova 1697, Bílé Předměstí, 530 03 Pardubice	RAŽITKO: Kontroloval: DATUM: PODPIS:
--	--

KOORDINÁTOR RDS:  M - PROJEKCE, s.r.o. Resslova 956/13, 500 02 Hradec Králové	RAŽITKO: Kontroloval: DATUM: PODPIS:
--	--

SOURADNICOVÝ SYSTÉM: S-JTSK
VÝŠKOVÝ SYSTÉM: B.P.V.

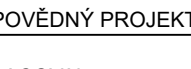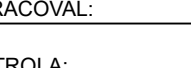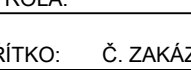ČISTOPIS

NÁZEV STAVBY: II/603 SULICE - ŽELIVEC, REKONSTRUKCE SILNICE A MOSTŮ					
ČÁST / STAVEBNÍ OBJEKT: SO 103 - SILNICE II/603 OKRUŽNÍ KŘIŽOVATKA					
PŘÍLOHA: PODÉLNÝ PROFIL					
ZHOTOVITEL RDS:  M - PROJEKCE, s.r.o. Resslova 956/13 500 02 Hradec Králové	HLAVNÍ INŽENÝR PROJEKTU:	Bc. R. MĚSTECKÝ		PARÉ:	
	ZODPOVĚDNÝ PROJEKTANT:	Ing. M. STEJSKAL			
	VYPRACOVAL:	Bc. R. MĚSTECKÝ			
	KONTROLA:	Ing. P. KEJČA			
	MĚŘITKO:	Č. ZAKÁZKY:	STUPEŇ:	DATUM:	ČÁST:
1:1000/100		25-118-03	RDS	06/2026	103
				ČÁST:	PŘÍLOHA:
				3	3