

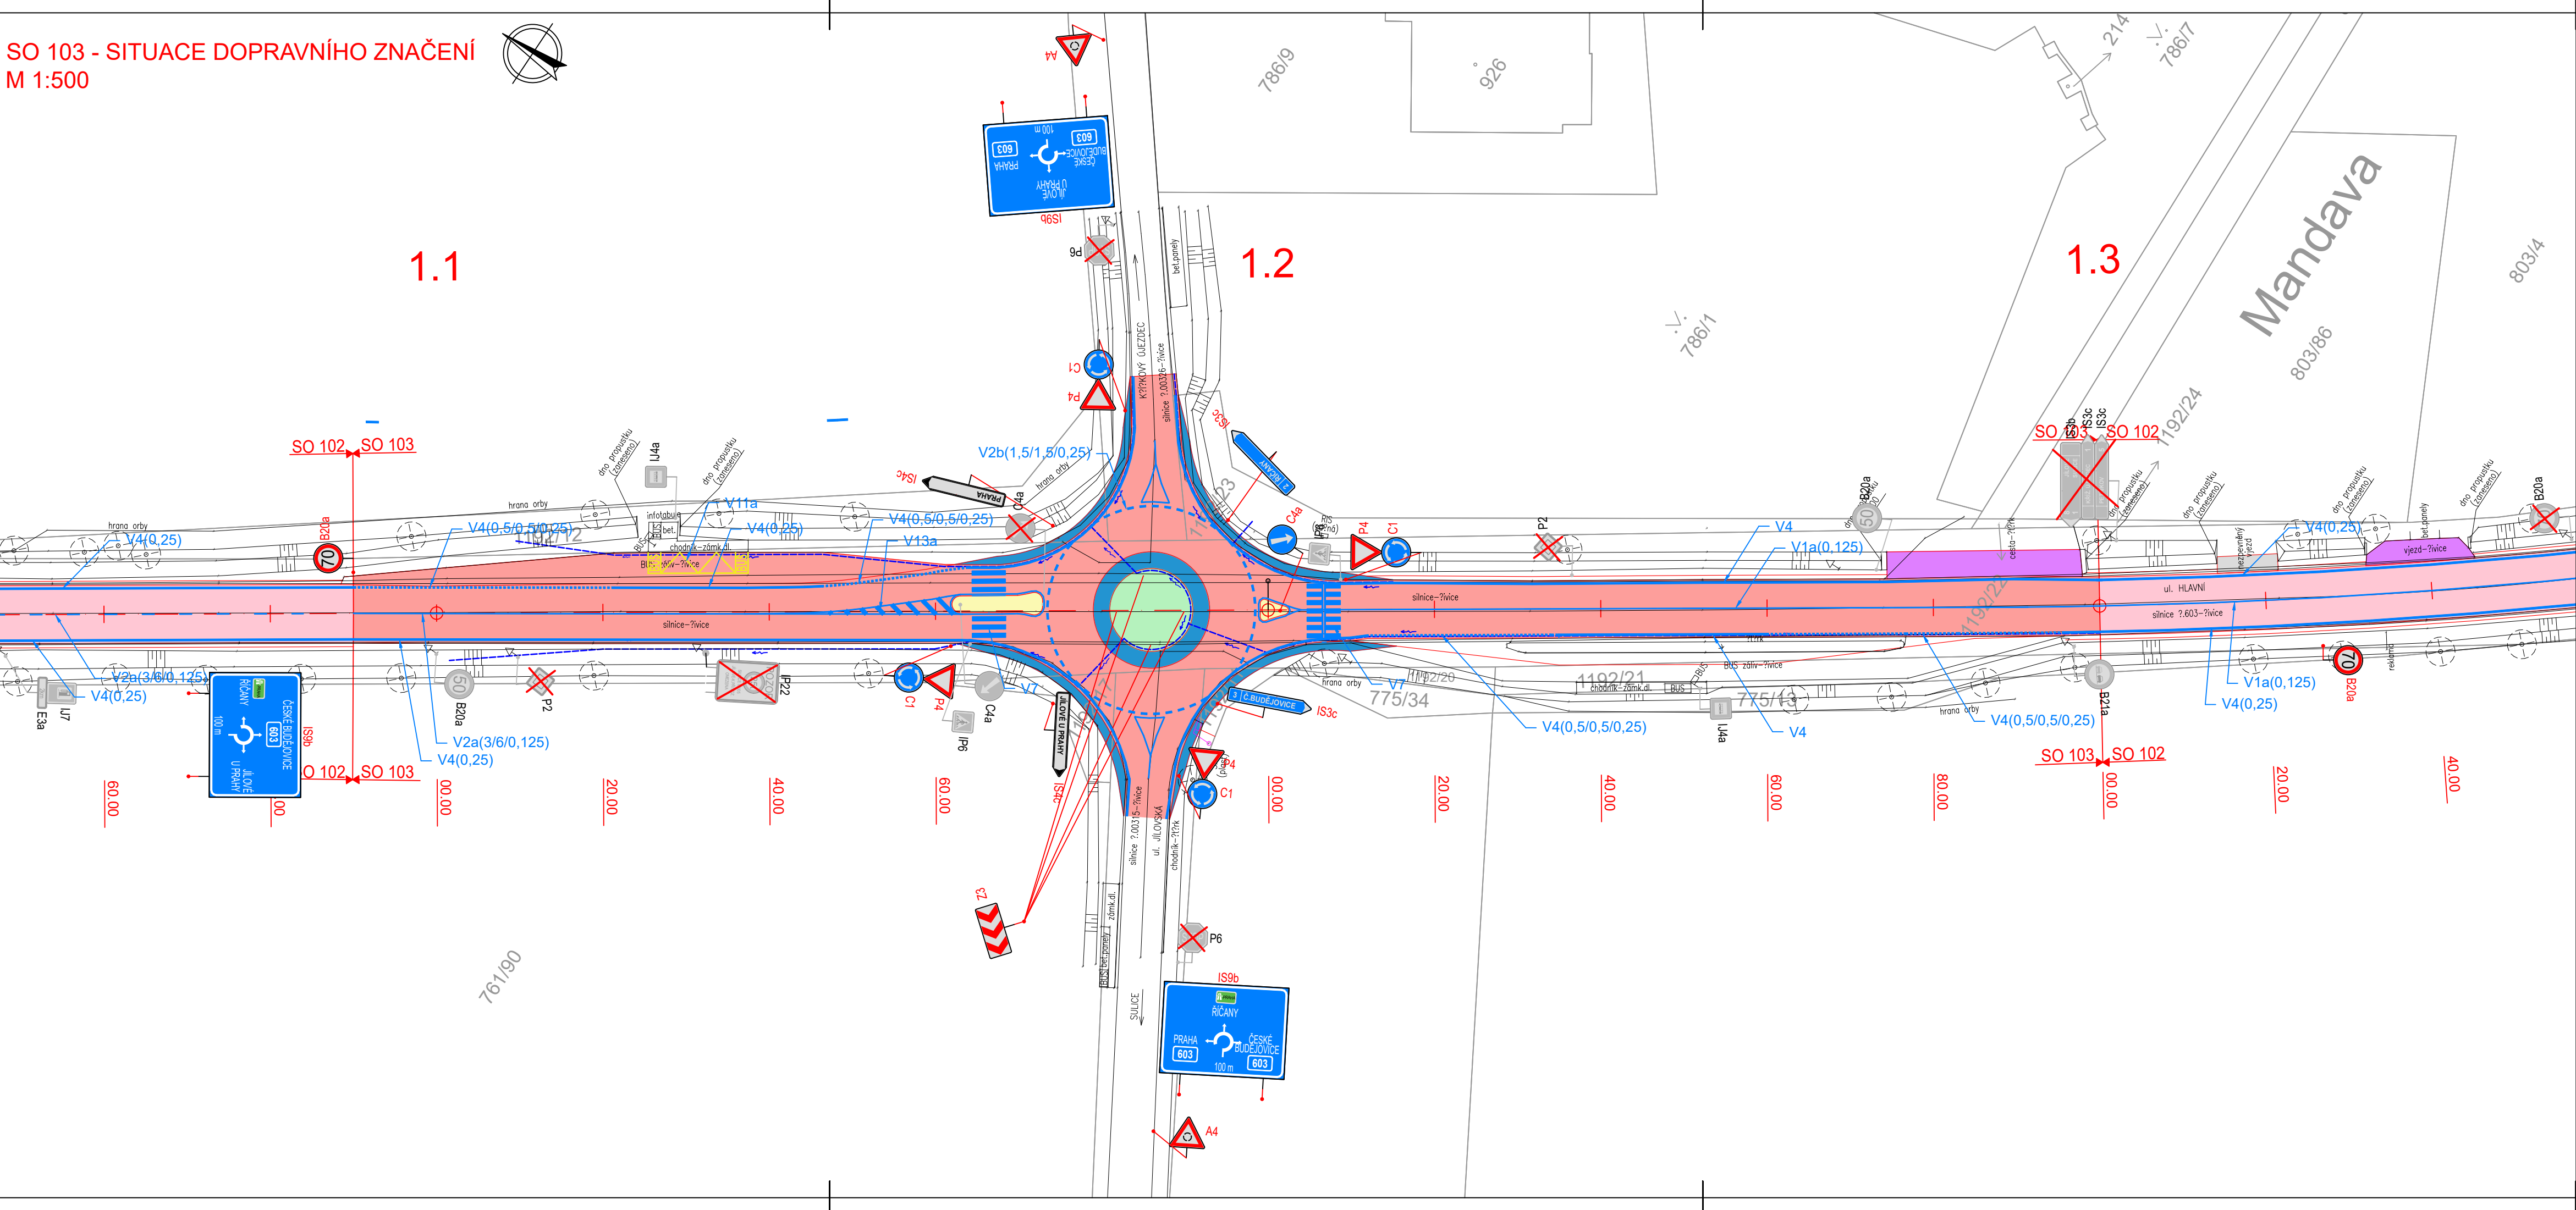
SO 103 - SITUACE DOPRAVNÍHO ZNAČENÍ
M 1:500



1.1

1.2

1.3



SEZNAM STAVEBNÍCH OBJEKTŮ:

100 - OBJEKTY POZEMNÍCH KOMUNIKACÍ

- SO 101 - SILNICE II/603 ÚSEK 1 - INTRAVILÁN
- SO 101.1 - SILNICE II/603 ÚSEK 1 - INTRAVILÁN CHODNÍK 2,721-2,797
- SO 101.2 - OZELENĚNÍ NEZPEVNĚNÉ PLOCHY ULICE RINGHOFFEROVA
- SO 101.3 - SILNICE II/603 ÚSEK 1 - INTRAVILÁN - OPRAVA POVRCHU
- SO 101.4 - SILNICE II/603 ÚSEK 1 - KOMPLEXNÍ OPRAVA 2,471-2,509
- SO 102 - SILNICE II/603 ÚSEK 2 - EXTRAVILÁN
- SO 103 - SILNICE II/603 ÚSEK 3 - OKRUŽNÍ KŘÍŽOVATKA
- SO 104 - SILNICE II/603 ÚSEK 4 - PROPUSTEK 1
- SO 105 - SILNICE II/603 ÚSEK 5 - PROPUSTEK 2
- SO 106 - SILNICE II/603 ÚSEK 6 - NOVÁ HOSPODA
- SO 107 - SILNICE II/603 ÚSEK 7 - ZPOMALOVACÍ OSTRŮVEK
- SO 161 - DOPRAVNĚ INŽENÝRSKÉ OPATŘENÍ (NENÍ ZOBRAZENO)

300 - VODOHOSPODÁŘSKÉ OBJEKTY

- SO 331 - OCHRANA / ÚPRAVA KANALIZACE V ÚSEKU 1
- SO 334 - OCHRANA / ÚPRAVA KANALIZACE V ÚSEKU 4
- SO 335 - OCHRANA / ÚPRAVA KANALIZACE V ÚSEKU 5
- SO 335.1 - OCHRANA / ÚPRAVA DEŠŤOVÉ KANALIZACE V ÚSEKU 5
- SO 336 - OCHRANA / ÚPRAVA KANALIZACE V ÚSEKU 6
- SO 337 - OCHRANA / ÚPRAVA KANALIZACE V ÚSEKU 7
- SO 341 - OCHRANA / ÚPRAVA VODOVODU V ÚSEKU 1
- SO 343 - OCHRANA / ÚPRAVA VODOVODU V ÚSEKU 3
- SO 344 - OCHRANA / ÚPRAVA VODOVODU V ÚSEKU 4
- SO 345 - OCHRANA / ÚPRAVA VODOVODU V ÚSEKU 5
- SO 346 - OCHRANA / ÚPRAVA VODOVODU V ÚSEKU 6

400 - ELEKTRO A SDĚLOVACÍ OBJEKTY

- SO 413 - PŘELOŽKA VEDENÍ VN V ÚSEKU 3
- SO 414 - OCHRANA / ÚPRAVA VEDENÍ VN V ÚSEKU 4
- SO 432 - OCHRANA / ÚPRAVA KABELŮ NN A VN V ÚSEKU 1 A 2
- SO 434 - OCHRANA / ÚPRAVA VEDENÍ NN V ÚSEKU 4
- SO 435 - OCHRANA / ÚPRAVA VEDENÍ NN V ÚSEKU 5
- SO 437 - OCHRANA / ÚPRAVA VEDENÍ NN V ÚSEKU 7
- SO 441 - DOPLNĚNÍ A ÚPRAVA VO V ÚSEKU 1, KM 2,756
- SO 443 - DOPLNĚNÍ A ÚPRAVA VO V ÚSEKU 3 - OK
- SO 444 - OCHRANA / ÚPRAVA KABELŮ VO V ÚSEKU 4
- SO 445 - OCHRANA / ÚPRAVA KABELŮ VO V ÚSEKU 5
- SO 446 - OCHRANA / ÚPRAVA KABELŮ VO V ÚSEKU 6
- SO 447 - DOPLNĚNÍ A ÚPRAVA VO V ÚSEKU 7 - ZPOMALOVACÍ OSTRŮVEK
- SO 452 - OCHRANA / ÚPRAVA SDĚLOVACÍCH KABELŮ V ÚSEKU 1 A 2
- SO 453 - OCHRANA / ÚPRAVA SDĚLOVACÍCH KABELŮ V ÚSEKU 3
- SO 454 - OCHRANA / ÚPRAVA SDĚLOVACÍCH KABELŮ V ÚSEKU 4
- SO 455 - OCHRANA / ÚPRAVA SDĚLOVACÍCH KABELŮ V ÚSEKU 5
- SO 457 - OCHRANA / ÚPRAVA SDĚLOVACÍCH KABELŮ V ÚSEKU 7

500 - OBJEKTY TRUBNÍCH VEDENÍ

- SO 515 - OCHRANA / ÚPRAVA VLT PLYNOVODŮ V ÚSEKU 5
- SO 521 - OCHRANA / ÚPRAVA STL PLYNOVODŮ V ÚSEKU 1
- SO 524 - OCHRANA / ÚPRAVA STL PLYNOVODŮ V ÚSEKU 4
- SO 525 - OCHRANA / ÚPRAVA STL PLYNOVODŮ V ÚSEKU 5
- SO 526 - OCHRANA / ÚPRAVA STL PLYNOVODŮ V ÚSEKU 6
- SO 527 - OCHRANA / ÚPRAVA STL PLYNOVODŮ V ÚSEKU 7

LEGENDA:

ČÁRY A HRANY

- HRANY KOMUNIKACE
- OSA KOMUNIKACE
- SOUVISEJÍCÍ STAVBA
- ZAMĚŘENÍ STÁVAJÍCÍHO STAVU
- KATASTRÁLNÍ MAPA
- DRENAŽ
- NOVÉ SVISLÉ DZ
- STÁVAJÍCÍ SVISLÉ DZ
- STÁVAJÍCÍ SVISLÉ DZ - ZRUŠÍ SE
- VODOROVNÉ DOPRAVNÍ ZNAČENÍ

PLOCHY

- PLOCHA KOMUNIKACE - SKLADBA 1 (INTRAVILÁN)
- PLOCHA KOMUNIKACE - SKLADBA 2 (EXTRAVILÁN)
- PLOCHA KOMUNIKACE - SKLADBA 3 (OPRAVA OBRUSU)
- PLOCHA KOMUNIKACE - SKLADBA 4 (POJÍZDNÁ DLAŽBA OK)
- PLOCHA KOMUNIKACE - SKLADBA 5 (NEPOJÍZDNÁ DLAŽBA CHODNÍKY)
- PLOCHA KOMUNIKACE - SKLADBA 6 (POJÍZDNÁ DLAŽBA)
- OBNOVA NAPOJENÍ SJEZDŮ (ŠTĚRK)
- OBNOVA NAPOJENÍ SJEZDŮ (DLAŽBA POJÍZDNÁ)
- OBNOVA NAPOJENÍ SJEZDŮ (ASFALT)
- NEZPEVNĚNÁ KRAJNICE
- ZPEVNĚNÍ POVRCHU S ODVODŇOVACÍ FUNKCÍ
- OZELENĚNÍ, NEZPEVNĚNÁ PLOCHA, TERÉNNÍ ÚPRAVY

REVIZE:	PŘEDMĚT ZMĚNY:	DATUM:	VYPRACOVAL:
a			
b			
c			

NÁZEV STAVBY: II/603 SULICE - ŽELIVEC, REK. SILNICE A MOSTŮ	ČÍSLO OBJEKTU: SO 103
--	--------------------------

INVESTOR STAVBY č.1:  KRAJSKÁ SPRÁVA A ÚDRŽBA SILNIC STŘEDOČESKÉHO KRAJE p.o. Zborovská 81/11, 150 21 Praha 5	RAZÍTKO: DATUM: PODPIS:
---	--------------------------------

INVESTOR STAVBY č.2:  OBEC KAMENICE Ringhofferovo náměstí 434 Olešovice, 251 68 Kamenice	RAZÍTKO: DATUM: PODPIS:
--	--------------------------------

TECHNICKÝ DOZOR INVESTORA  REALSTAV MB, s.r.o. Klaudiovna 124, 293 01 Mladá Boleslav	RAZÍTKO: KONTOLOVAL: DATUM: PODPIS:
---	---

ZHOTOVITEL STAVBY:  M - SILNICE, a.s. Husova 1697, Bílé Předměstí, 530 03 Pardubice	RAZÍTKO: KONTOLOVAL: DATUM: PODPIS:
--	---

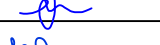
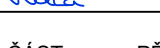
KOORDINÁTOR RDS:  M - PROJEKCE, s.r.o. Resslova 956/13, 500 02 Hradec Králové	RAZÍTKO: KONTOLOVAL: DATUM: PODPIS:
--	---

SOUDNICOVÝ SYSTÉM: S-JTSK
VÝŠKOVÝ SYSTÉM: B.P.V.

ČISTOPIS

NÁZEV STAVBY: II/603 SULICE - ŽELIVEC, REKONSTRUKCE SILNICE A MOSTŮ
--

ČÁST / STAVEBNÍ OBJEKT: SO 103 - SILNICE II/603 ÚSEK 3 - OKRUŽNÍ KŘÍŽOVATKA
--

PŘÍLOHA: SITUACE DOPRAVNÍHO ZNAČENÍ (KM 1,090 - 1,300)				
ZHOTOVITEL RDS:  M - PROJEKCE, s.r.o. Resslova 956/13 500 02 Hradec Králové	HLAVNÍ INŽENÝR PROJEKTU: Bc. R. MĚSTECKÝ		PARÉ:	
	ZODPOVĚDNÝ PROJEKTANT: Ing. M. STEJSKAL			
	VYPRACOVAL: Ing. M. ŠPRONGL			
	KONTROLA: Ing. P. KELČA			
	MĚŘÍTKO: 1:500	Č. ZAKÁZKY: 25-118-03	STUPEŇ: RDS	DATUM: 06/2026
			ČÁST: 103	PŘÍLOHA: 6