



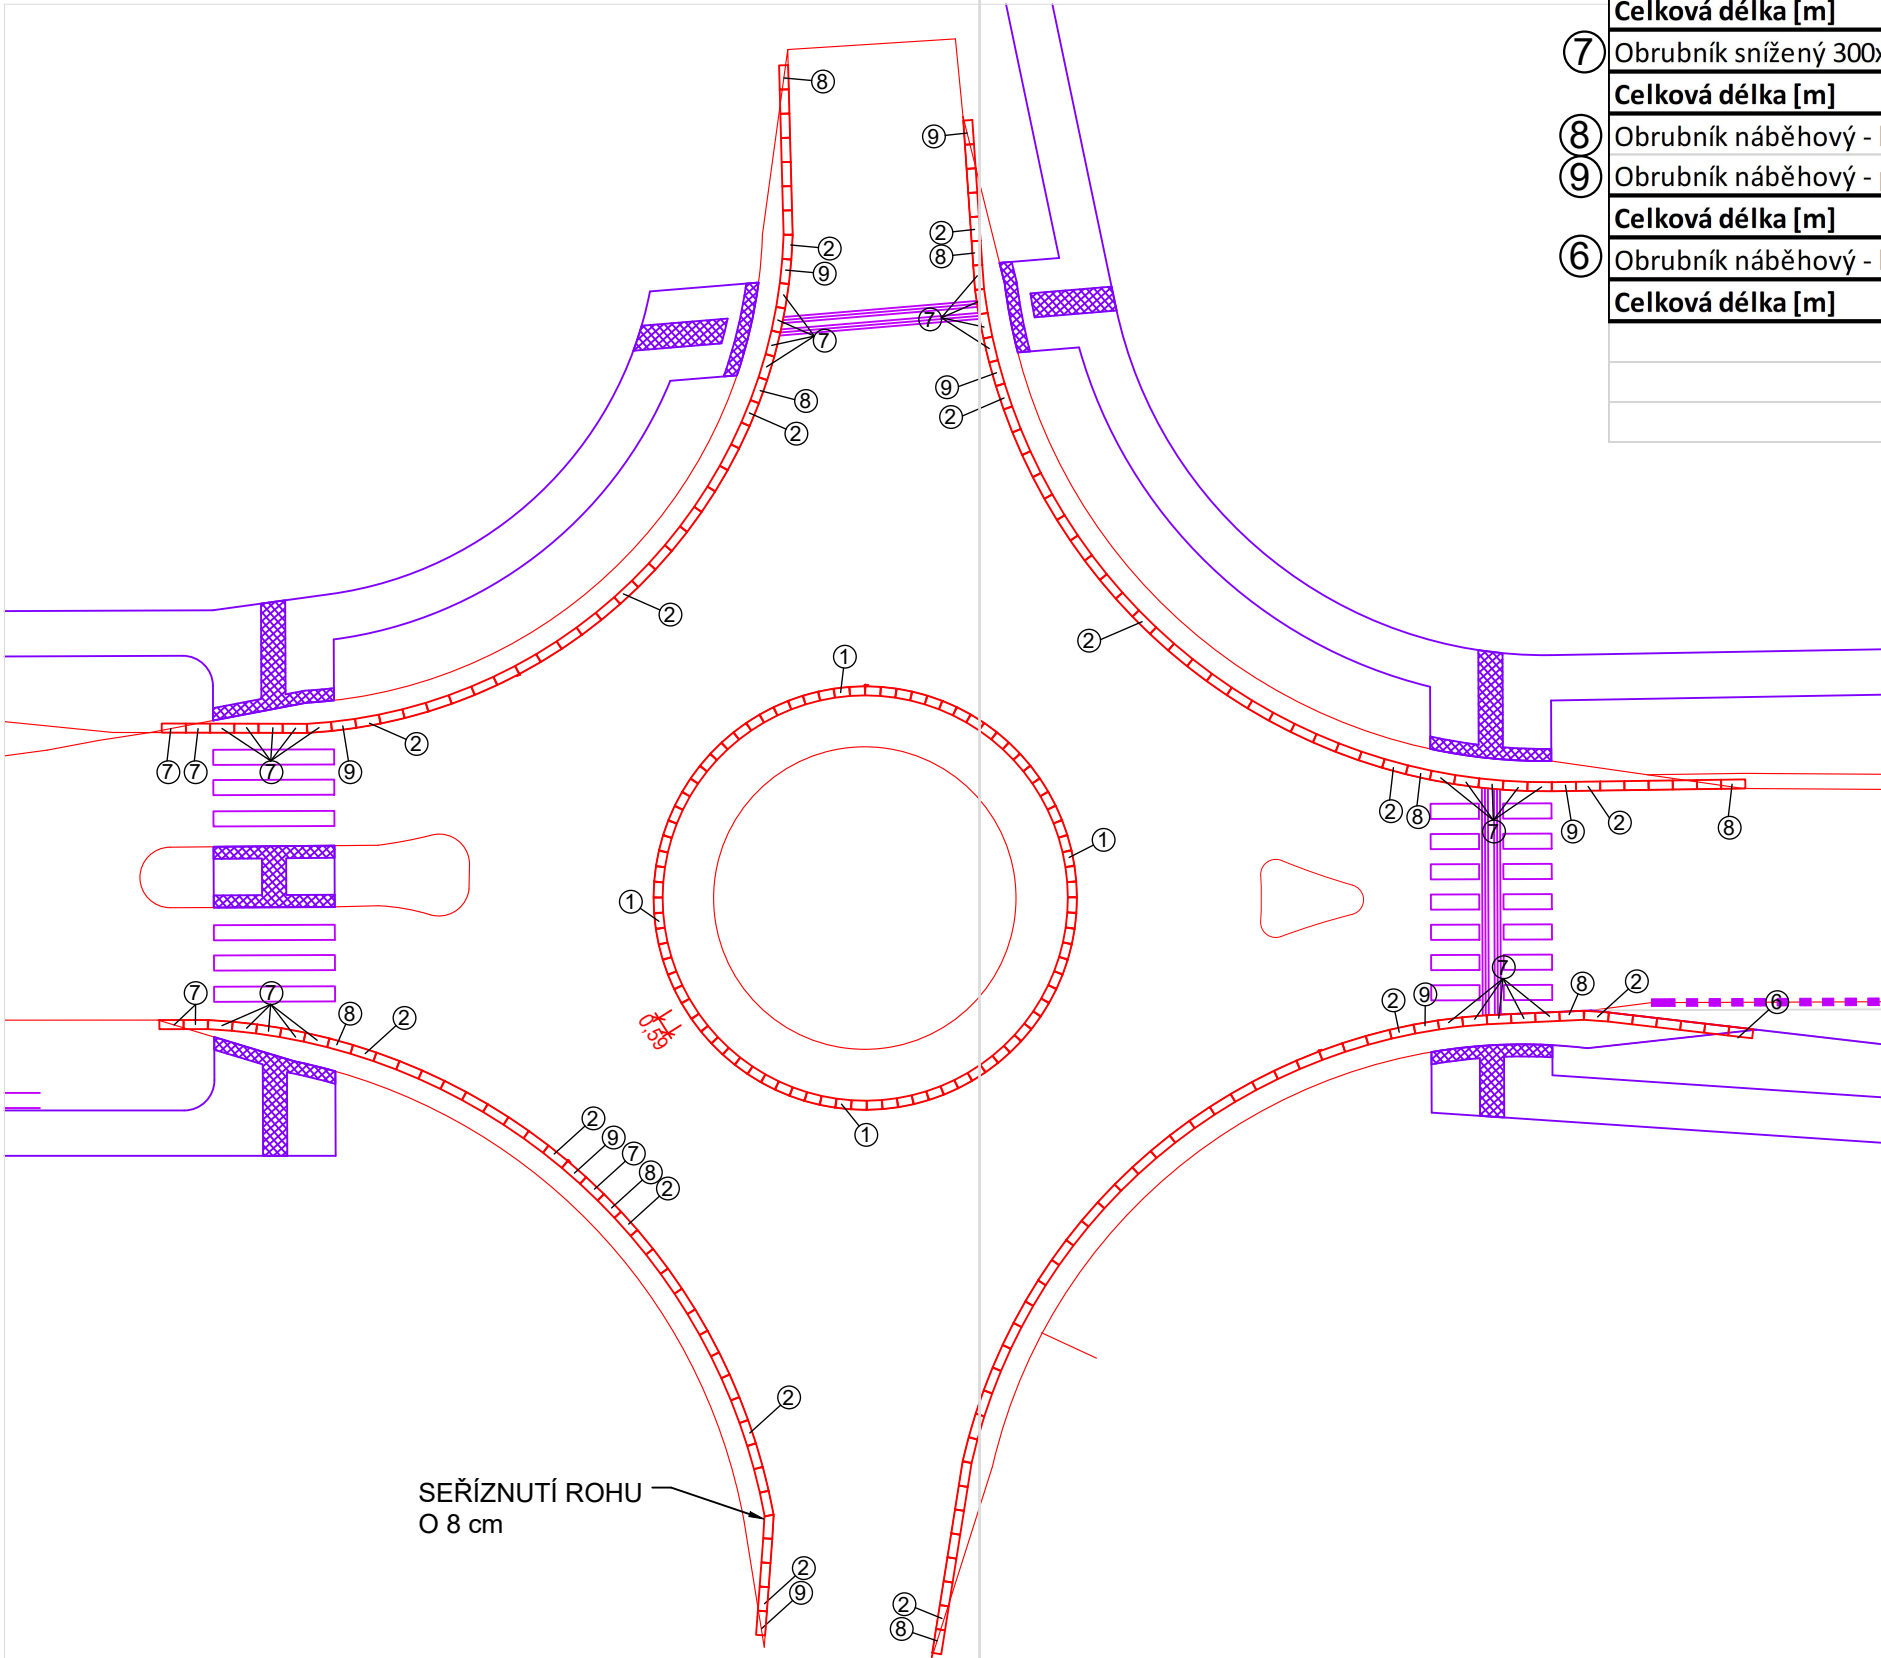


	Obrubník	délka [m]	rádius [m]	počet [ks]
①	Obrubník zkosený	0,50	přímá	83
②		0,59		1
		0,80		131
	Celková délka [m]	146,89		
⑦	Obrubník snížený 300x140	0,80	přímá	33
	Celková délka [m]	26,40		
⑧	Obrubník náběhový - levý 0-80mm	0,80	přímá	9
⑨	Obrubník náběhový - pravý 0-80mm			8
	Celková délka [m]	13,60		
⑥	Obrubník náběhový - levý 120-80mm	0,80	přímá	1
	Celková délka [m]	0,80		

SCHÉMA OBRUBNÍKŮ 1:25

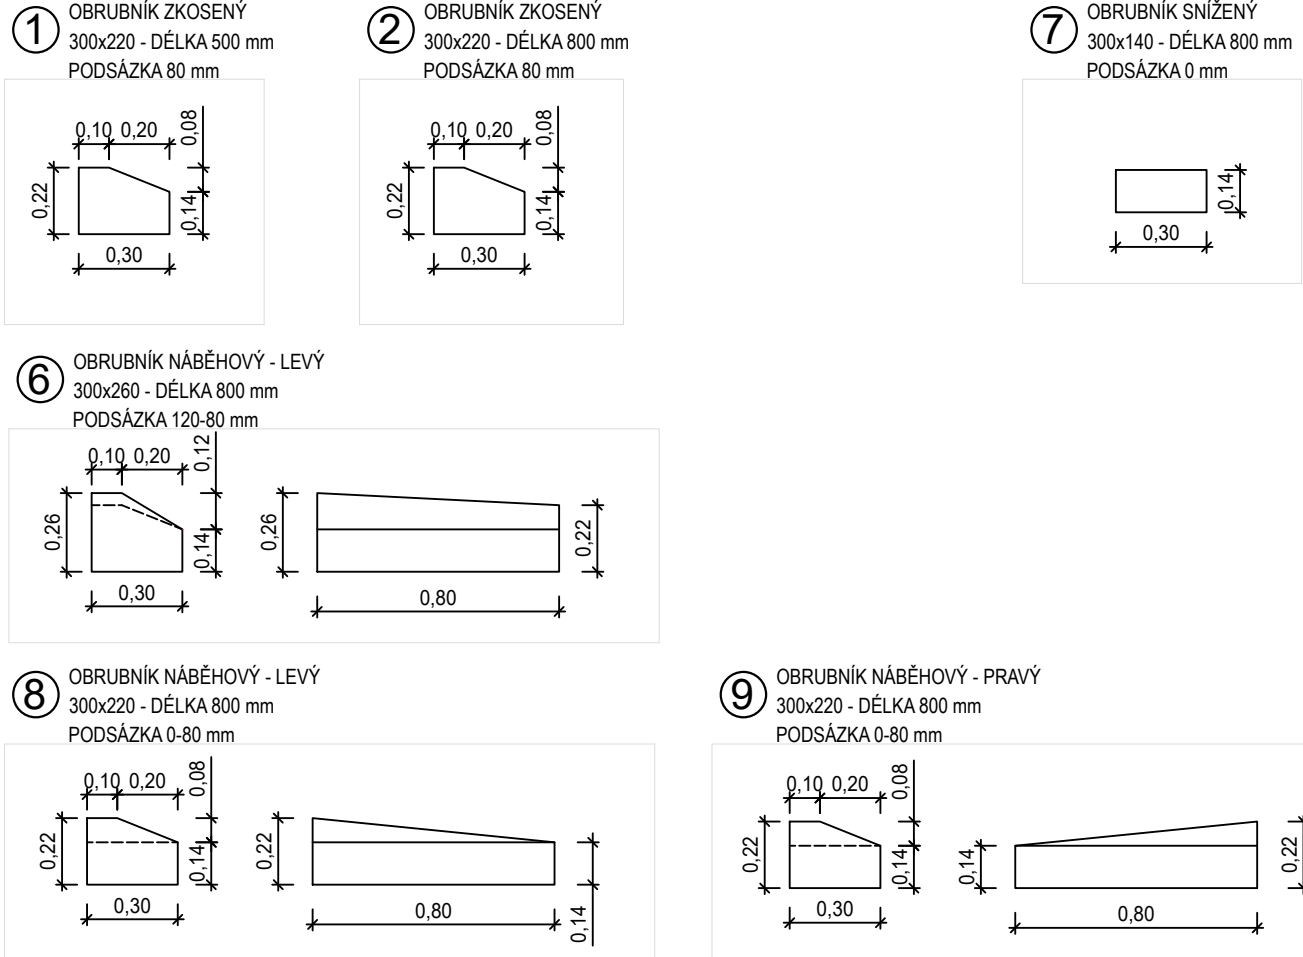


DETAIL SPÁR 1:10

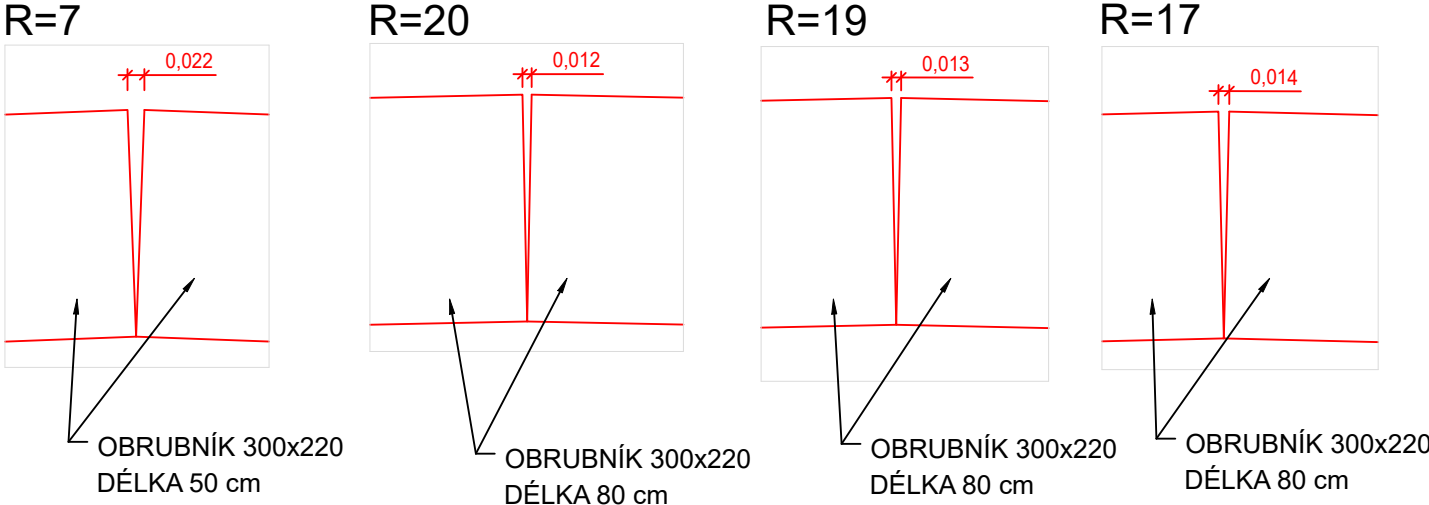

REVIZE:	PŘEDMĚT ZMĚNY:	DATUM:	VYPRACOVAL:
a			
b			
c			
NÁZEV STAVBY: II/603 SULICE - ŽELIVEC, REK. SILNICE A MOSTŮ		ČÍSLO OBJEKTU: SO 103	
INVESTOR STAVBY č.1:  KRAJSKÁ SPRÁVA A ÚDRŽBA SILNIC STŘEDOČESKÉHO KRAJE p.o. Zborovská 81/11, 150 21 Praha 5		RAZÍTKO: DATUM: PODPIS:	
INVESTOR STAVBY č.2:  OBEC KAMENICE Ringhofferovo náměstí 434 Olešovice, 251 68 Kamenice		RAZÍTKO: DATUM: PODPIS:	
TECHNICKÝ DOZOR INVESTORA  REALSTAV MB, s.r.o. Klaudíánova 124, 293 01 Mladá Boleslav		RAZÍTKO: KONTROLOVAL: DATUM: PODPIS:	
ZHOTOVITEL STAVBY:  M - SILNICE, a.s. Husova 1697, Bílé Předměstí, 530 03 Pardubice		RAZÍTKO: KONTROLOVAL: DATUM: PODPIS:	
KOORDINÁTOR RDS:  M - PROJEKCE, s.r.o. Resslova 956/13, 500 02 Hradec Králové		RAZÍTKO: KONTROLOVAL: DATUM: PODPIS:	

SOUŘADNICOVÝ SYSTÉM: S-JTSK
VÝŠKOVÝ SYSTÉM: B.P.V.

ČISTOPIS

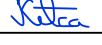NÁZEV STAVBY: II/603 SULICE - ŽELIVEC, REKONSTRUKCE SILNICE A MOSTŮ					
ČÁST / STAVEBNÍ OBJEKT: SO 103 - SILNICE II/603 ÚSEK 3 - OKRUŽNÍ KŘÍŽOVATKA					
PŘÍLOHA: KLADEČSKÝ PLÁN					
ZHOTOVITEL RDS:  M - PROJEKCE, s.r.o. Resslova 956/13 500 02 Hradec Králové	HLAVNÍ INŽENÝR PROJEKTU:	Bc. R. MĚSTECKÝ		PARÉ:	
	ZODPOVĚDNÝ PROJEKTANT:	Ing. M. STEJSKAL			
	VYPRACOVAL:	Bc. R. MĚSTECKÝ			
	KONTROLA:	Ing. P. KELČA			
	MĚŘÍTKO:	Č. ZAKÁZKY:	STUPEŇ:	DATUM:	ČÁST: PŘÍLOHA:
	1:250	25-118-03	RDS	06/2026	103 9