


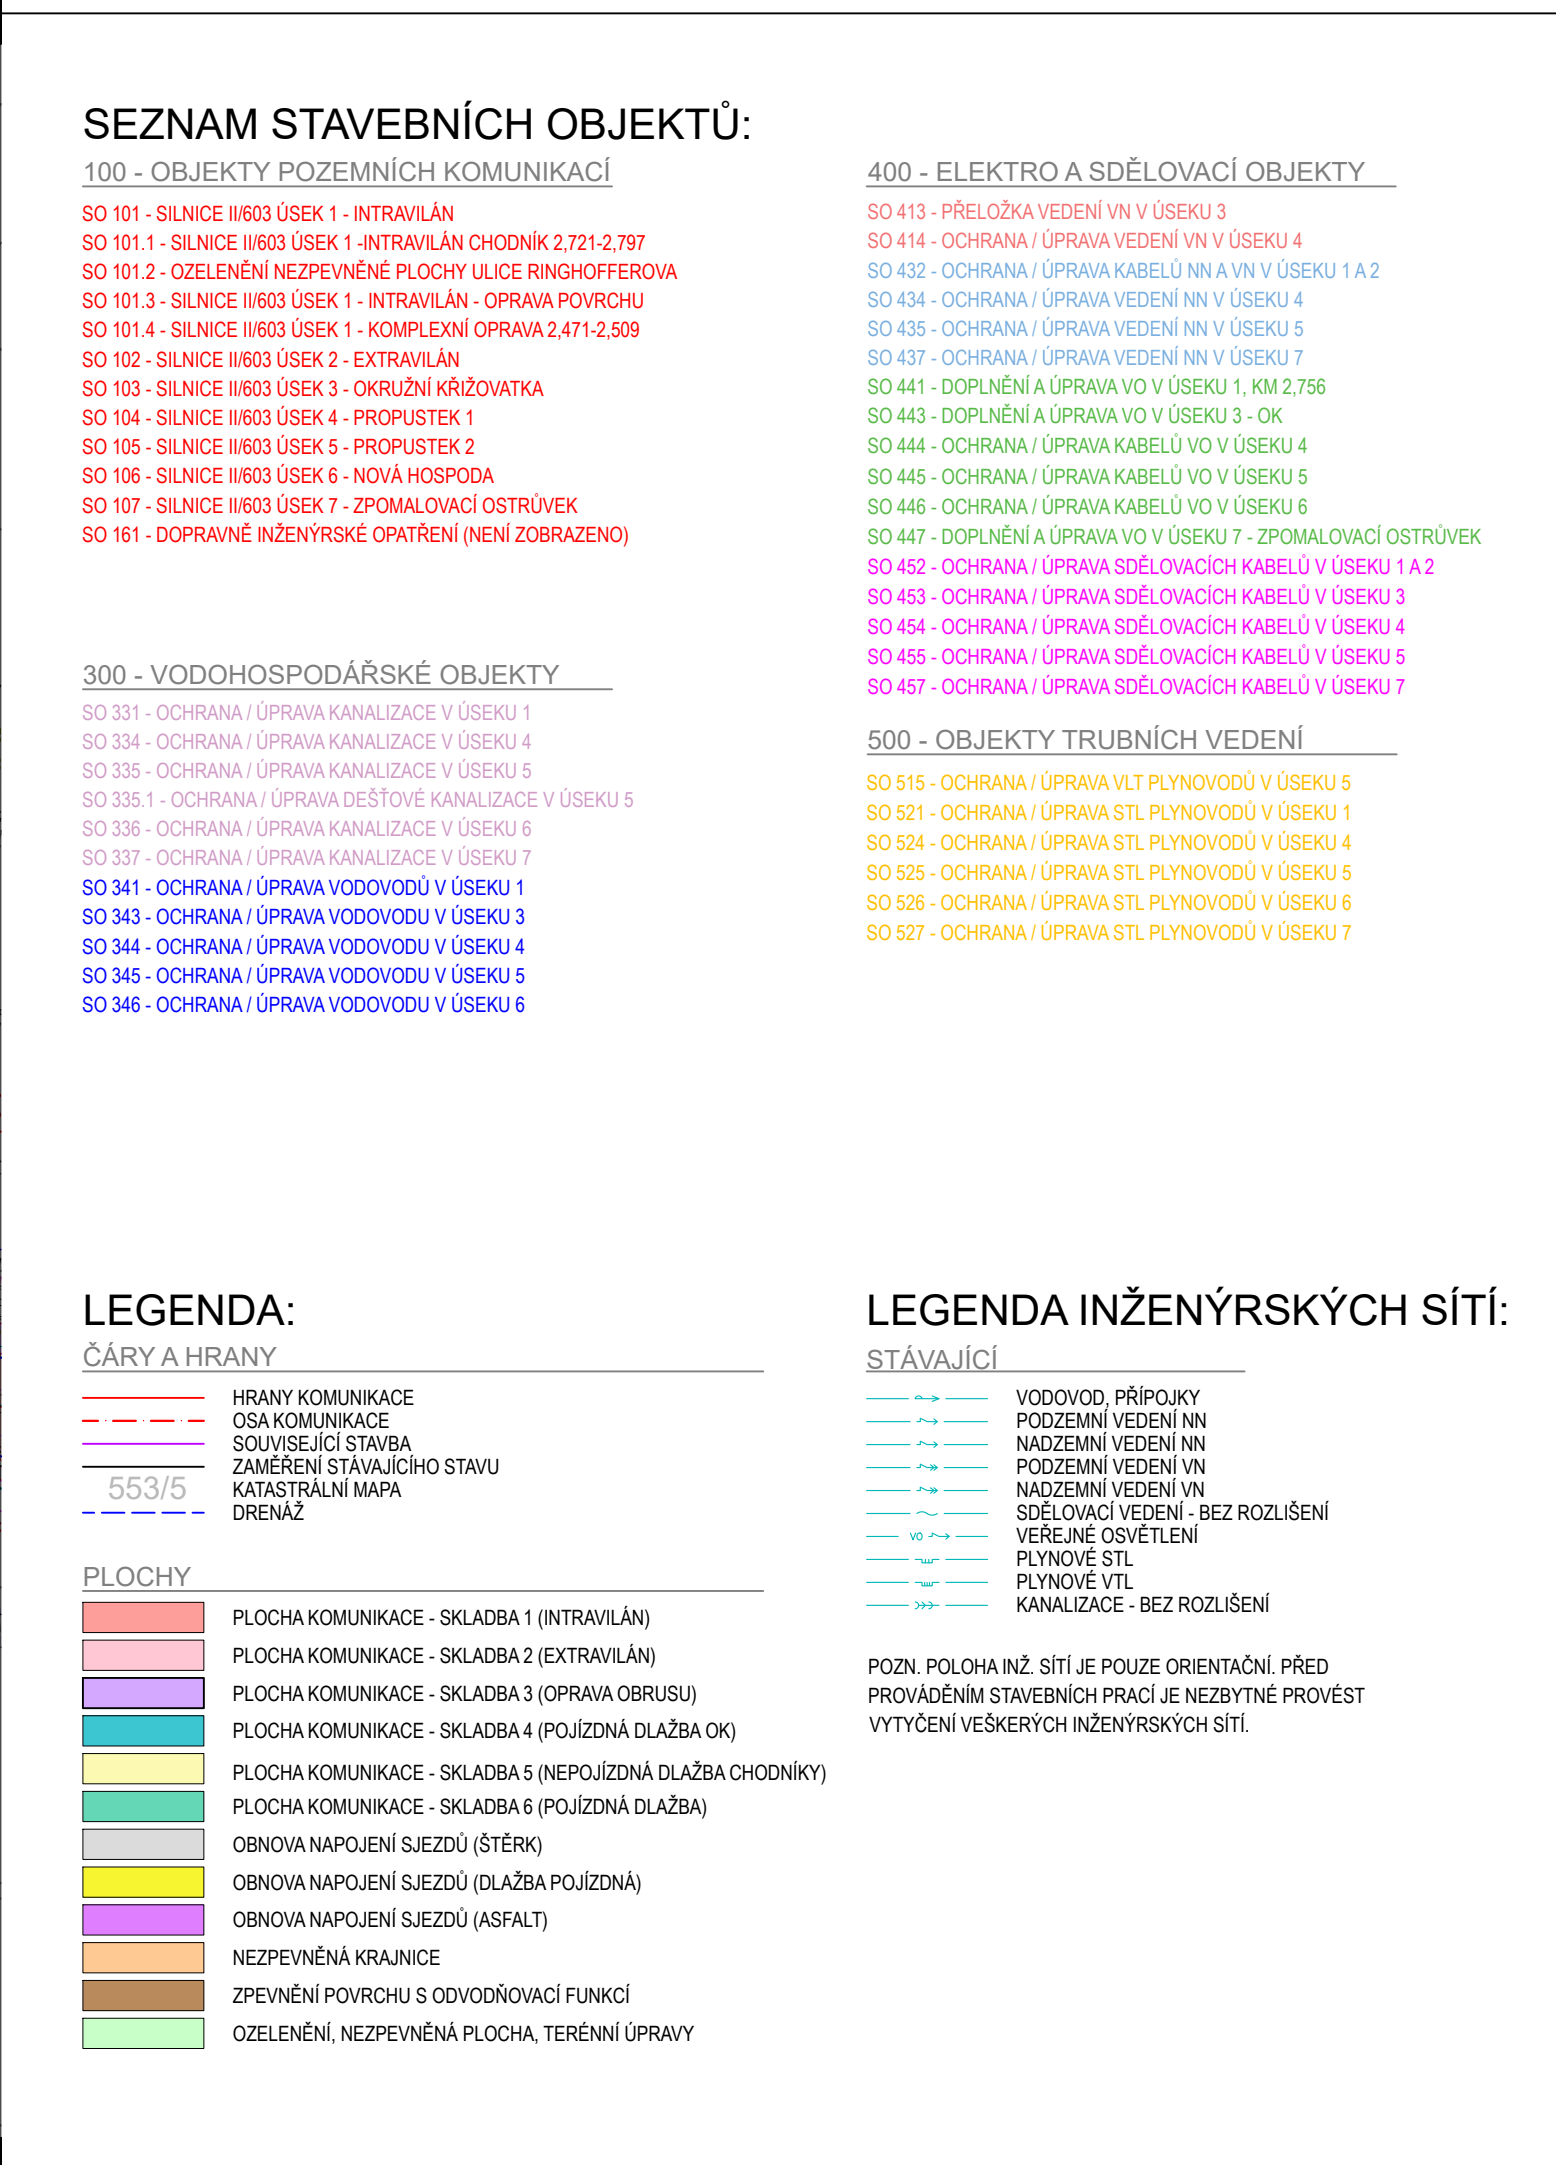

REVIZE:	PŘEDMĚT ZMĚNY:	DATUM:	VYPRACOVAL:
a			
b			
c			

NÁZEV STAVBY: II/603 SULICE - ŽELIVEC, REK. SILNICE A MOSTŮ	ČÍSLO OBJEKTU: SO 104
---	---------------------------------

INVESTOR STAVBY č.1:  KRAJSKÁ SPRÁVA A ÚDRŽBA SILNIC STŘEDOČESKÉHO KRAJE p.o. Zborovská 81/11, 150 21 Praha 5	RAZÍTKO: DATUM: PODPIS:
--	---

INVESTOR STAVBY č.2:  OBEC KAMENICE Ringhofferovo náměstí 434 Olešovice, 251 68 Kamenice	RAZÍTKO: DATUM: PODPIS:
--	---

TECHNICKÝ DOZOR INVESTORA  REALSTAV MB, s.r.o. Klaudánova 124, 293 01 Mladá Boleslav	RAZÍTKO: KONTROLOVAL: DATUM: PODPIS:
---	---

ZHOTOVITEL STAVBY:  M - SILNICE, a.s. Husova 1697, Bílé Předměstí, 530 03 Pardubice	RAZÍTKO: KONTROLOVAL: DATUM: PODPIS:
--	---

KOORDINÁTOR RDS:  M - PROJEKCE, s.r.o. Resslova 956/13, 500 02 Hradec Králové	RAZÍTKO: KONTROLOVAL: DATUM: PODPIS:
--	---

SOUŘADNICOVÝ SYSTÉM: S-JTSK
VÝŠKOVÝ SYSTÉM: B.P.V.

ČISTOPIS

NÁZEV STAVBY: II/603 SULICE - ŽELIVEC, REKONSTRUKCE SILNICE A MOSTŮ							
ČÁST / STAVEBNÍ OBJEKT: SO 104 - SILNICE II/603 ÚSEK 4 - PROPUSTEK 1							
PŘÍLOHA: SITUACE STAVBY (KM 2,350 - 2,460)							
 M - PROJEKCE, s.r.o. Resslova 956/13 500 02 Hradec Králové	HLAVNÍ INŽENÝR PROJEKTU:		Bc. R. MĚSTECKÝ			PARÉ:	
	ZODPOVĚDNÝ PROJEKTANT:		Ing. M. STEJSKAL				
	VYPRACOVAL:		Ing. M. ŠPRONGL				
	KONTROLA:		Ing. P. KELČA				
	MĚŘÍTKO:	Č. ZAKÁZKY:	STUPEŇ:	DATUM:	ČÁST:	PŘÍLOHA:	
1:500, 1:250	25-118-03	RDS	06/2026	104	2		