

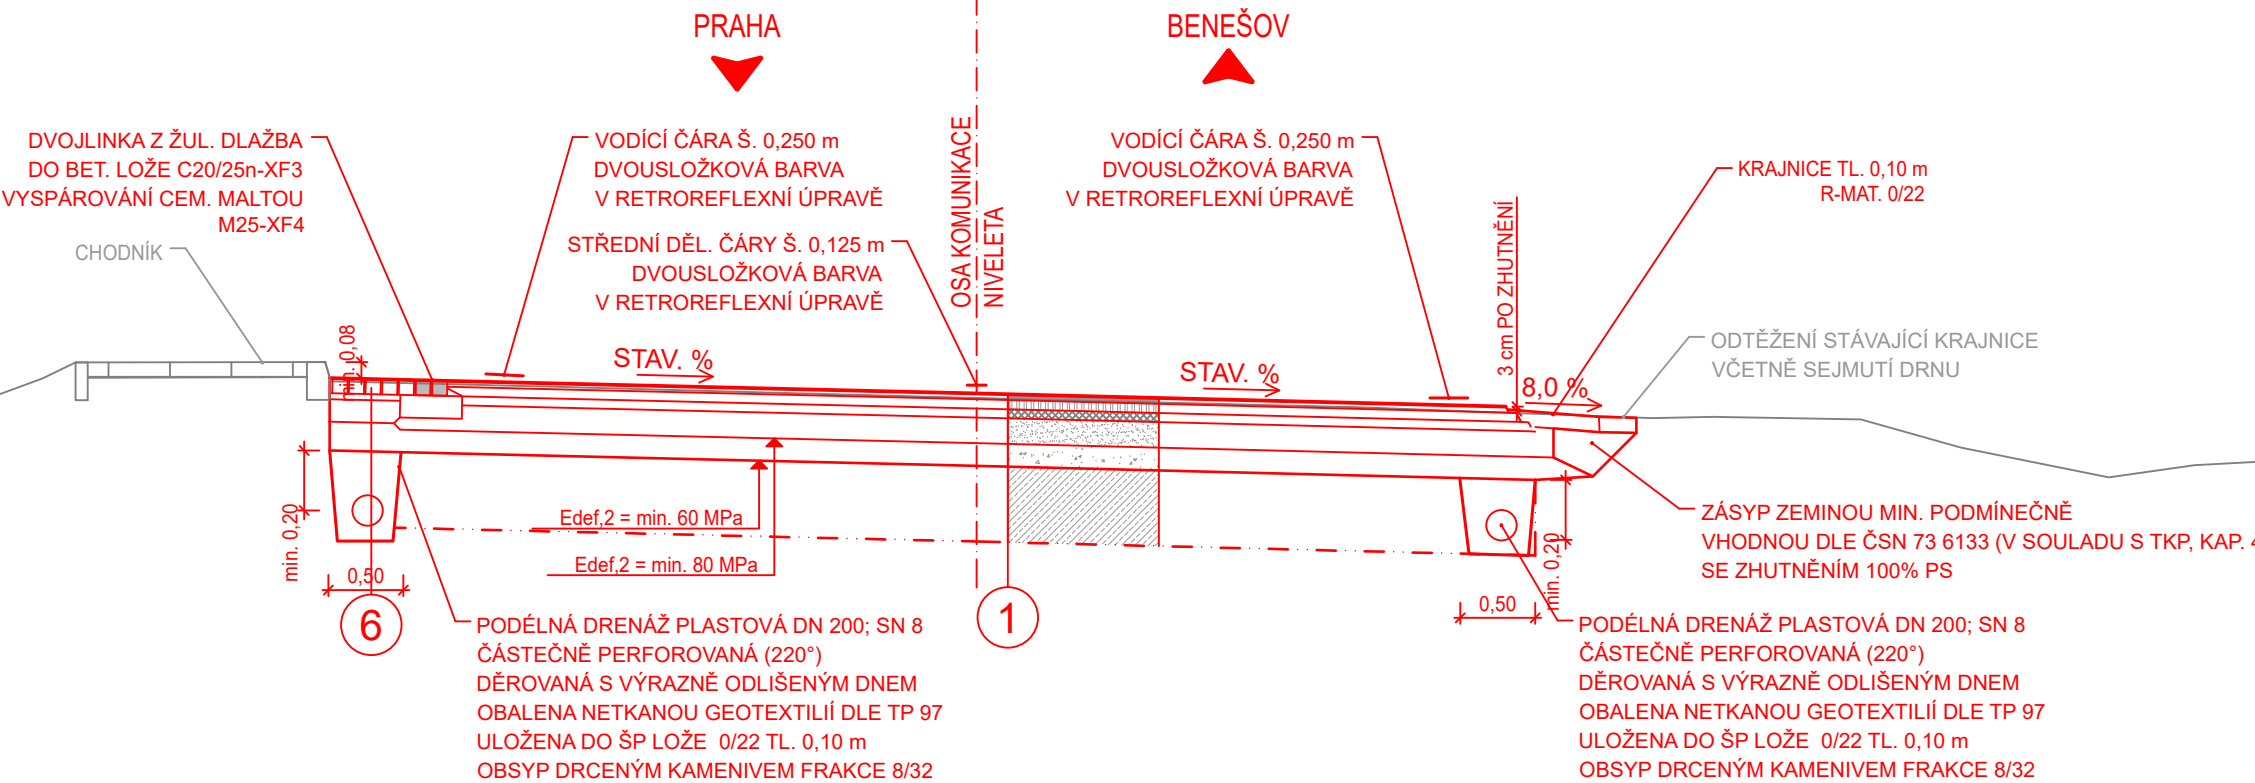
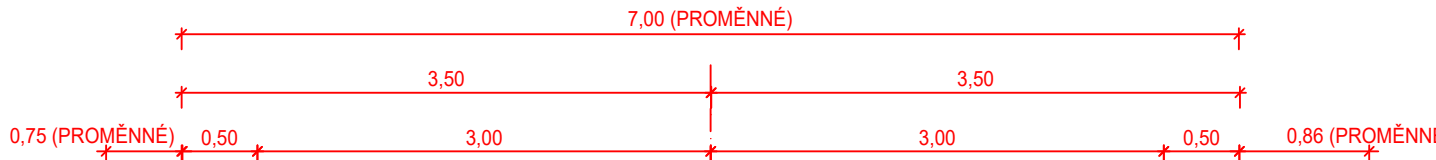


SO 104 - Silnice II/603 M - 1:50 $\approx$ MS2 -/8/50 odvozená
(Skladba č.1) intravilán + stávající chodník (km 2,434 08)

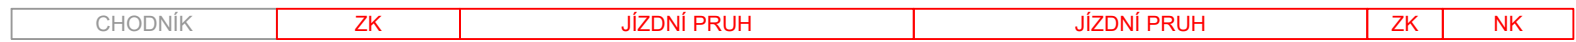

V místě s novým chodníkem

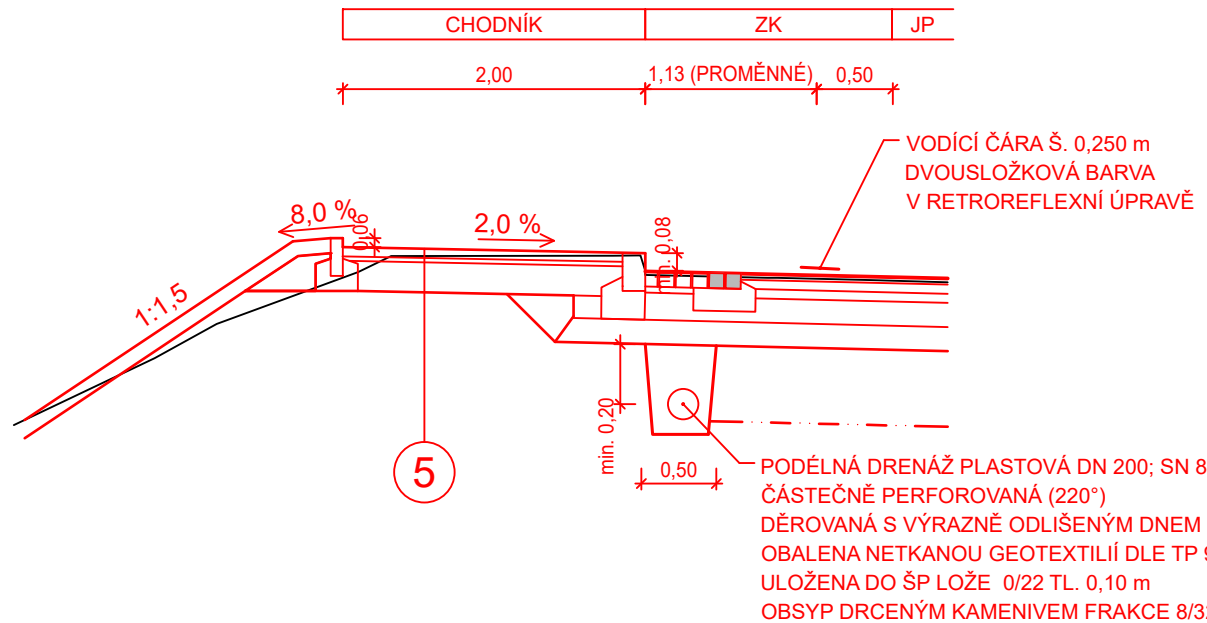

- **POZNÁMKY:**
 - AKTIVNÍ ZÓNA JE NAVRŽENA Z UPRAVENÝCH ZEMIN V PODLOŽÍ – PŘEDPOKLAD VYUŽITÍ STÁVAJÍCÍ KONSTRUKCE S PŘIDÁNÍM HYDRAULICKÉHO POJIVA NA TLOUŠŤKU 500 mm (ZÁVISÍ NA ZASTIŽENÝCH VLASTNOSTECH PARAPLÁNĚ AZ) NEBO VÝMĚNA PODLOŽÍ S VYUŽITÍM STÁVAJÍCÍCH ODTĚŽENÝCH VRSTEV S PAU A ULOŽENÝCH TECHNOLOGIÍ RECYKLACE ZA STUDENA. JEDNÁ SE O STÁVAJÍCÍ ZEMINY PODMÍNĚNĚ VHDNÉ, KTERÉ JE MOŽNO POVAŽOVAT DLE TP 170 PŘI HODNOTĚ CBR < 15 % ZA TP III PŘI OPTIMÁLNÍCH PODMÍNKÁCH VLHKOSTI NEBO UPRAVOU ZEMIN AZ S HYDRAULICKÝM POJIVEM MIB. PIII A PŘI DOSAŽENÍ VÝŠŠÍHO CBR 30 % ZA TP II.
 - ODTĚŽENÉ VRSTVY VOZOVÉK S OBSAHEM PAU LZE POUŽÍT V SOULADU S VYHLÁŠKOU 283/2023 SB. DO AKTIVNÍ ZÓNY, POKUD BUDOU ULOŽENY DLE TP 208 TECHNOLOGIÍ RECYKLACE ZA STUDENA V MAX. TL. 250 mm.

- | | | | |
|-------------------|---------------------------|------------------------------|------------------------------------|
| 1 | SKLADBA KONSTRUKCE Č. 1 | | |
| | ASF. BETON OBRUSNÝ MODIF. | ACO 11+ PMB 45/80-65 | 40 mm ČSN 73 6121 |
| | SPOJOVACÍ POSTŘÍK MODIF. | PS-CP | 0,40 kg/m ² ČSN 73 6129 |
| | ASF. BETON LOŽNÍ MODIF. | ACL 22S PMB 25/55-65 | 60 mm ČSN 73 6121 |
| | SPOJOVACÍ POSTŘÍK MODIF. | PS-CP | 0,40 kg/m ² ČSN 73 6129 |
| | VYROVNÁVACÍ VRSTVA | ACP 16S 50/70 | 60 mm ČSN 73 6121 |
| | RECYKLACE | RS CA 0/32 (0/45) | 170 mm ČSN 736147 |
| | ŠTÉRKODRŤ | ŠDa 0/32 GE | 150 mm ČSN 736126-1 |
| KONSTRUKCE CELKEM | | 480 mm | |
| FRÉZOVÁNÍ | | -100 mm | |
| NAVÝŠENÍ NIVELETY | | ±30 mm DLE POĐELNÉHO PROFILU | |

- POZNÁMKY:**
- POSTŘÍKY JSOU UVEDENY V MNOŽSTVÍ ZBYTKOVÉHO POJIVA.
 - Edef = min. 60 MPa CBR sat. 30%
 - AKTIVNÍ ZÓNA (zeminy v podloží stávající konstrukce s přidáním hydraulického pojiva nebo kameniva z odtěžených vrstev vozovky) tl. 500 mm

- | | | | |
|---|--------------------------------------|-------------|----------------------|
| 5 | SKLADBA KONSTRUKCE Č.3 | | |
| | BETONOVÁ NEBO KAMENNÁ DLAŽBA | DL | 60 mm ČSN 73 6131 |
| | LOŽE (DROBNÉ DRCENÉ KAMENIVO 4-8 MM) | L 4/8 | 30 mm ČSN 73 6126-1 |
| | ŠTĚRKODRŤ | ŠDb 0/32 Gn | 150 mm ČSN 73 6126-1 |
| | KONSTRUKCE CELKEM | | 240 mm |

- | | | | |
|---|--------------------------------------|-------------|----------------------|
| 6 | SKLADBA KONSTRUKCE Č.2 | | |
| | KAMENNÁ DLAŽBA POJIZDNÁ | DL | 100 mm ČSN 73 6131 |
| | LOŽE (DROBNÉ DRCENÉ KAMENIVO 4-8 MM) | L 4/8 | 40 mm ČSN 73 6131 |
| | ŠTĚRKODŘŤ | ŠDa 0/32 GE | 150 mm ČSN 73 6126-1 |
| | ŠTĚRKODŘŤ | ŠDa 0/32 GE | 190 mm ČSN 73 6126-1 |
| | KONSTRUKCE CELKEM | | 480 mm |

- POZNÁMKY:**
- Edef = min. 60 MPa CBR sat. 30%

REVIZE:	PŘEDMĚT ZMĚNY:	DATUM:	VYPRACOVAL:
a			
b			
c			

NÁZEV STAVBY: II/603 SULICE - ŽELIVEC, REK. SILNICE A MOSTŮ	ČÍSLO OBJEKTU: SO 104
--	--------------------------

INVESTOR STAVBY č.1:	RAŽITKO:
 KRAJSKÁ SPRÁVA A ÚDRŽBA SILNIC STŘEDOČESKÉHO KRAJE p.o. Zborovská 81/11, 150 21 Praha 5	DATUM: _____ PODPIS: _____

INVESTOR STAVBY č.2:  OBEC KAMENICE Ringhofferovo náměstí 434 Olešovice, 251 68 Kamenice	RAŽÍTKO: DATUM: _____ PODPIS: _____
--	---

TECHNICKÝ DOZOR INVESTORA REALSTAV MB, spol. s r.o. REALSTAV MB, s.r.o. Klaudiánova 124, 293 01 Mladá Boleslav	RAŽÍTKO: KONTROLOVAL: DATUM: PODPIS:
---	--

ZHOTOVITEL STAVBY:  M - SILNICE, a.s. Husova 1697, Bílé Předměstí, 530 03 Pardubice	RAŽÍTKO: KONTROLOVAL: DATUM: PODPIS:
---	--

KOORDINÁTOR RDS:  M - PROJEKCE , s.r.o. Resslova 956/13, 500 02 Hradec Králové	RAZÍTKO: KONTROLOVAL: DATUM: PODPIS:
--	---

SOUŘADNICOVÝ SYSTÉM: S-JTSK

VÝŠKOVÝ SYSTÉM: B.P.V.

ČISTOPIS

NÁZEV STAVBY:	II/603 SULICE - ŽELIVEC, REKONSTRUKCE SILNICE A MOSTŮ
---------------	---

ČAST / STAVEBNÍ OBJEKT: SO 104 - SILNICE II/603 ÚSEK 4 - PROPUSTEK 1

VZOROVÉ PŘÍČNÉ ŘEZY							
ZHOTOVITEL RDS:		HLAVNÍ INŽENÝR PROJEKTU: Bc. R. MĚSTECKÝ		<i>Městecký</i>		PARÉ:	
		ZODPOVĚDNÝ PROJEKTANT: Ing. M. STEJSKAL		<i>Skus</i>			
		VYPRACOVAL: Ing. M. ŠPRONGL		<i>Šprongl</i>			
		KONTROLA: Ing. P. KELČA		<i>Kelča</i>			
M - PROJEKCE, s.r.o. Resslova 956/13 500 02 Hradec Králové							
MĚŘÍTKO: 1:50 Č. ZAKÁZKY: 25-118-03 STUPEŇ: RDS DATUM: 06/2026 ČÁST: 104 PŘÍLOHA: 4							