



SO 104 - CHARAKTERISTICKÉ ŘEZY
M 1:100


2,360000

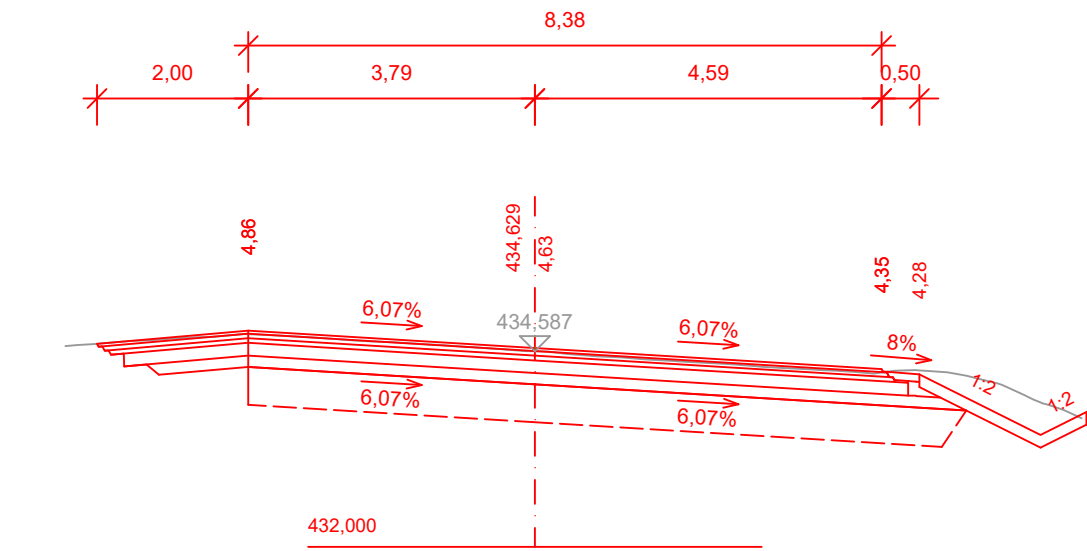


2,380000

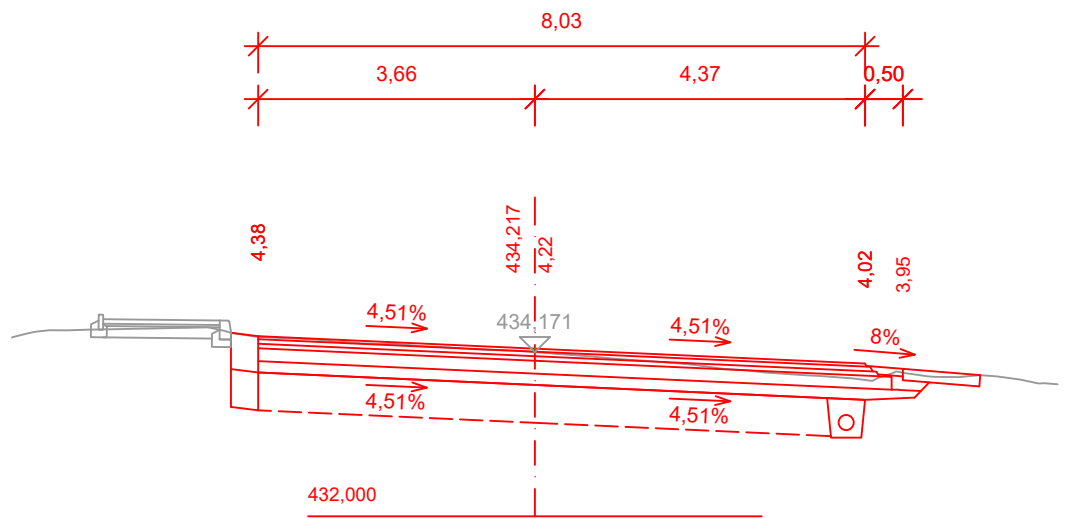


2,400000

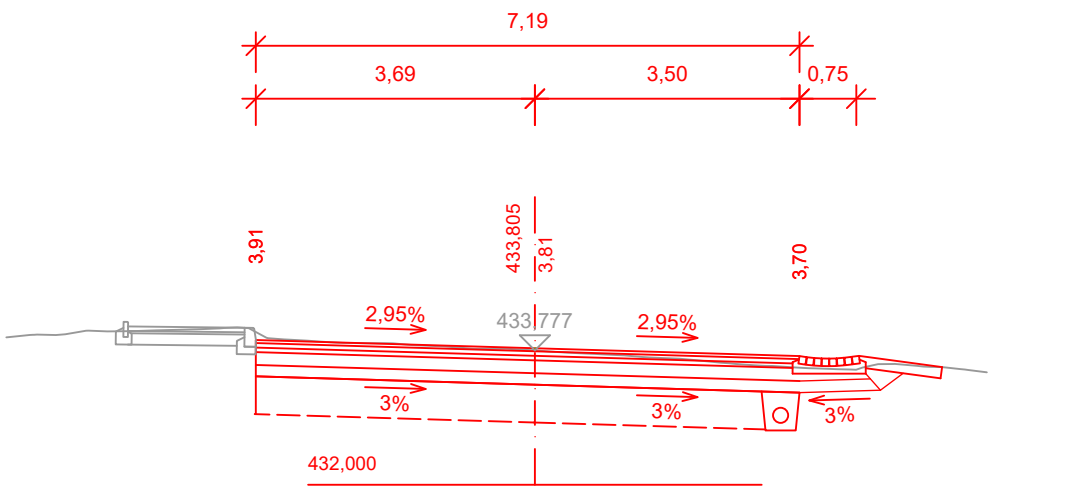


2,420000

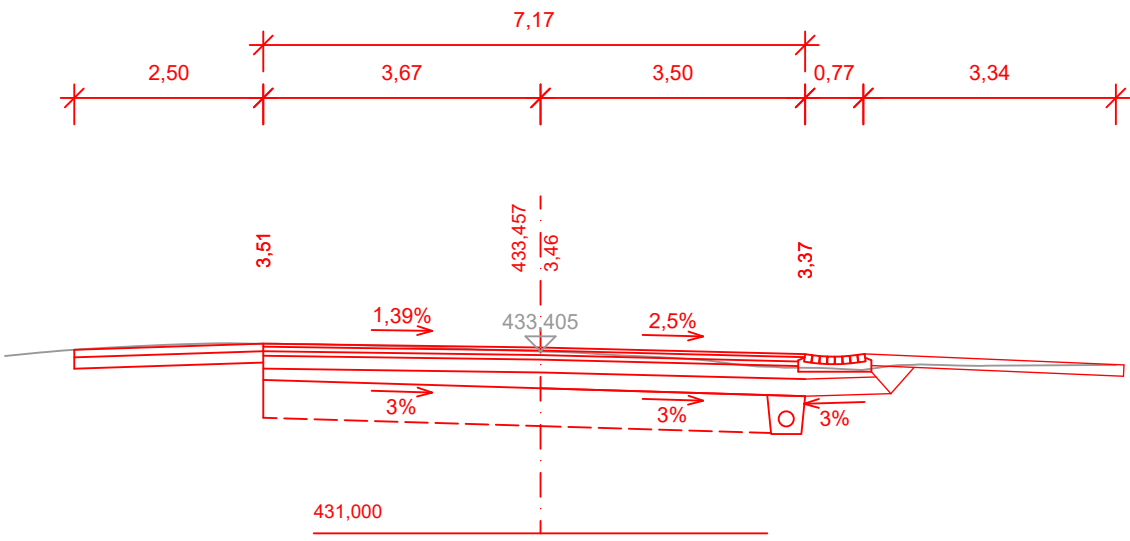

2,440000

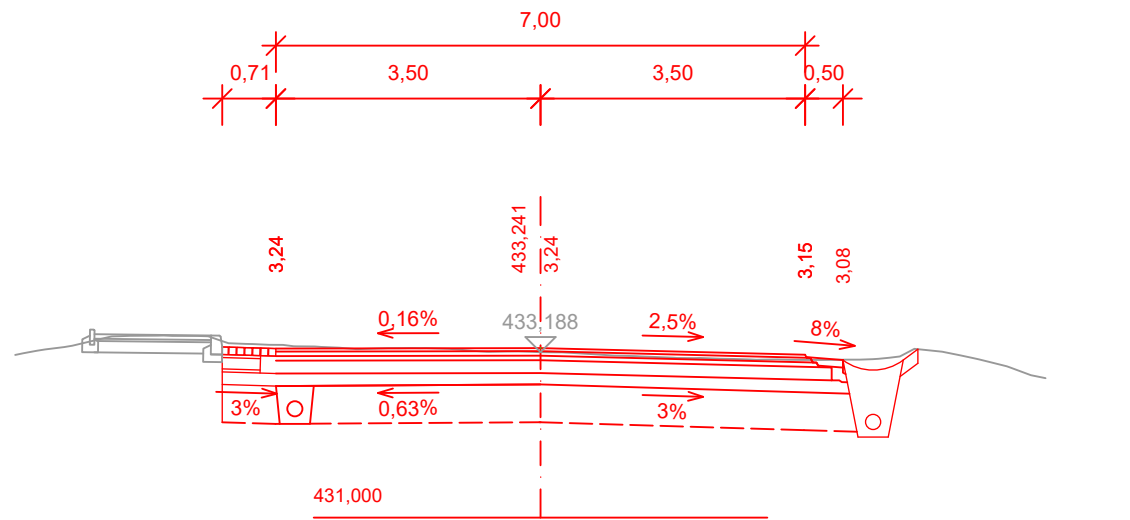

2,460000

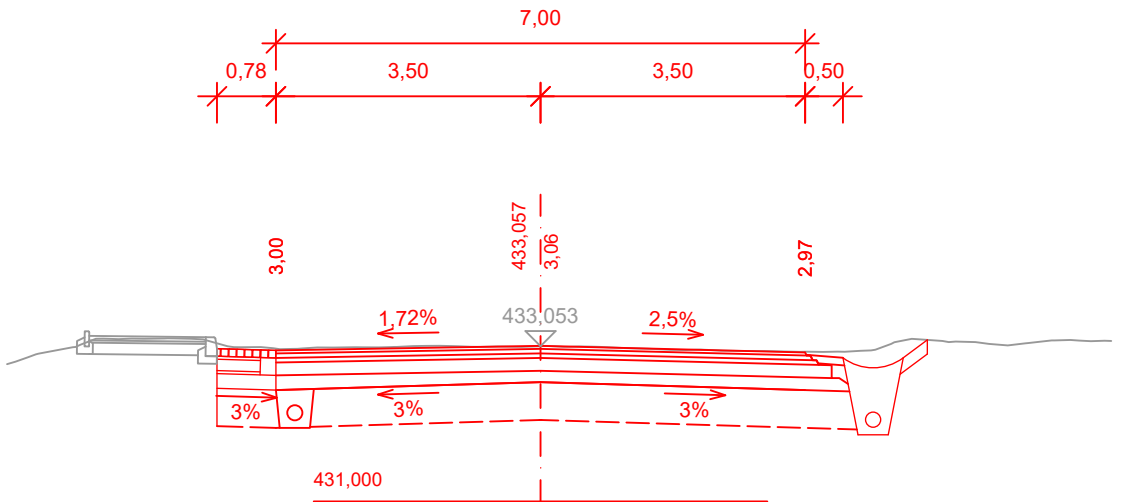

REVIZE:	PŘEDMĚT ZMĚNY:	DATUM:	VYPRACOVAL:
a			
b			
c			

NÁZEV STAVBY: II/603 SULICE - ŽELIVEC, REK. SILNICE A MOSTŮ	ČÍSLO OBJEKTU: SO 104
--	--------------------------

INVESTOR STAVBY č.1:  KRAJSKÁ SPRÁVA A ÚDRŽBA SILNIC STŘEDOČESKÉHO KRAJE p.o. Zborovská 81/11, 150 21 Praha 5	RAZÍTKO: DATUM: PODPIS:
---	--------------------------------

INVESTOR STAVBY č.2:  OBEC KAMENICE Ringhofferovo náměstí 434 Olešovice, 251 68 Kamenice	RAZÍTKO: DATUM: PODPIS:
--	--------------------------------

TECHNICKÝ DOZOR INVESTORA  REALSTAV MB, spol. s r.o. Klaudíanova 124, 293 01 Mladá Boleslav	RAZÍTKO: KONTROLOVAL: DATUM: PODPIS:
--	--

ZHOTOVITEL STAVBY:  M - SILNICE, a.s. Husova 1697, Bílé Předměstí, 530 03 Pardubice	RAZÍTKO: KONTROLOVAL: DATUM: PODPIS:
--	--

KOORDINÁTOR RDS:  M - PROJEKCE, s.r.o. Resslova 956/13, 500 02 Hradec Králové	RAZÍTKO: KONTROLOVAL: DATUM: PODPIS:
--	--

SOUŘADNICOVÝ SYSTÉM: S-JTSK

VÝŠKOVÝ SYSTÉM: B.P.V.

ČISTOPIS

NÁZEV STAVBY: II/603 SULICE - ŽELIVEC, REKONSTRUKCE SILNICE A MOSTŮ
--

ČÁST / STAVEBNÍ OBJEKT: SO 104 - SILNICE II/603 ÚSEK 4 - PROPUSTEK 1

PŘÍLOHA: CHARAKTERISTICKÉ PŘÍČNÉ ŘEZY
--

ZHOTOVITEL RDS:  M - PROJEKCE, s.r.o. Resslova 956/13 500 02 Hradec Králové	HLAVNÍ INŽENÝR PROJEKTU: Bc. R. MĚSTECKÝ ZODPOVĚDNÝ PROJEKTANT: Ing. M. STEJSKAL VYPRACOVAL: Bc. R. MĚSTECKÝ KONTROLA: Ing. P. KELČA MĚŘÍTKO: 1:100 Č. ZAKÁZKY: 25-118-03 STUPEŇ: RDS DATUM: 06/2026 ČÁST: 104 PŘÍLOHA: 5	PARÉ:    
---	--	---