




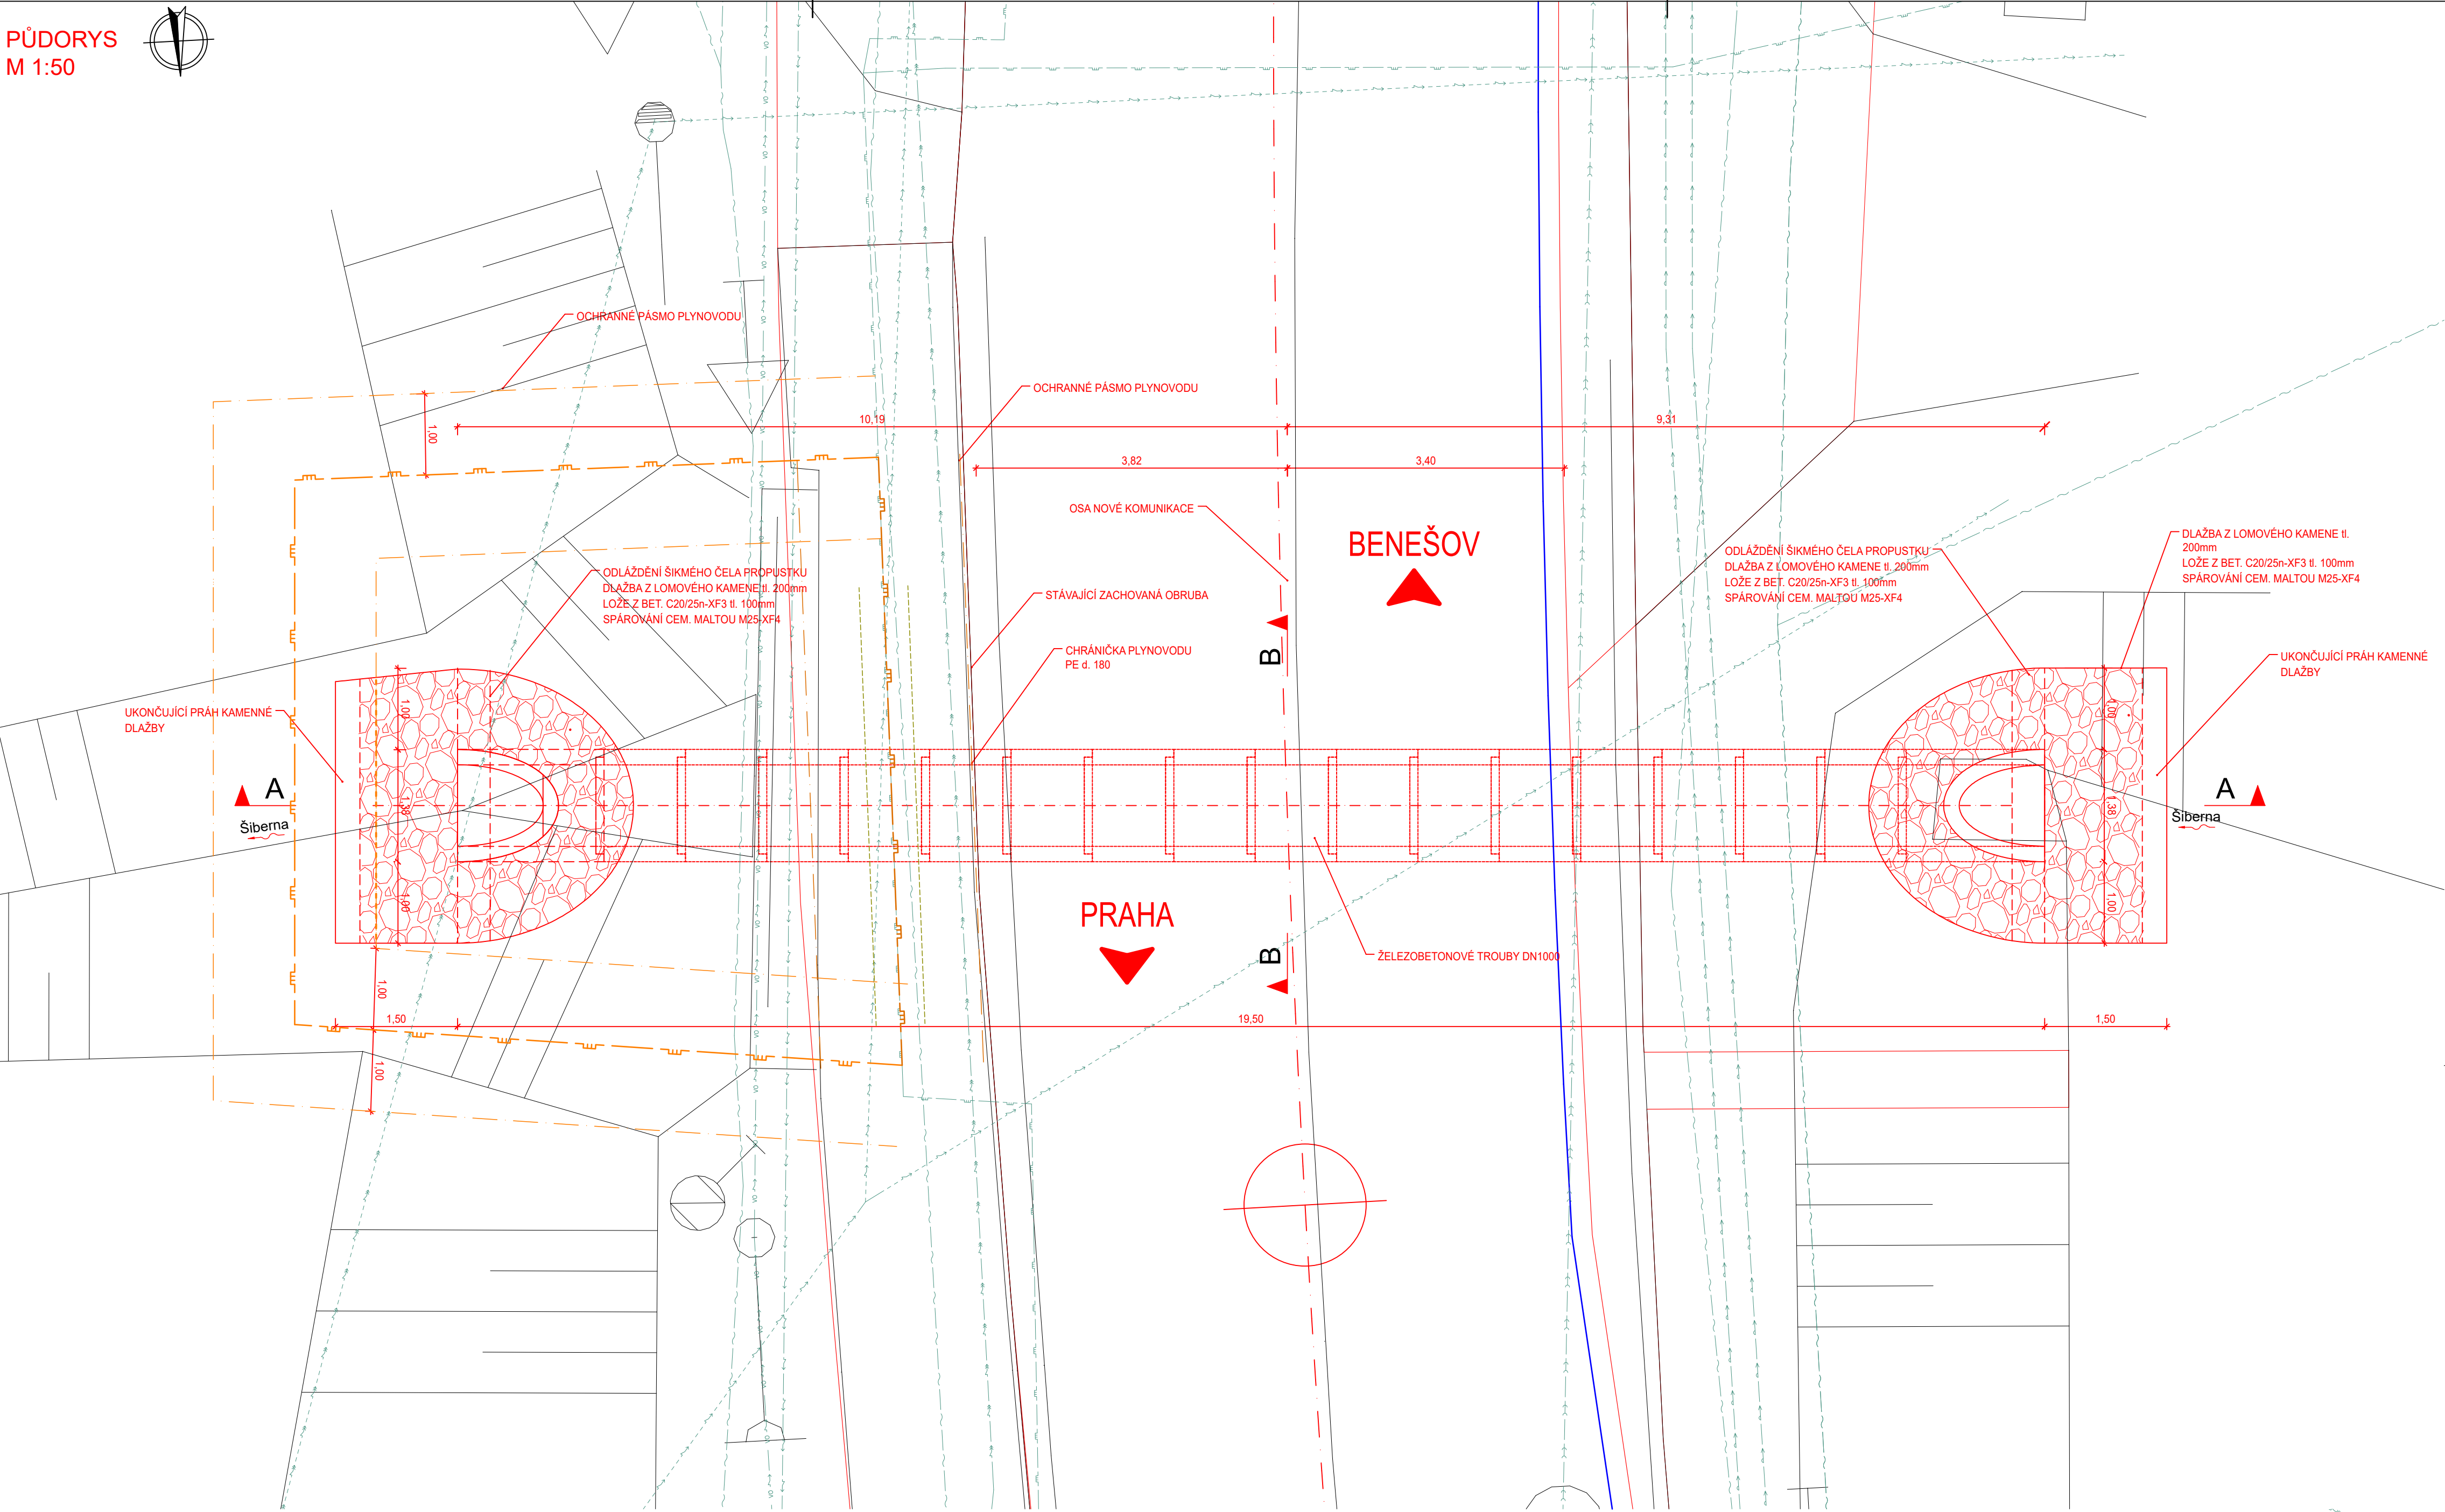

PODÉLNÝ ŘEZ PROPUSTKU
M 1:50

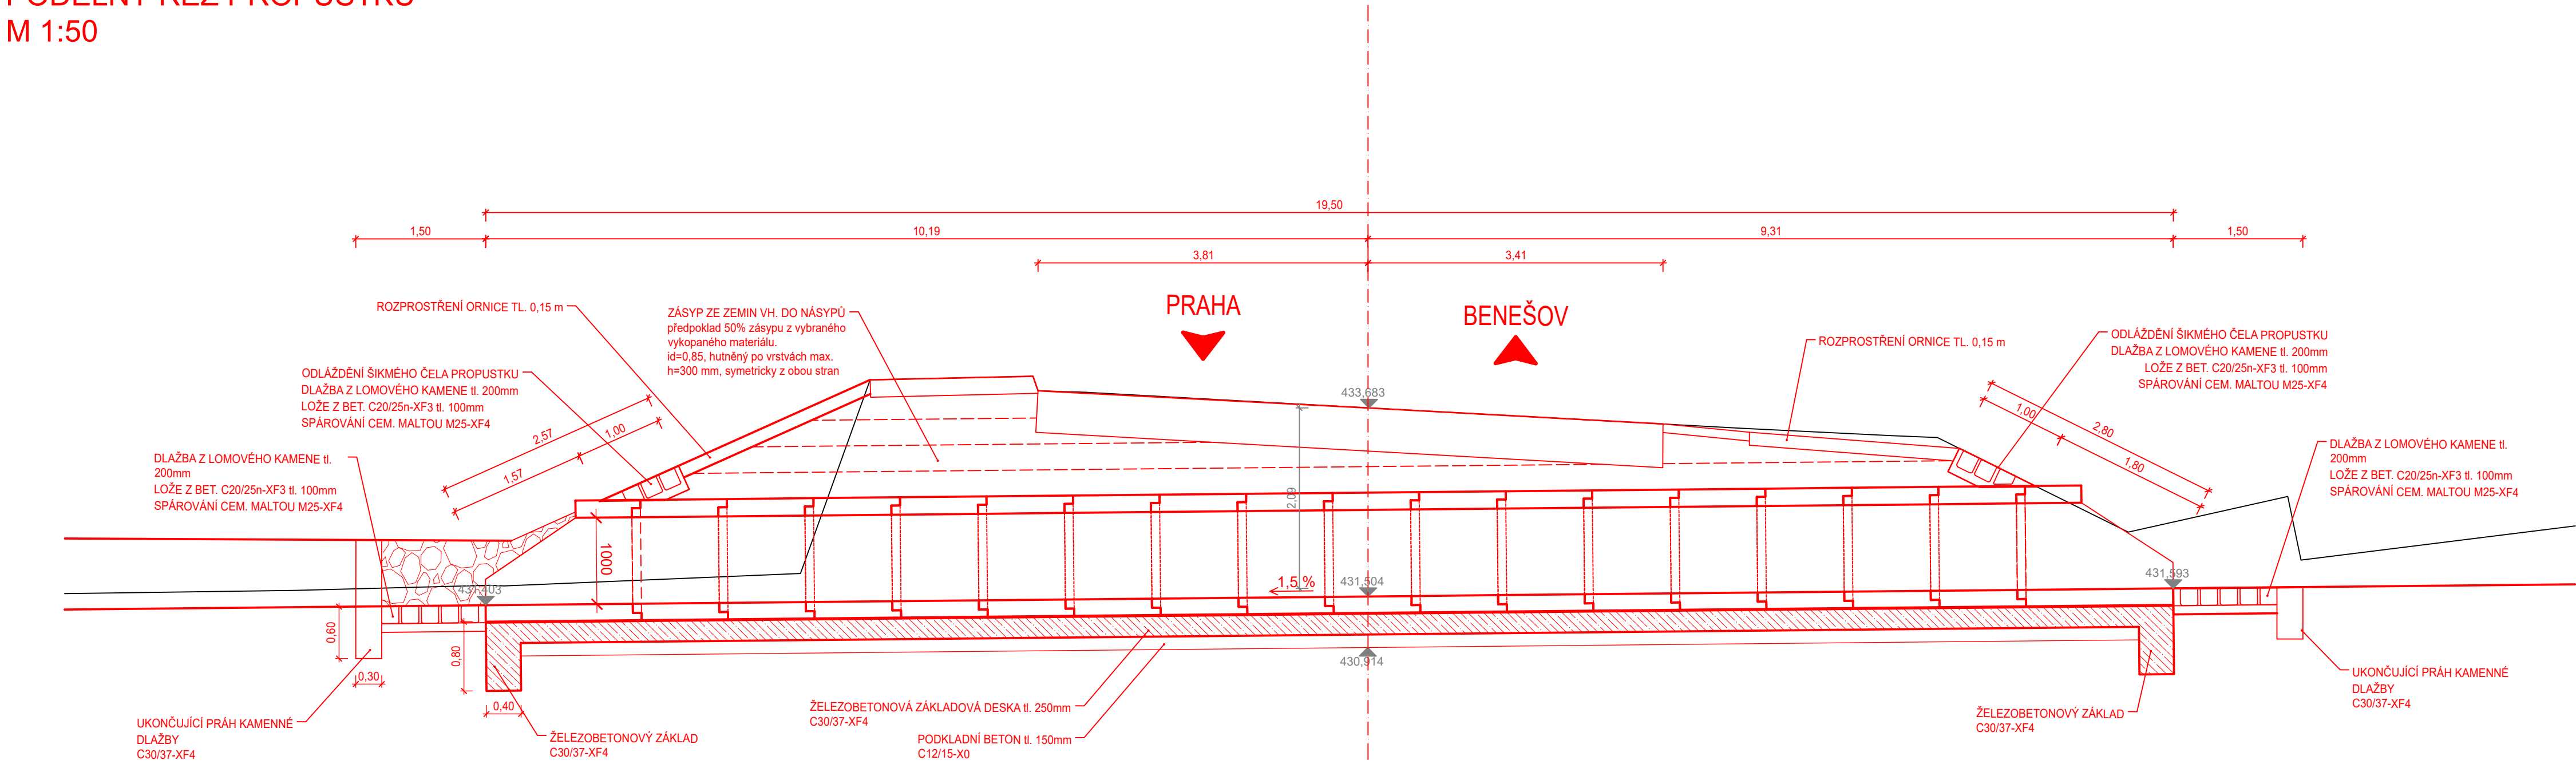

ŘEZ B
M 1:50

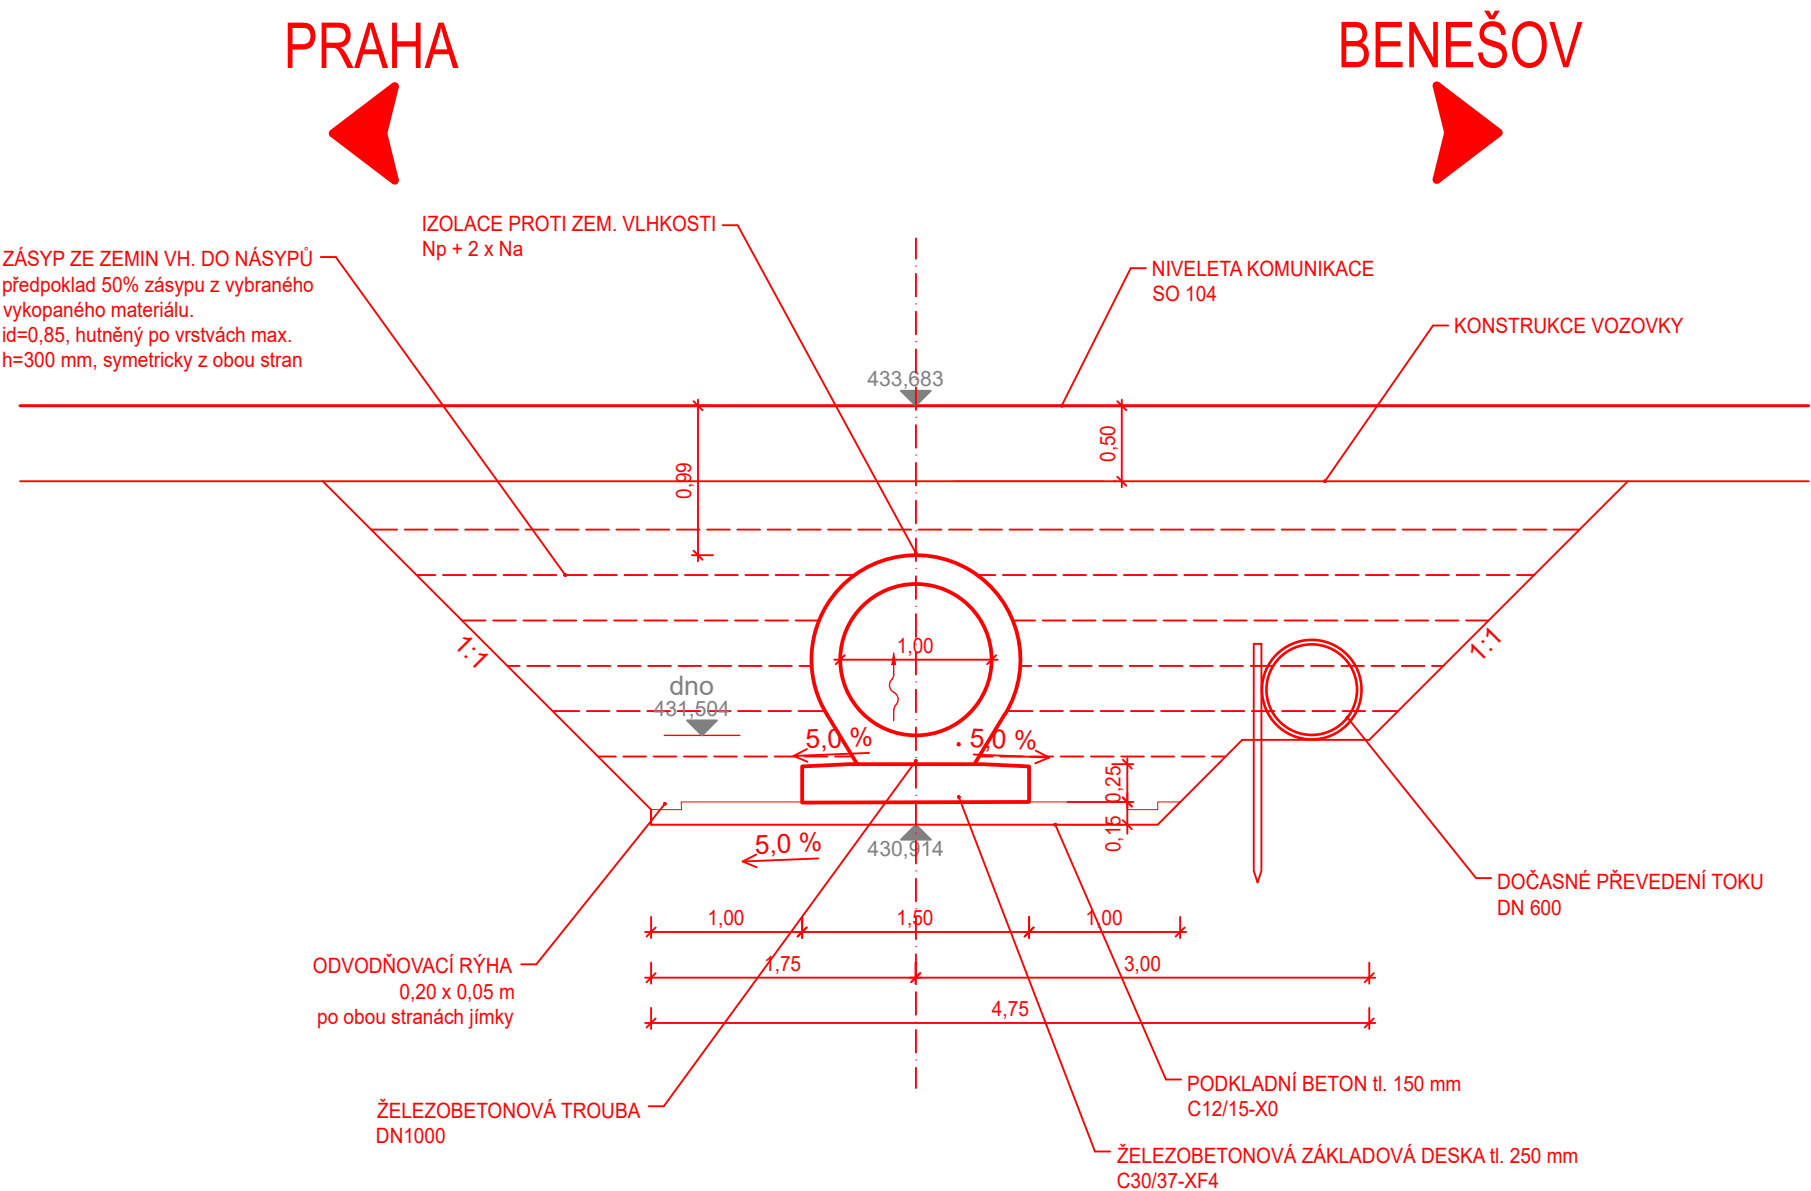

LEGENDA INŽENÝRSKÝCH SÍTÍ:

STÁVAJÍCÍ

- VODOVOD, PŘÍPOJKY
- PODZEMNÍ VEDENÍ NN
- NADZEMNÍ VEDENÍ NN
- PODZEMNÍ VEDENÍ VN
- NADZEMNÍ VEDENÍ VN
- SOĎLOVACÍ VEDENÍ - BEZ ROZLIŠENÍ
- VEREJNÉ OSVĚTLENÍ
- PLYNOVÉ SÍTĚ
- PLYNOVÉ VTL
- KANALIZACE - BEZ ROZLIŠENÍ

POZN. POLOHA INŽ. SÍTÍ JE POLIZE ORIENTAČNÍ. PŘED PROVÁDĚNÍM STAVEBNÍCH PRACÍ JE NEZBYTNÉ PROVĚST VYTÝČENÍ VEŠKERÝCH INŽENÝRSKÝCH SÍTÍ.


POZNÁMKY:

- DEMOLICE STÁVAJÍCÍHO MOSTU JE PŘEDMĚTEM SO 005
- VÝSTAVBA NOVOHO PROPUSTKU BUDE PROBÍHAT ZA ÚPLNÉHO VYLOUČENÍ PROVOZU
- VŠECHNY INŽENÝRSKÉ SÍTĚ BUDOU PŘELOŽENY NEBO OCHRÁNĚNY (viz samostatné tabulní objekty)
- KORYTO VODOTEČE BUDE PROVÍZORNĚ ZATRUBNĚNO
- ODLÁŽENÍ VYTOKU VÝSTOKU PROPUSTKU A KORYTA BUDE KAMENNOU SPÁROVANOU DLAŘBOU II. 200 DO BETONU II. 100 mm. ODLÁŽENÍ UKONČENO BETONOVÝM PRAHEM 300x600 mm. V ODLÁŽENÍ BUDE VYZNAČEN LETOPOČET VÝSTAVBY.

REVIZE:	PŘEDMĚT ZMĚNY:	DATUM:	VYPRACOVAL:
a			
b			
c			
NÁZEV STAVBY: II/603 SULICE - ŽELIVEC, REK. SILNICE A MOSTŮ		ČÍSLO OBJEKTU: SO 105	
INVESTOR STAVBY č.1:  KRAJSKÁ SPRÁVA A ÚDRŽBA SILNIC STŘEDOČESKÉHO KRAJE p.o. Zborovská 81/11, 150 21 Praha 5		RAŽITKO: DATUM: PODPIS:	
INVESTOR STAVBY č.2:  OBEC KAMENICE Ringhofferovo náměstí 434 Olešovice, 251 66 Kamenice		RAŽITKO: DATUM: PODPIS:	
TECHNICKÝ DOZOR INVESTORA  REALSTAV MB, s.r.o. Klaudínova 124, 293 01 Mladá Boleslav		RAŽITKO: KONTROLOVAL: DATUM: PODPIS:	
ZHOTOVITEL STAVBY:  M - SILNICE, a.s. Husova 1697, Bláh Předměstí, 530 03 Pardubice		RAŽITKO: KONTROLOVAL: DATUM: PODPIS:	
KOORDINÁTOR RDS:  M - PROJEKCE, s.r.o. Ressova 956/13, 500 02 Hradec Králové		RAŽITKO: KONTROLOVAL: DATUM: PODPIS:	

SOUDRADNICOVÝ SYSTÉM: S-JTSK
VÝSKOVÝ SYSTÉM: B.P.V.

ČISTOPIS

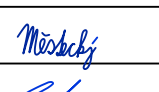NÁZEV STAVBY:				
II/603 SULICE - ŽELIVEC, REKONSTRUKCE SILNICE A MOSTŮ				
ČÁST / STAVEBNÍ OBJEKT:				
SO 104 - SILNICE II/603 ÚSEK 4 - PROPUSTEK 1				
PŘÍLOHA:				
PROPUSTEK 1 - NOVÝ STAV				
ZHOTOVITEL RDS:		HLAVNÍ INŽENÝR PROJEKTU:		PARÉ:
 M - PROJEKCE, s.r.o. Resslova 956/13 500 02 Hradec Králové		Bc. R. MĚSTEČKÝ		
		ZODPOVĚDNÝ PROJEKTANT:		Ing. M. ŠTEJSKAL
		VYPRACOVAL:		Ing. M. ŠPRONGL
		KONTROLA:		Ing. P. KELČA
MĚŘITKO:		Č. ZAKÁZKY:	STUPEŇ:	DATUM:
1:50		25-118-03	RDS	06/2026
				ČÁST:
				104
				PŘÍLOHA:
				6