



SO 103 - KLADEČSKÝ PLÁN
M 1:250

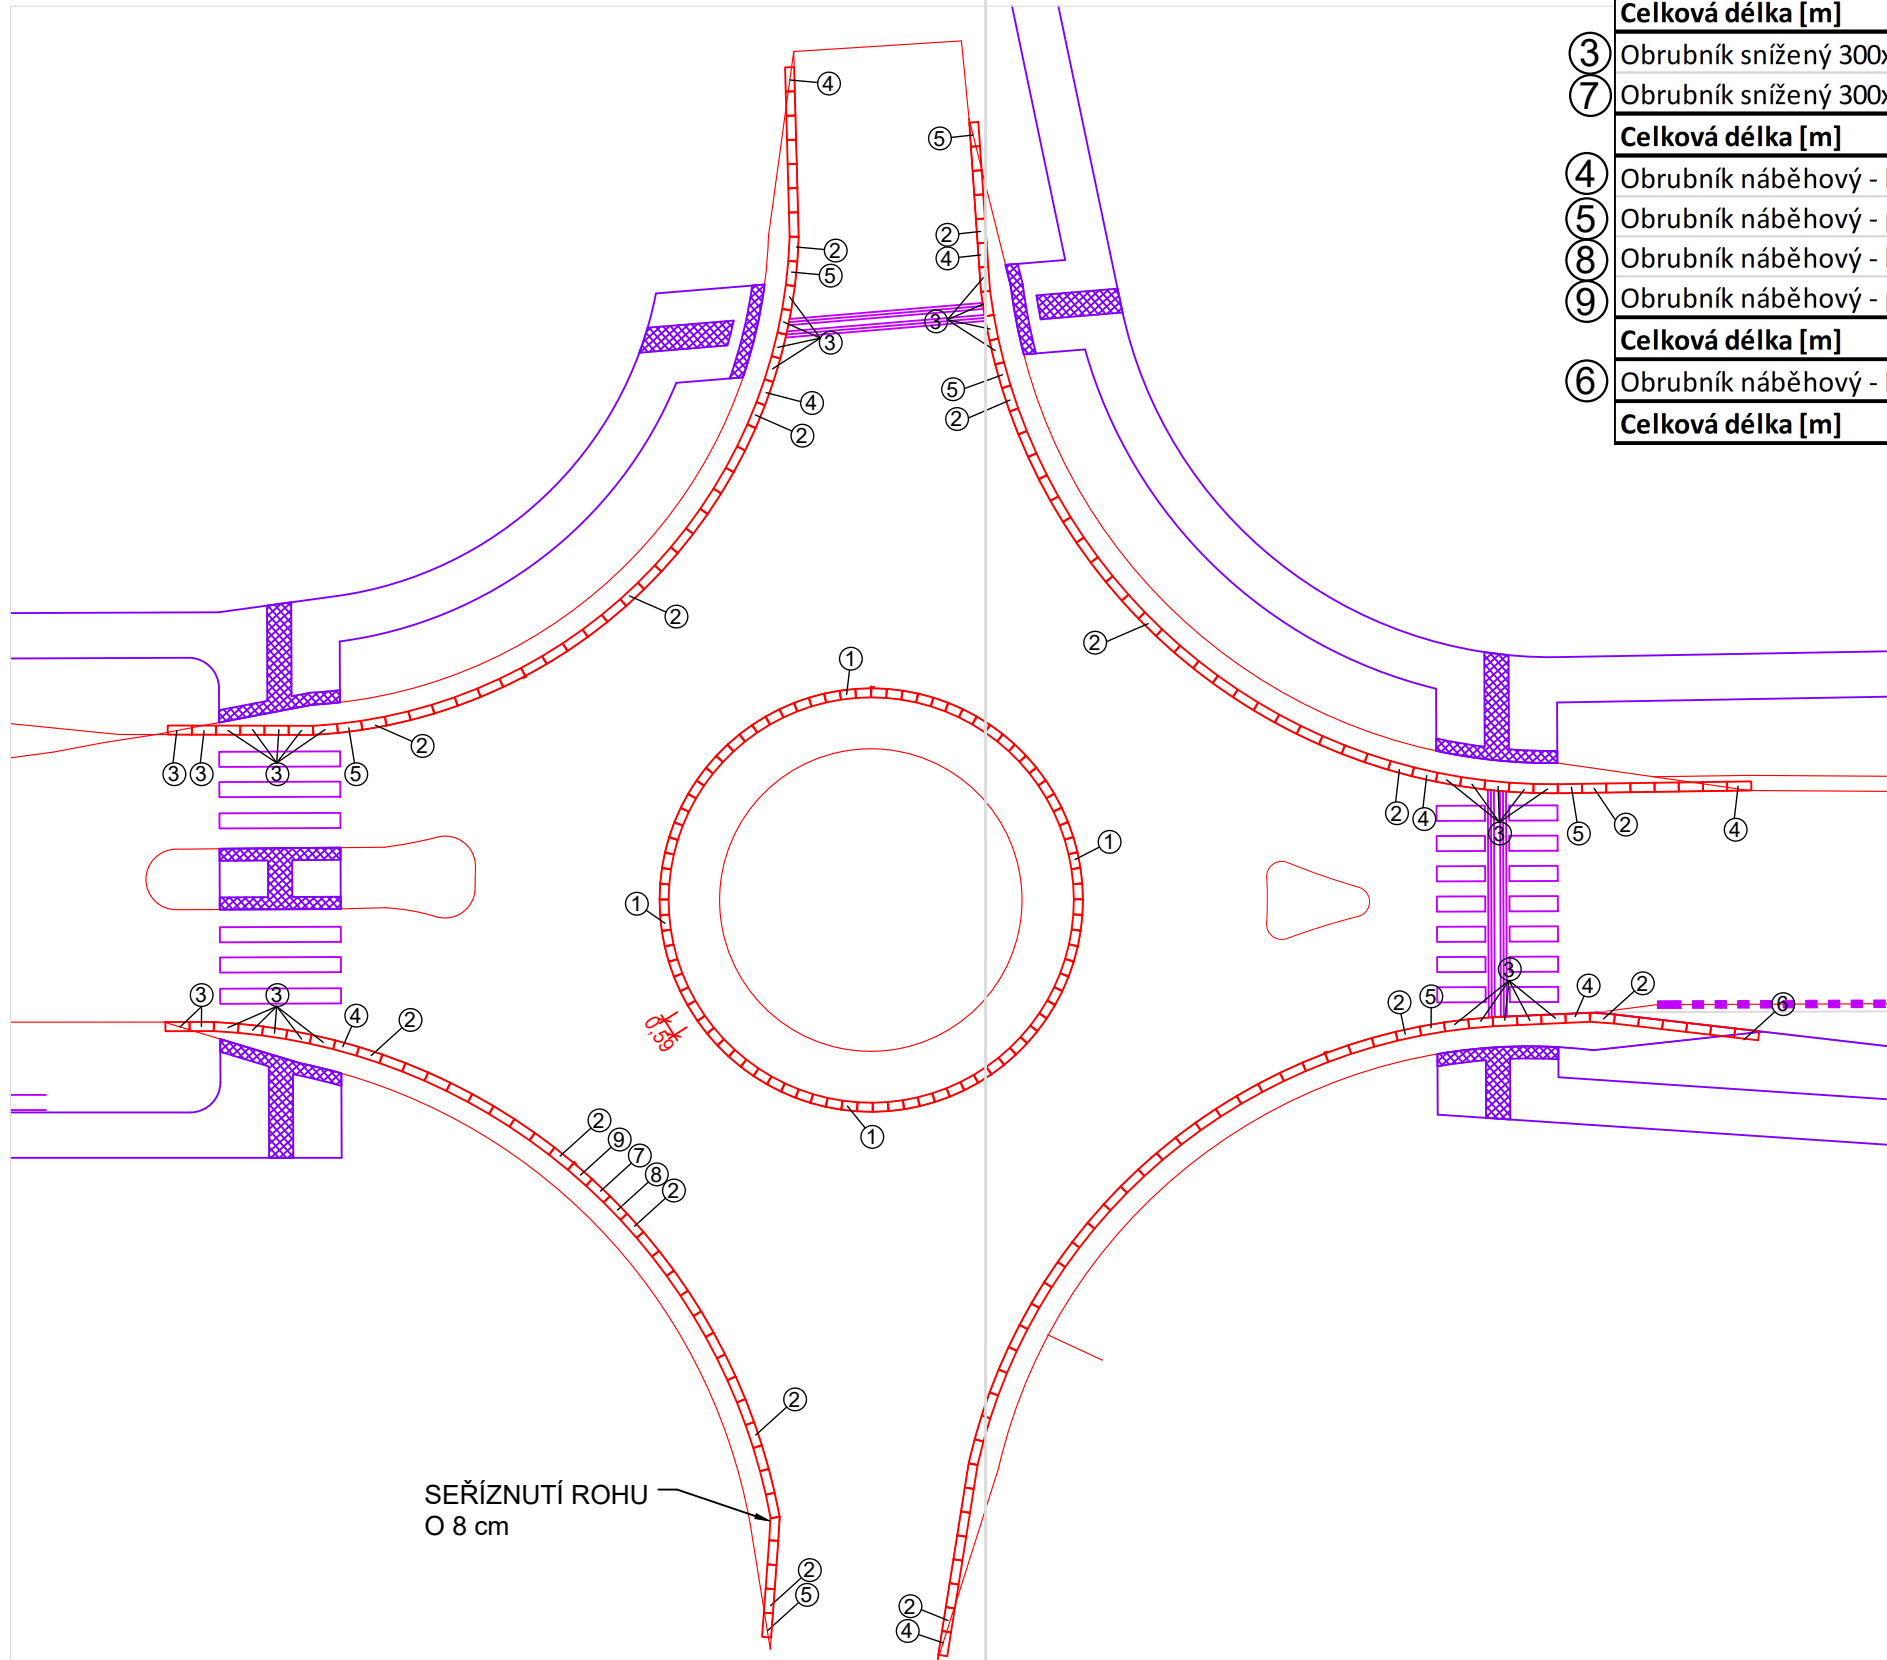


	Obrubník	délka [m]	rádius [m]	počet [ks]
①	Obrubník zkosený	0,50	přímá	83
②		0,59		1
		0,80		131
	Celková délka [m]	146,89		
③	Obrubník snížený 300x160	0,80	přímá	32
⑦	Obrubník snížený 300x140	0,80		1
	Celková délka [m]	26,40		
④	Obrubník náběhový - levý 20-80mm	0,80	přímá	8
⑤	Obrubník náběhový - pravý 20-80mm			7
⑧	Obrubník náběhový - levý 0-80mm			1
⑨	Obrubník náběhový - pravý 0-80mm			1
	Celková délka [m]			13,60
⑥	Obrubník náběhový - levý 120-80mm	0,80	přímá	1
	Celková délka [m]	0,80		

SCHÉMA OBRUBNÍKŮ 1:25

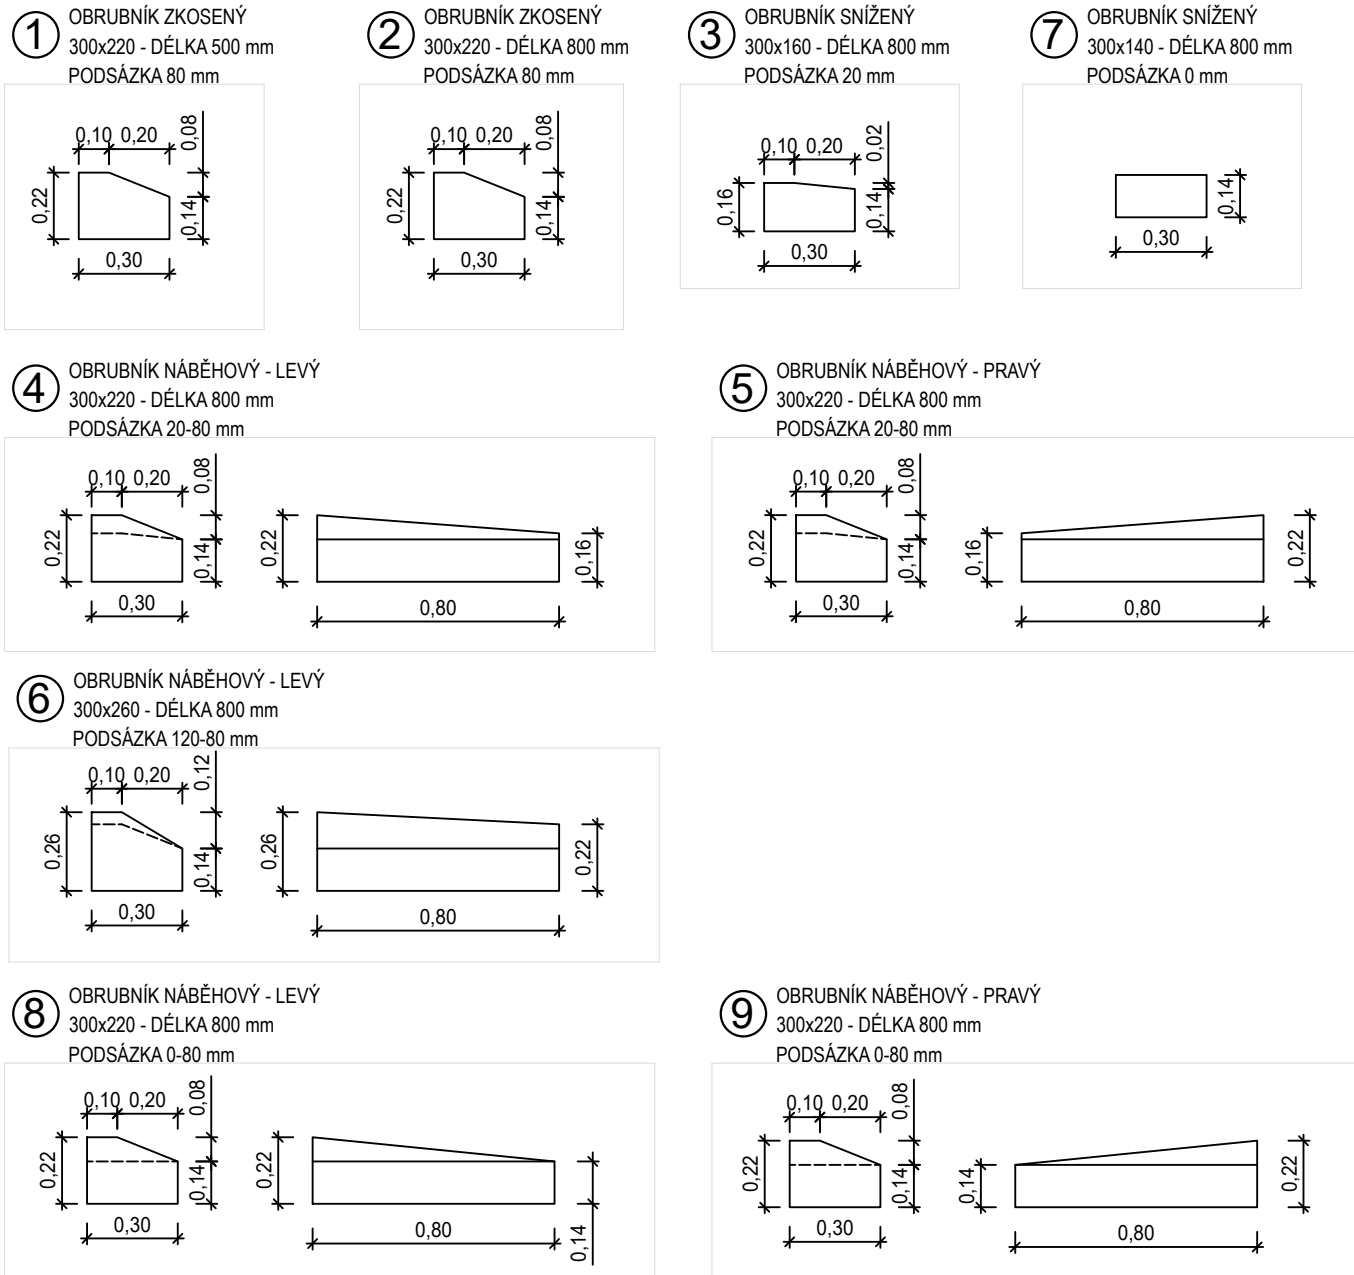

DETAIL SPÁR 1:10

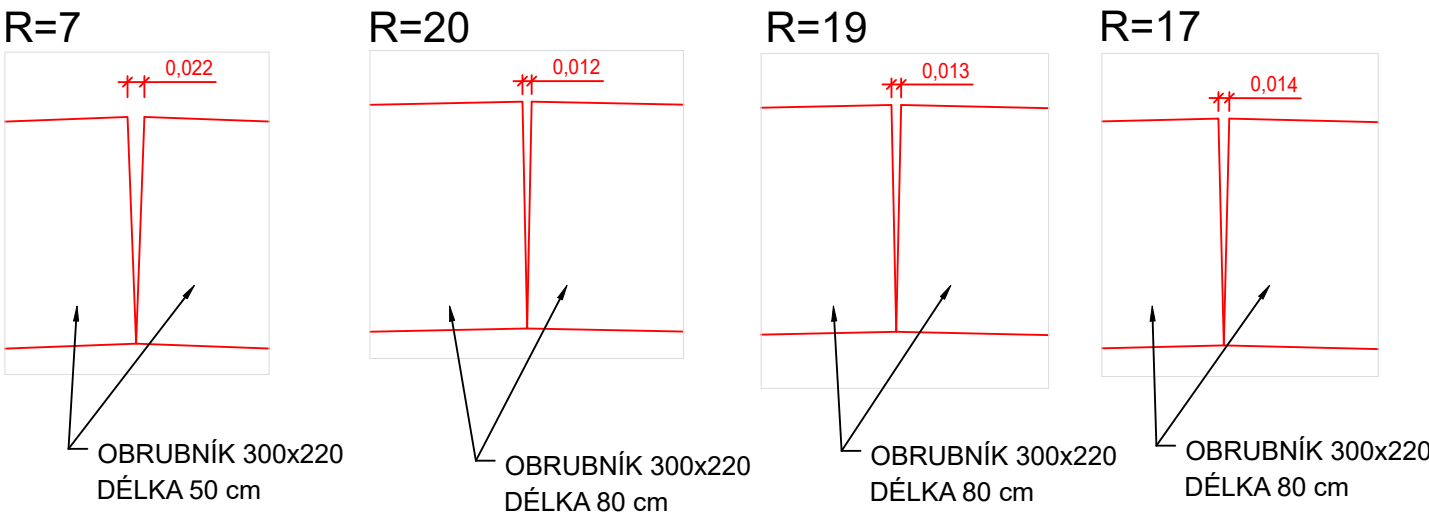

REVIZE:	PŘEDMĚT ZMĚNY:	DATUM:	VYPRACOVAL:
a			
b			
c			

NÁZEV STAVBY: II/603 SULICE - ŽELIVEC, REK. SILNICE A MOSTŮ	ČÍSLO OBJEKTU: SO 103
--	--------------------------

INVESTOR STAVBY č.1:  KRAJSKÁ SPRÁVA A ÚDRŽBA SILNIC STŘEDOČESKÉHO KRAJE p.o. Zborovská 81/11, 150 21 Praha 5	RAZÍTKO:
DATUM:	PODPIS:

INVESTOR STAVBY č.2:  OBEC KAMENICE Ringhofferovo náměstí 434 Olešovice, 251 68 Kamenice	RAZÍTKO:
DATUM:	PODPIS:

TECHNICKÝ DOZOR INVESTORA  REALSTAV MB, s.r.o. Klaudíánova 124, 293 01 Mladá Boleslav	RAZÍTKO:
KONTROLOVAL:	PODPIS:

ZHOTOVITEL STAVBY:  M - SILNICE, a.s. Husova 1697, Bílé Předměstí, 530 03 Pardubice	RAZÍTKO:
KONTROLOVAL:	PODPIS:

KOORDINÁTOR RDS:  M - PROJEKCE, s.r.o. Resslova 956/13, 500 02 Hradec Králové	RAZÍTKO:
KONTROLOVAL:	PODPIS:

SOUŘADNICOVÝ SYSTÉM: S-JTSK
VÝŠKOVÝ SYSTÉM: B.P.V.

KONCEPT

NÁZEV STAVBY:

II/603 SULICE - ŽELIVEC, REKONSTRUKCE SILNICE A MOSTŮ

ČÁST / STAVEBNÍ OBJEKT:

SO 103 - SILNICE II/603 ÚSEK 3 - OKRUŽNÍ KŘÍŽOVATKA

PŘÍLOHA:

KLADEČSKÝ PLÁN

ZHOTOVITEL RDS:



M - PROJEKCE, s.r.o.
Resslova 956/13
500 02 Hradec Králové

HLAVNÍ INŽENÝR PROJEKTU:		Bc. R. MĚSTECKÝ		PARÉ:		
ZODPOVĚDNÝ PROJEKTANT:		Ing. M. STEJSKAL				
VYPRACOVAL:		Bc. R. MĚSTECKÝ				
KONTROLA:		Ing. P. KELČA				
MĚŘÍTKO:		Č. ZAKÁZKY:	STUPEŇ:	DATUM:	ČÁST:	PŘÍLOHA:
1:250	25-118-03	RDS	04/2026	103	-	