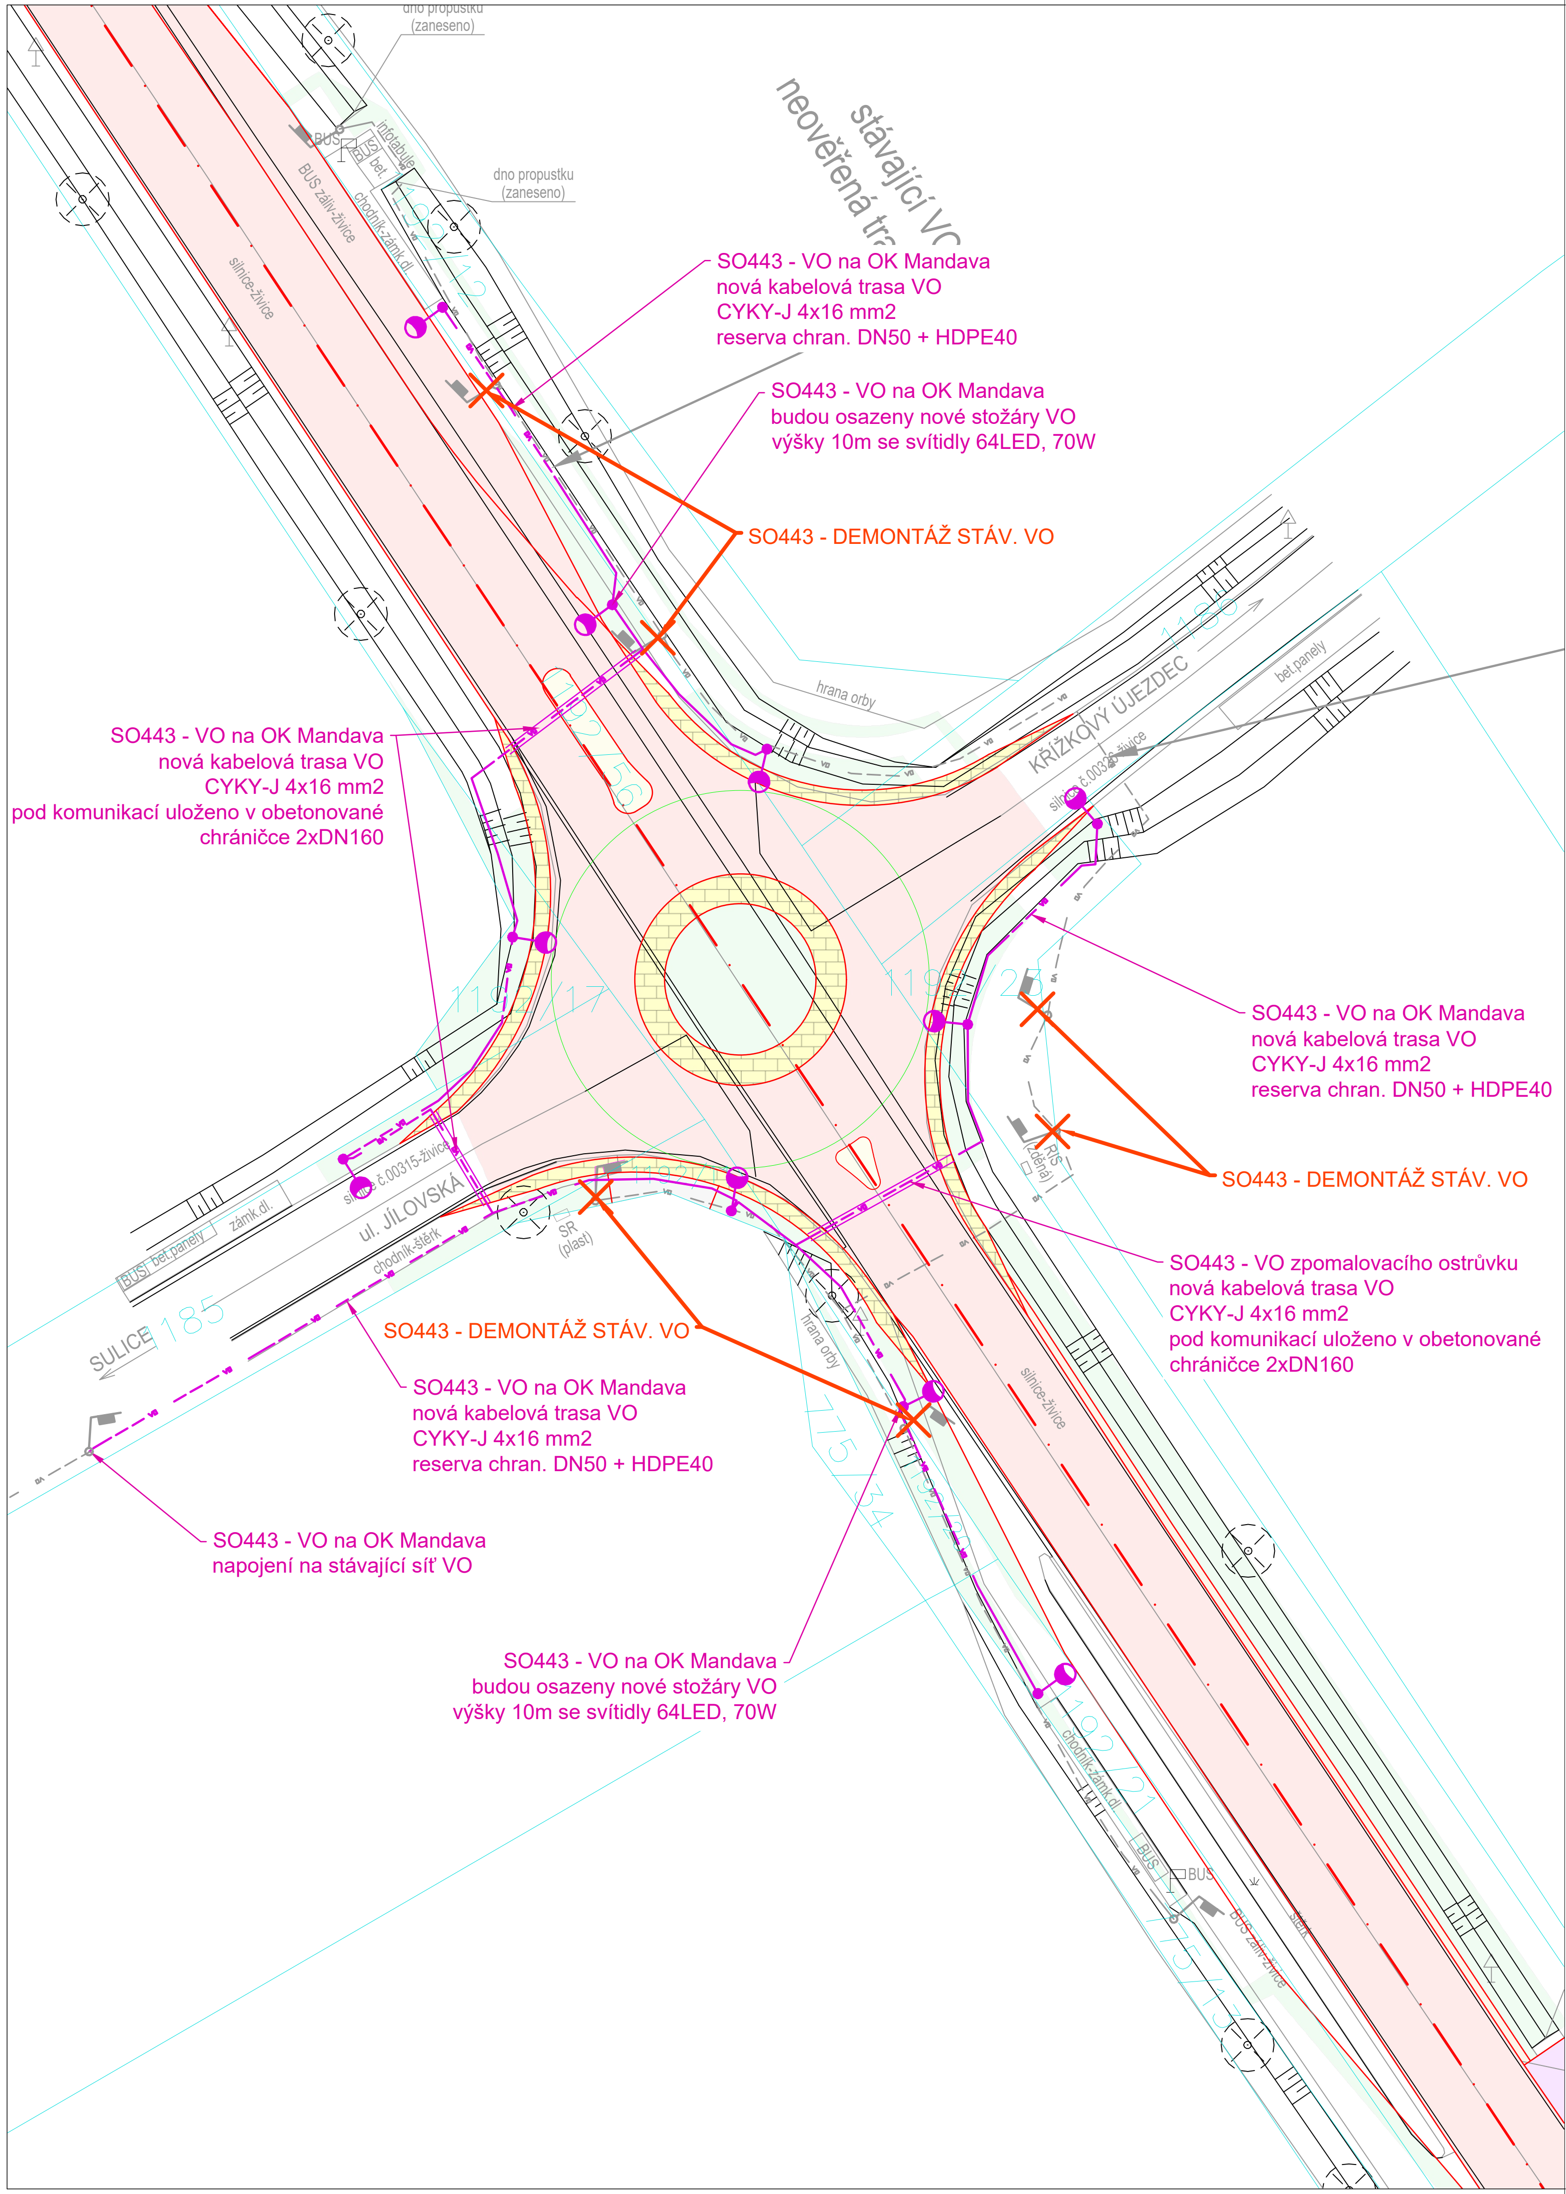

LEGENDA:

Nová kabelová trasa VO - CYKY-J 4x16mm2

Nový stožár VO - výšky 10m (UZN10) s výložníkem osazen LED svítidly AMPERA EVO1 40LED/70W

Č.	Datum	Popis	Vypracoval	Schválil
Č.	Datum	Popis	Vypracoval	Schválil
REVIZE				

Souřadnicový systém S-JTSK, Výškový systém Bpv

Objednatel:

Středočeský kraj
Zborovská 81/11,
150 21 Praha 5

Navrhl/vypracoval:	Zodpovědný projektant:	Zhotovitel:
Ing. Martin Čížek	Ing. Martin Čížek	Mott MacDonald CZ, spol. s.r.o.
Technická kontrola:	Hlavní inženýr projektu:	Národní 984/15, 110 00 Praha 1, +420 221412800
Ing. Martin Čížek	Ing. Dušan Cichra	

Kraj: Středočeský kraj	Čís.sm.obj.: S–1181/DOP/2019
Katastrální území: Sulice[759431], Štiřín[662496], Ládví [5662445]	Čís.akce: 390474
Akce: **II/603 Sulice- Želivec, rekonstrukce silnice a mostů** **SO 443 - Doplnění a úprava VO v úseku 3 - OK**	Datum: 07/2024
	Formát: 2xA4
	Měřítko: 1:500
	Stupeň: PDPS
	Číslo kopie:
Část: **Situace VO**	Číslo přílohy: D.443-2