



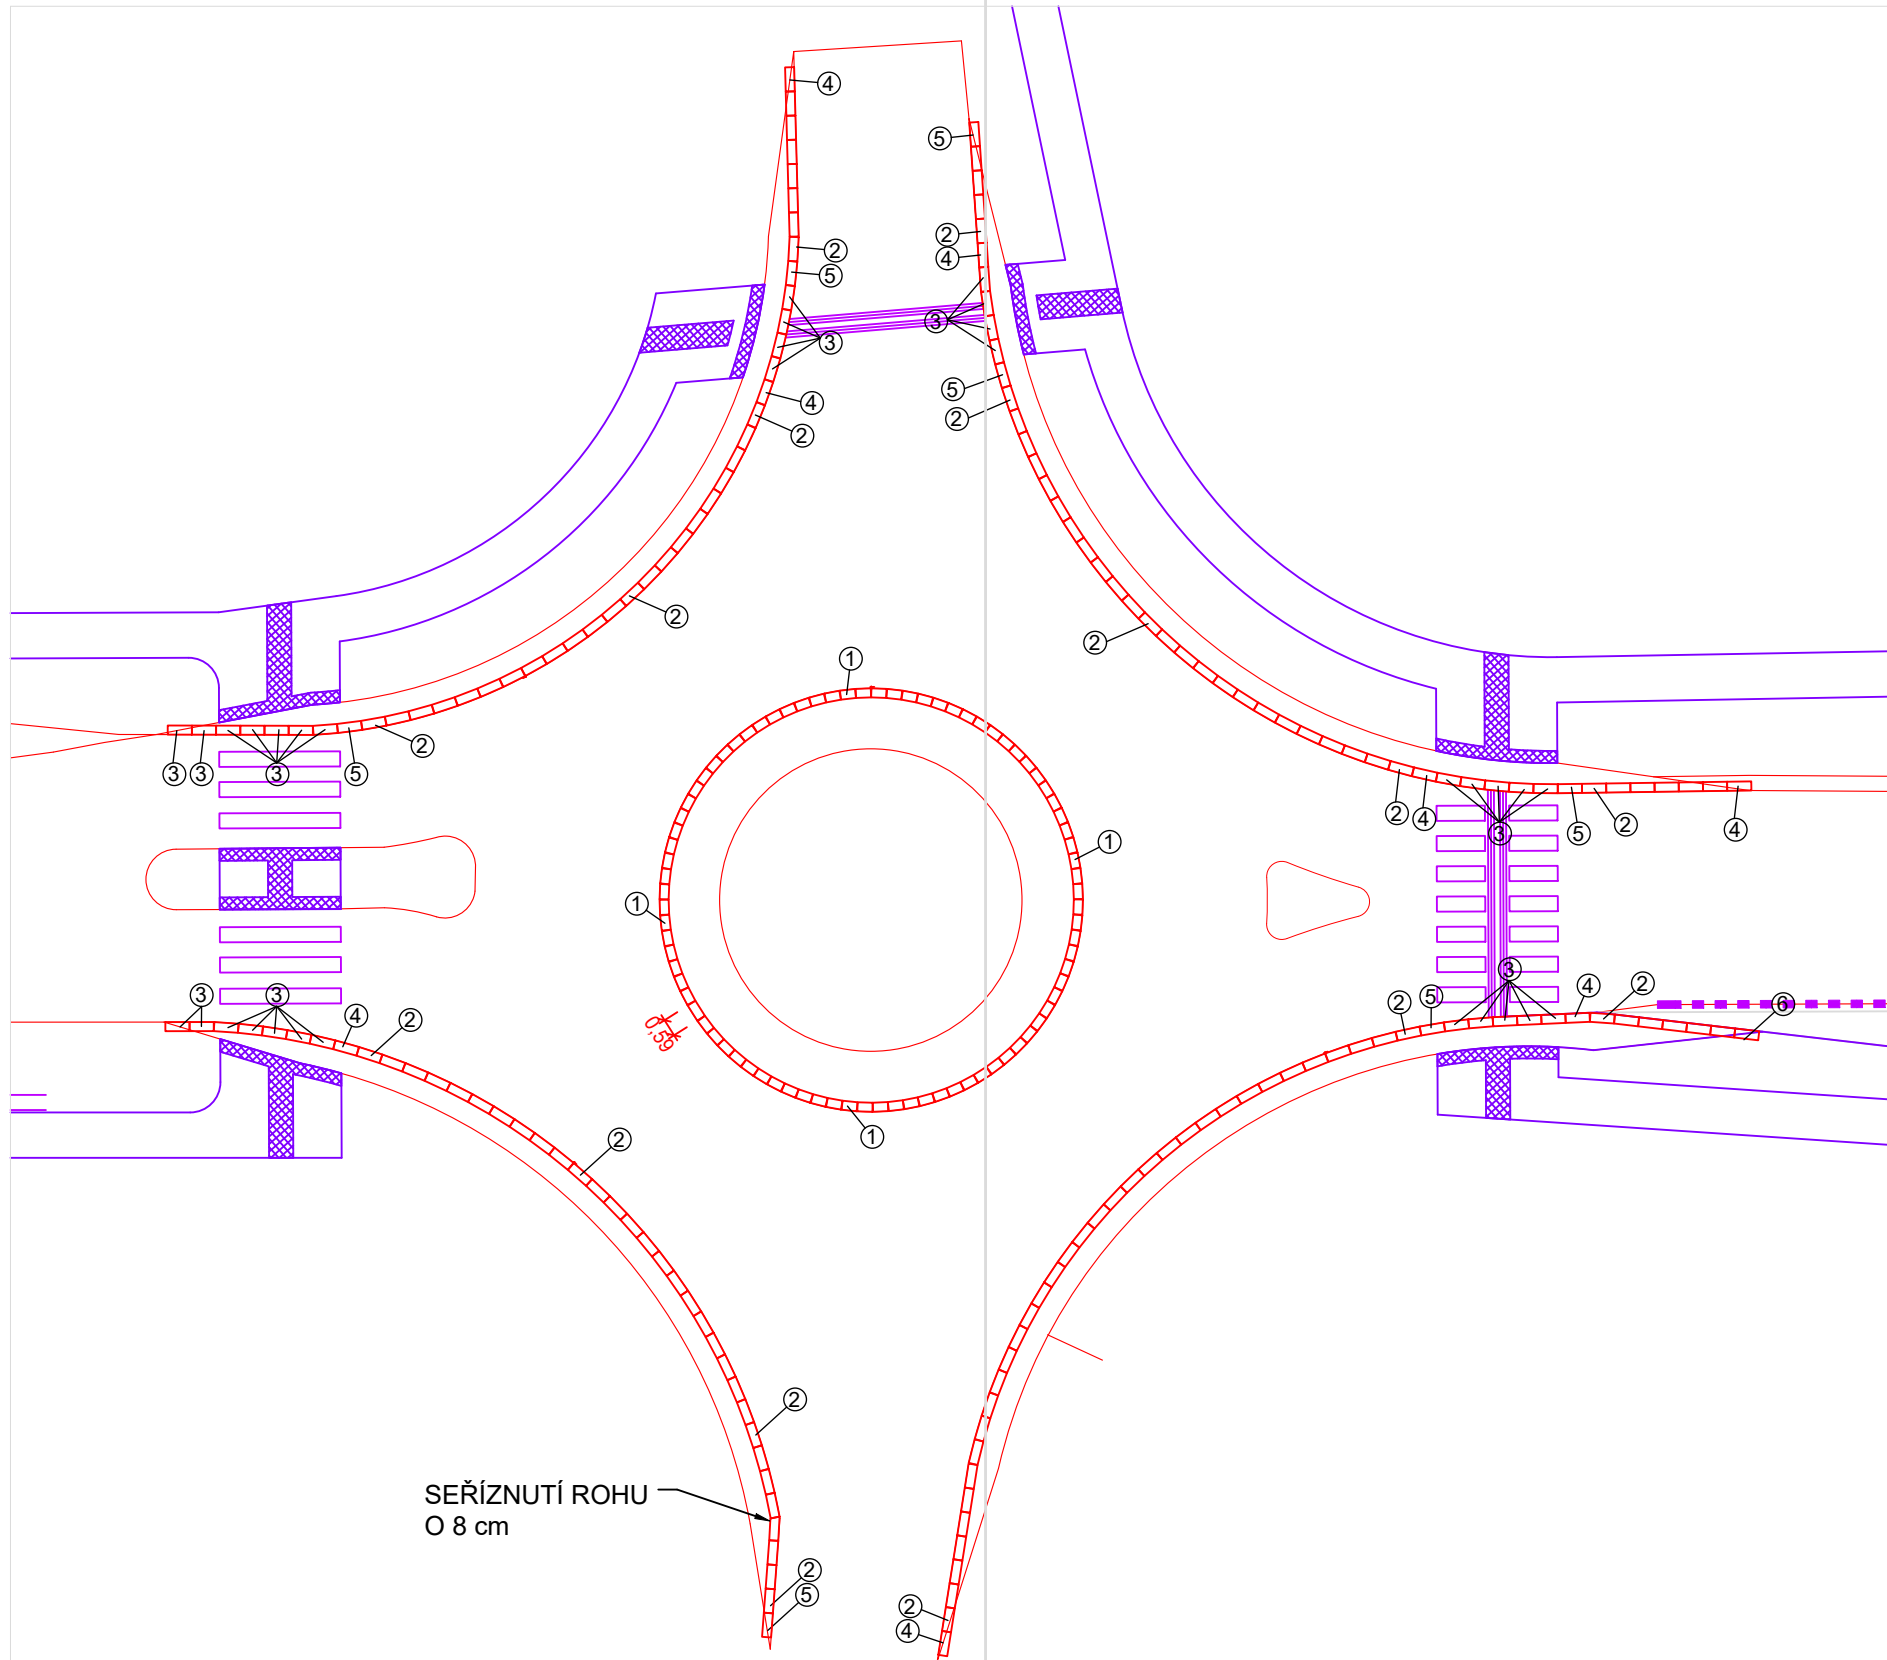


Obrubník	délka [m]	rádius [m]	počet [ks]
Obrubník zkosený	0,50	přímá	83
	0,59		1
	0,80		134
Celková délka [m]	149,29		
Obrubník snížený	0,80	přímá	32
Celková délka [m]	25,60		
Obrubník náběhový - levý	0,80	přímá	8
Obrubník náběhový - pravý			7
Celková délka [m]	12,00		
Obrubník náběhový - levý	0,80	přímá	1
Celková délka [m]	0,8		

SCHÉMA OBRUBNÍKŮ 1:25

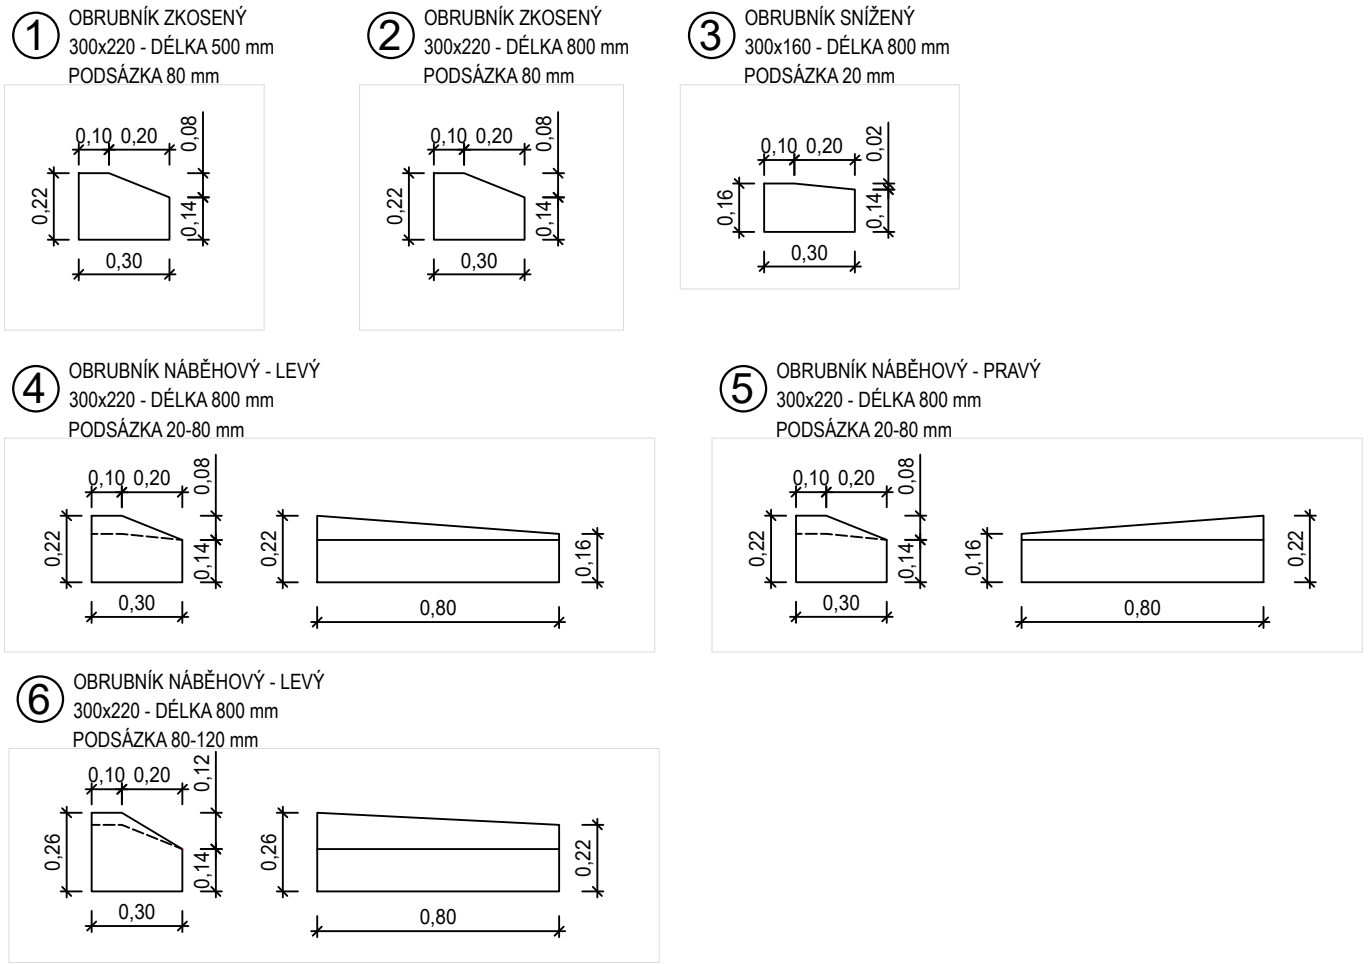



DETAIL SPÁR 1:10

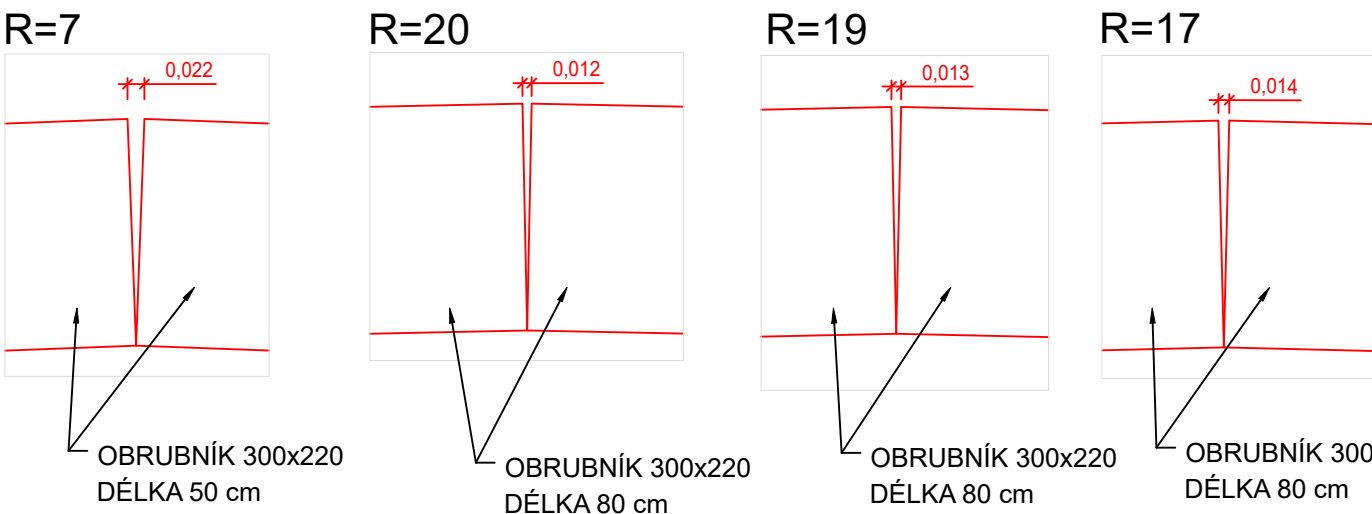

REVIZE:	PŘEDMĚT ZMĚNY:	DATUM:	VYPRACOVAL:
a			
b			
c			
NÁZEV STAVBY: II/603 SULICE - ŽELIVEC, REK. SILNICE A MOSTŮ		ČÍSLO OBJEKTU: SO 103	
INVESTOR STAVBY č.1:  KRAJSKÁ SPRÁVA A ÚDRŽBA SILNIC STŘEDOČESKÉHO KRAJE p.o. Zborovská 81/11, 150 21 Praha 5		RAZÍTKO: DATUM: PODPIS:	
INVESTOR STAVBY č.2:  OBEC KAMENICE Ringhofferovo náměstí 434 Olešovice, 251 68 Kamenice		RAZÍTKO: DATUM: PODPIS:	
TECHNICKÝ DOZOR INVESTORA  REALSTAV MB, s.r.o. Klaudánova 124, 293 01 Mladá Boleslav		RAZÍTKO: KONTROLOVAL: DATUM: PODPIS:	
ZHOTOVITEL STAVBY:  M - SILNICE, a.s. Husova 1697, Bílé Předměstí, 530 03 Pardubice		RAZÍTKO: KONTROLOVAL: DATUM: PODPIS:	
KOORDINÁTOR RDS:  M - PROJEKCE, s.r.o. Resslova 956/13, 500 02 Hradec Králové		RAZÍTKO: KONTROLOVAL: DATUM: PODPIS:	

SOUŘADNICOVÝ SYSTÉM: S-JTSK
VÝŠKOVÝ SYSTÉM: B.P.V.

KONCEPT

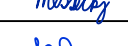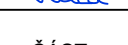NÁZEV STAVBY: II/603 SULICE - ŽELIVEC, REKONSTRUKCE SILNICE A MOSTŮ					
ČÁST / STAVEBNÍ OBJEKT: SO 103 - SILNICE II/603 ÚSEK 3 - OKRUŽNÍ KŘÍŽOVATKA					
PŘÍLOHA: KLADEČSKÝ PLÁN					
ZHOTOVITEL RDS:  M - PROJEKCE, s.r.o. Resslova 956/13 500 02 Hradec Králové	HLAVNÍ INŽENÝR PROJEKTU:	Bc. R. MĚSTECKÝ		PARÉ:	
	ZODPOVĚDNÝ PROJEKTANT:	Ing. M. STEJSKAL			
	VYPRACOVAL:	Bc. R. MĚSTECKÝ			
	KONTROLA:	Ing. P. KELČA			
	MĚŘÍTKO:	Č. ZAKÁZKY:	STUPEŇ:	DATUM:	ČÁST:
1:250	25-118-03	RDS	04/2026	103	-