



SO 103 - KLADEČSKÝ PLÁN
M 1:250

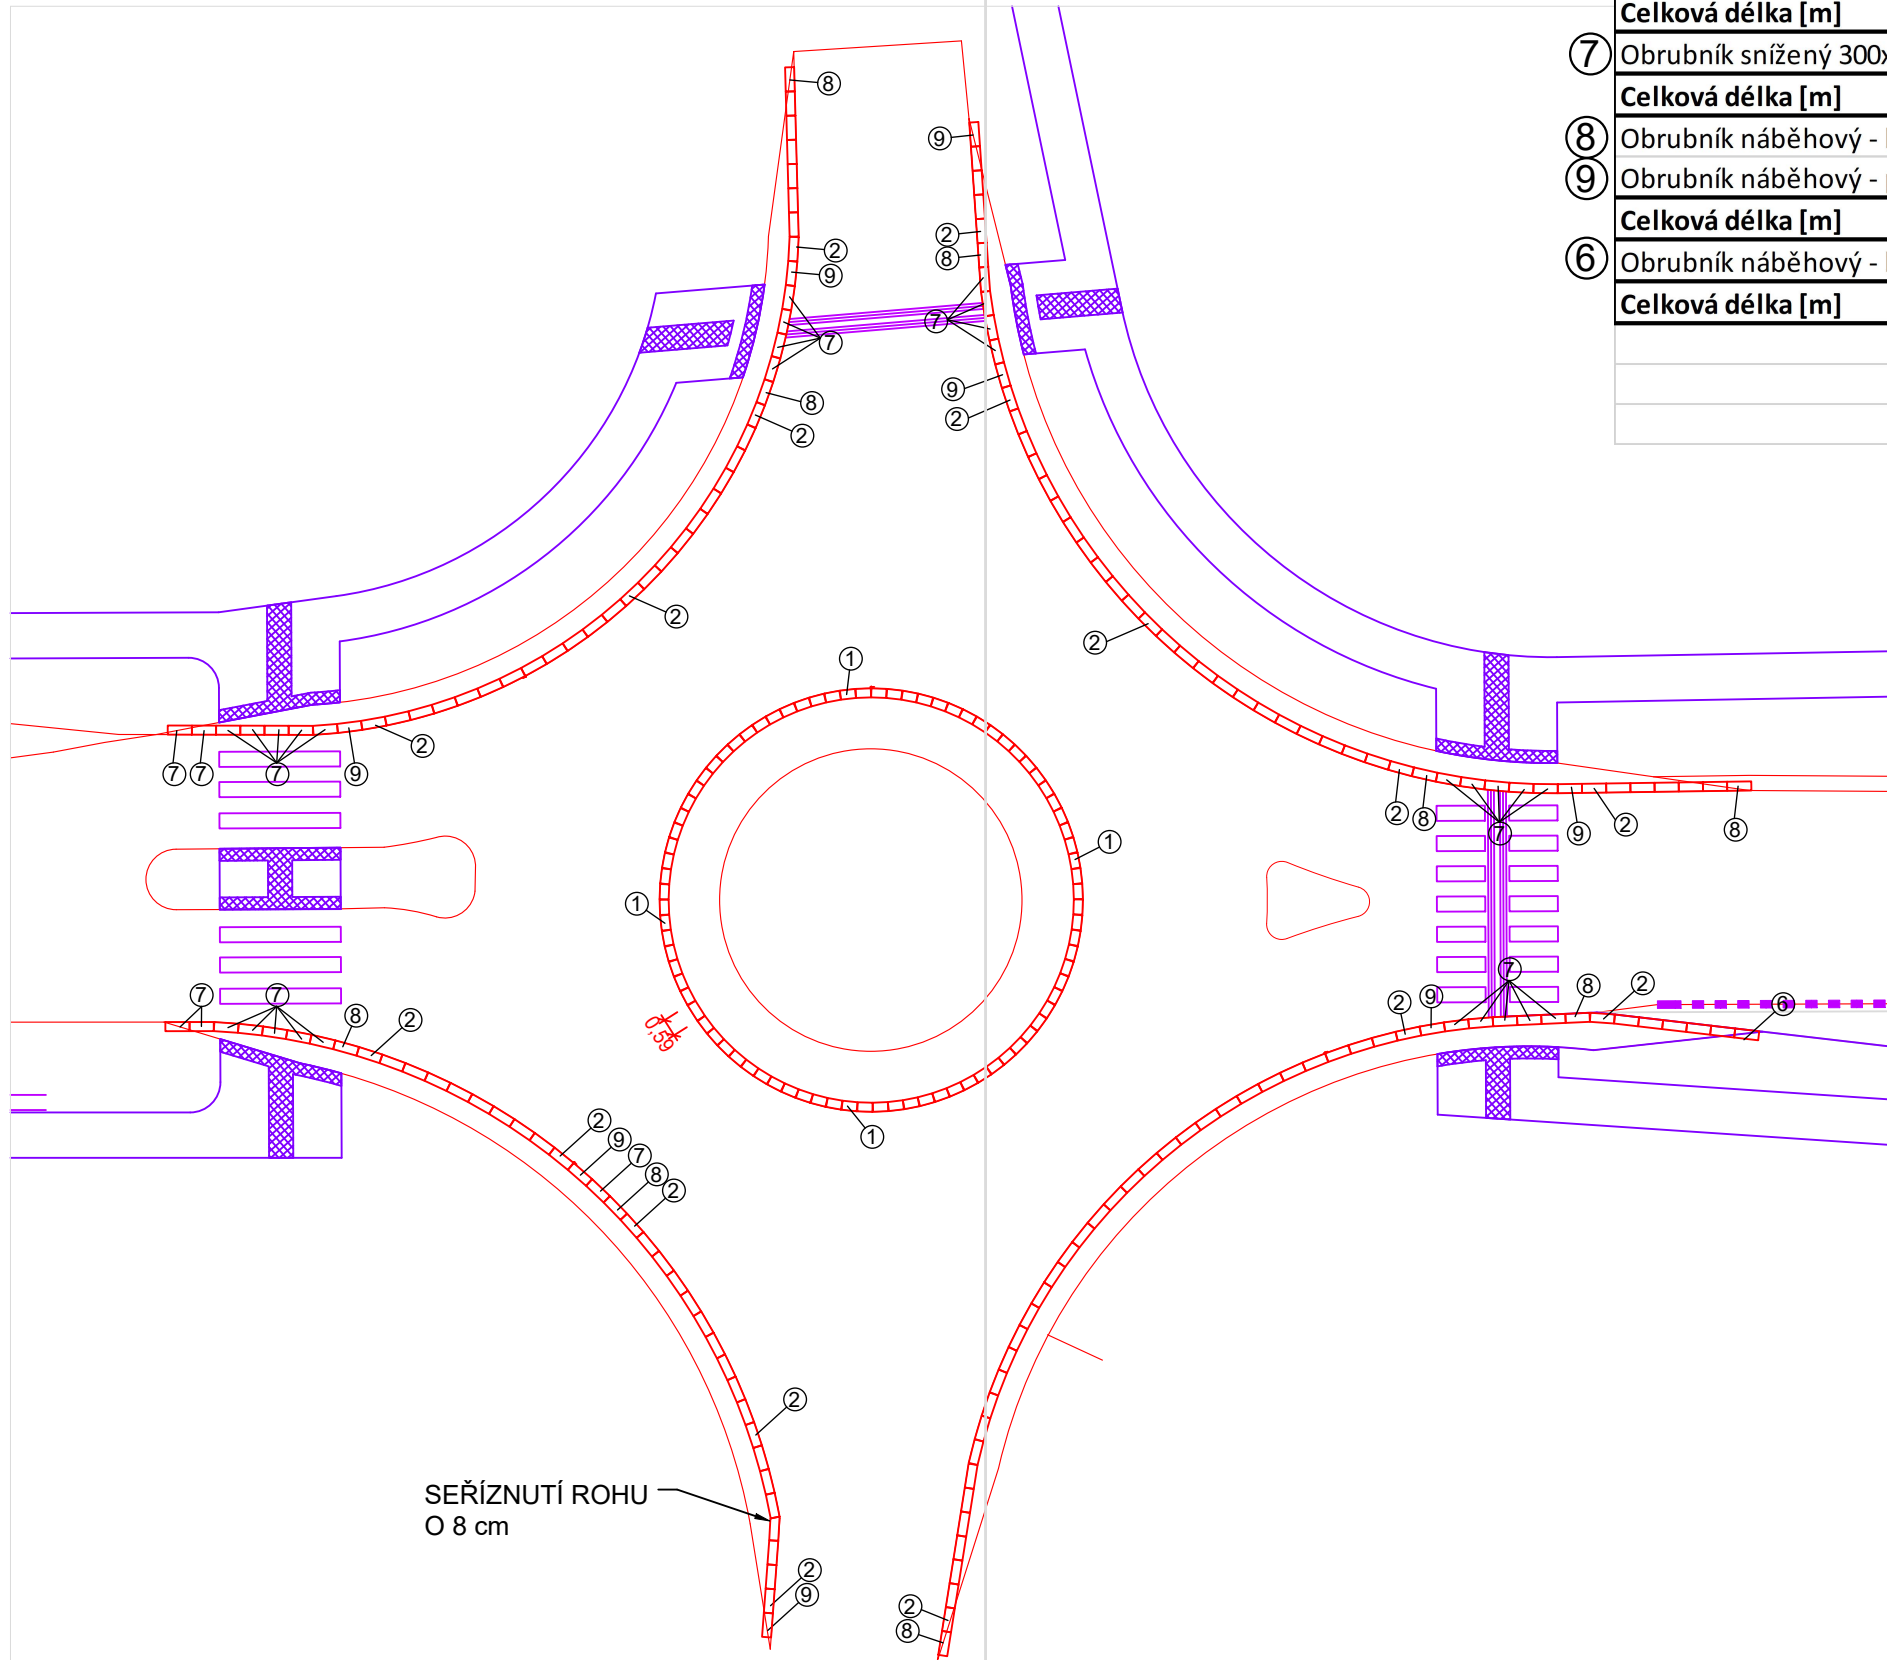


Obrubník	délka [m]	rádius [m]	počet [ks]
①	0,50		83
Obrubník zkosený	0,59	přímá	1
②	0,80		131
Celková délka [m]		146,89	
⑦	0,80	přímá	33
Celková délka [m]		26,40	
⑧	0,80	přímá	9
⑨	0,80	přímá	8
Celková délka [m]		13,60	
⑥	0,80	přímá	1
Celková délka [m]		0,80	

SCHÉMA OBRUBNÍKŮ 1:25


① OBRUBNÍK ZKOSENÝ
300x220 - DÉLKA 500 mm
PODSÁZKA 80 mm

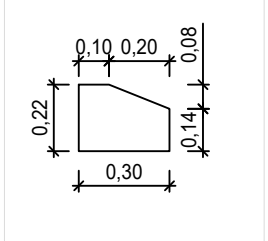


② OBRUBNÍK ZKOSENÝ
300x220 - DÉLKA 800 mm
PODSÁZKA 80 mm

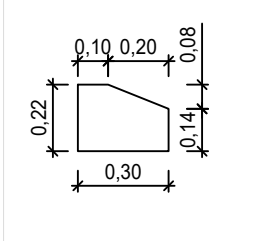


⑦ OBRUBNÍK SNÍŽENÝ
300x140 - DÉLKA 800 mm
PODSÁZKA 0 mm

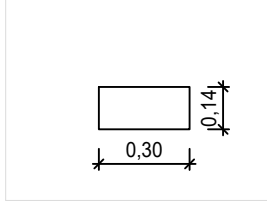

⑥ OBRUBNÍK NÁBĚHOVÝ - LEVÝ
300x260 - DÉLKA 800 mm
PODSÁZKA 120-80 mm

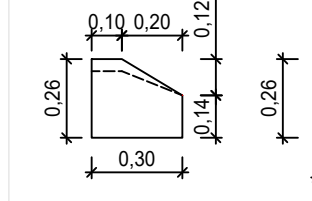


⑧ OBRUBNÍK NÁBĚHOVÝ - LEVÝ
300x220 - DÉLKA 800 mm
PODSÁZKA 0-80 mm

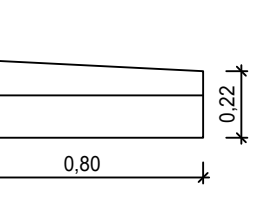


⑨ OBRUBNÍK NÁBĚHOVÝ - PRAVÝ
300x220 - DÉLKA 800 mm
PODSÁZKA 0-80 mm



⑧ OBRUBNÍK NÁBĚHOVÝ - LEVÝ
300x220 - DÉLKA 800 mm
PODSÁZKA 0-80 mm

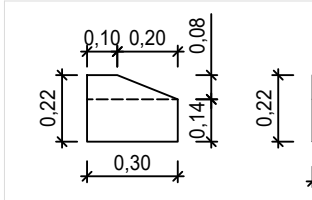


⑨ OBRUBNÍK NÁBĚHOVÝ - PRAVÝ
300x220 - DÉLKA 800 mm
PODSÁZKA 0-80 mm

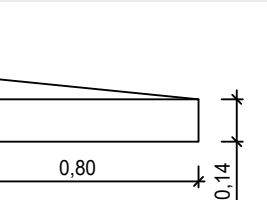

DETAIL SPÁR 1:10

R=7

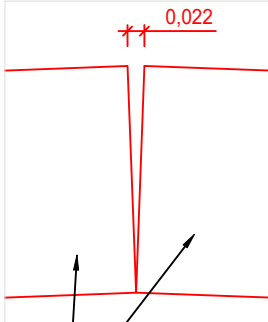


OBRUBNÍK 300x220
DÉLKA 50 cm

R=20




OBRUBNÍK 300x220
DÉLKA 80 cm

R=19

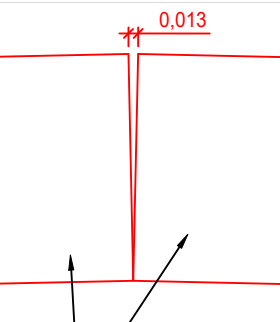

OBRUBNÍK 300x220
DÉLKA 80 cm

R=17

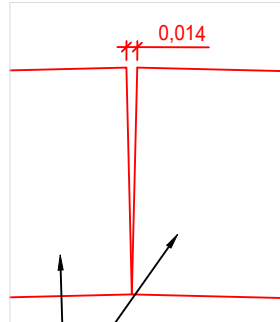

OBRUBNÍK 300x220
DÉLKA 80 cm

REVIZE:	PŘEDMĚT ZMĚNY:	DATUM:	VYPRACOVAL:
a			
b			
c			

NÁZEV STAVBY: II/603 SULICE - ŽELIVEC, REK. SILNICE A MOSTŮ	ČÍSLO OBJEKTU: SO 103
--	--------------------------

INVESTOR STAVBY č.1:  KRAJSKÁ SPRÁVA A ÚDRŽBA SILNIC STŘEDOČESKÉHO KRAJE p.o. Zborovská 81/11, 150 21 Praha 5	RAZÍTKO: DATUM: PODPIS:
---	--------------------------------

INVESTOR STAVBY č.2:  OBEC KAMENICE Ringhofferovo náměstí 434 Olešovice, 251 68 Kamenice	RAZÍTKO: DATUM: PODPIS:
--	--------------------------------

TECHNICKÝ DOZOR INVESTORA  REALSTAV MB, s.r.o. Klaudíánova 124, 293 01 Mladá Boleslav	RAZÍTKO: KONTROLOVAL: DATUM: PODPIS:
--	--




ZHOTOVITEL STAVBY:  M - SILNICE, a.s. Husova 1697, Bílé Předměstí, 530 03 Pardubice	RAZÍTKO: KONTROLOVAL: DATUM: PODPIS:
--	--

KOORDINÁTOR RDS:  M - PROJEKCE, s.r.o. Resslova 956/13, 500 02 Hradec Králové	RAZÍTKO: KONTROLOVAL: DATUM: PODPIS:
--	--

SOUŘADNICOVÝ SYSTÉM: S-JTSK

VÝŠKOVÝ SYSTÉM: B.P.V.

KONCEPT

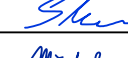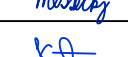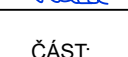NÁZEV STAVBY: II/603 SULICE - ŽELIVEC, REKONSTRUKCE SILNICE A MOSTŮ					
ČÁST / STAVEBNÍ OBJEKT: SO 103 - SILNICE II/603 ÚSEK 3 - OKRUŽNÍ KŘÍŽOVATKA					
PŘÍLOHA: KLADEČSKÝ PLÁN					
ZHOTOVITEL RDS:  M - PROJEKCE, s.r.o. Resslova 956/13 500 02 Hradec Králové	HLAVNÍ INŽENÝR PROJEKTU:	Bc. R. MĚSTECKÝ		PARÉ:	
	ZODPOVĚDNÝ PROJEKTANT:	Ing. M. STEJSKAL			
	VYPRACOVAL:	Bc. R. MĚSTECKÝ			
	KONTROLA:	Ing. P. KELČA			
	MĚŘÍTKO:	Č. ZAKÁZKY:	STUPEŇ:	DATUM:	ČÁST:
1:250		25-118-03	RDS	04/2026	103
					-